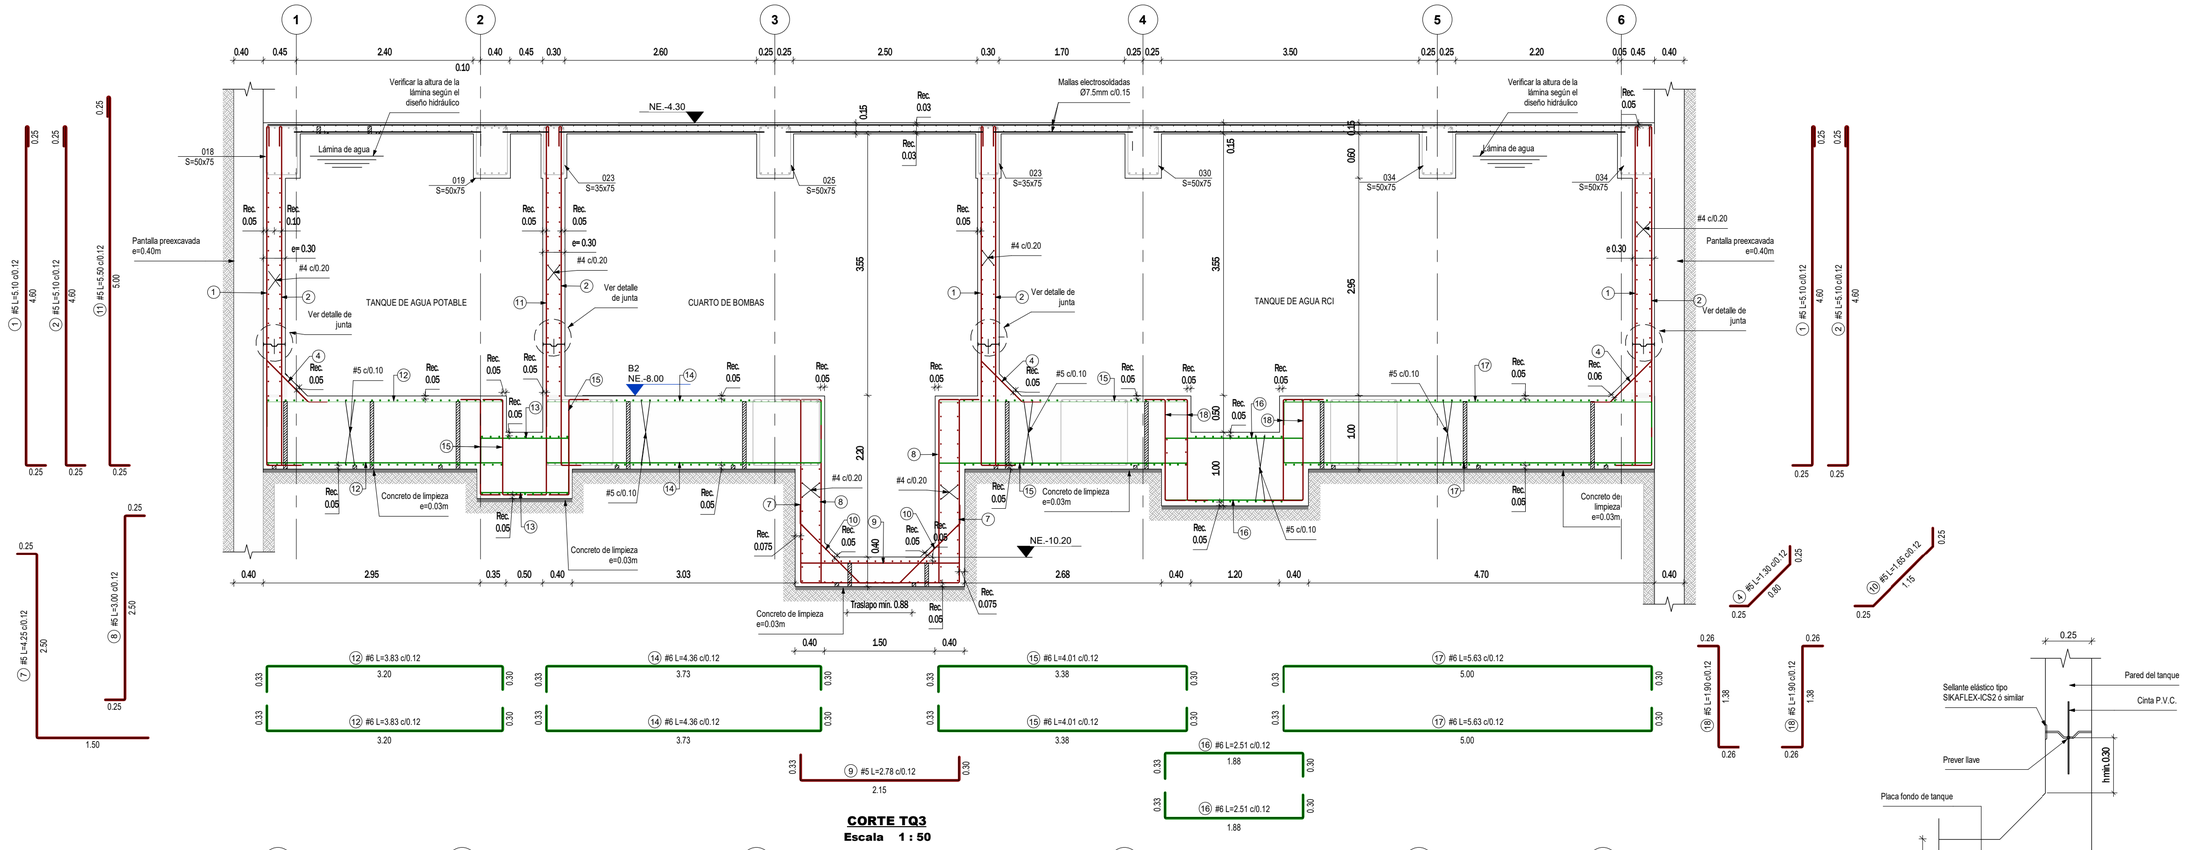

CORTE TQ3
Escala 1 : 50

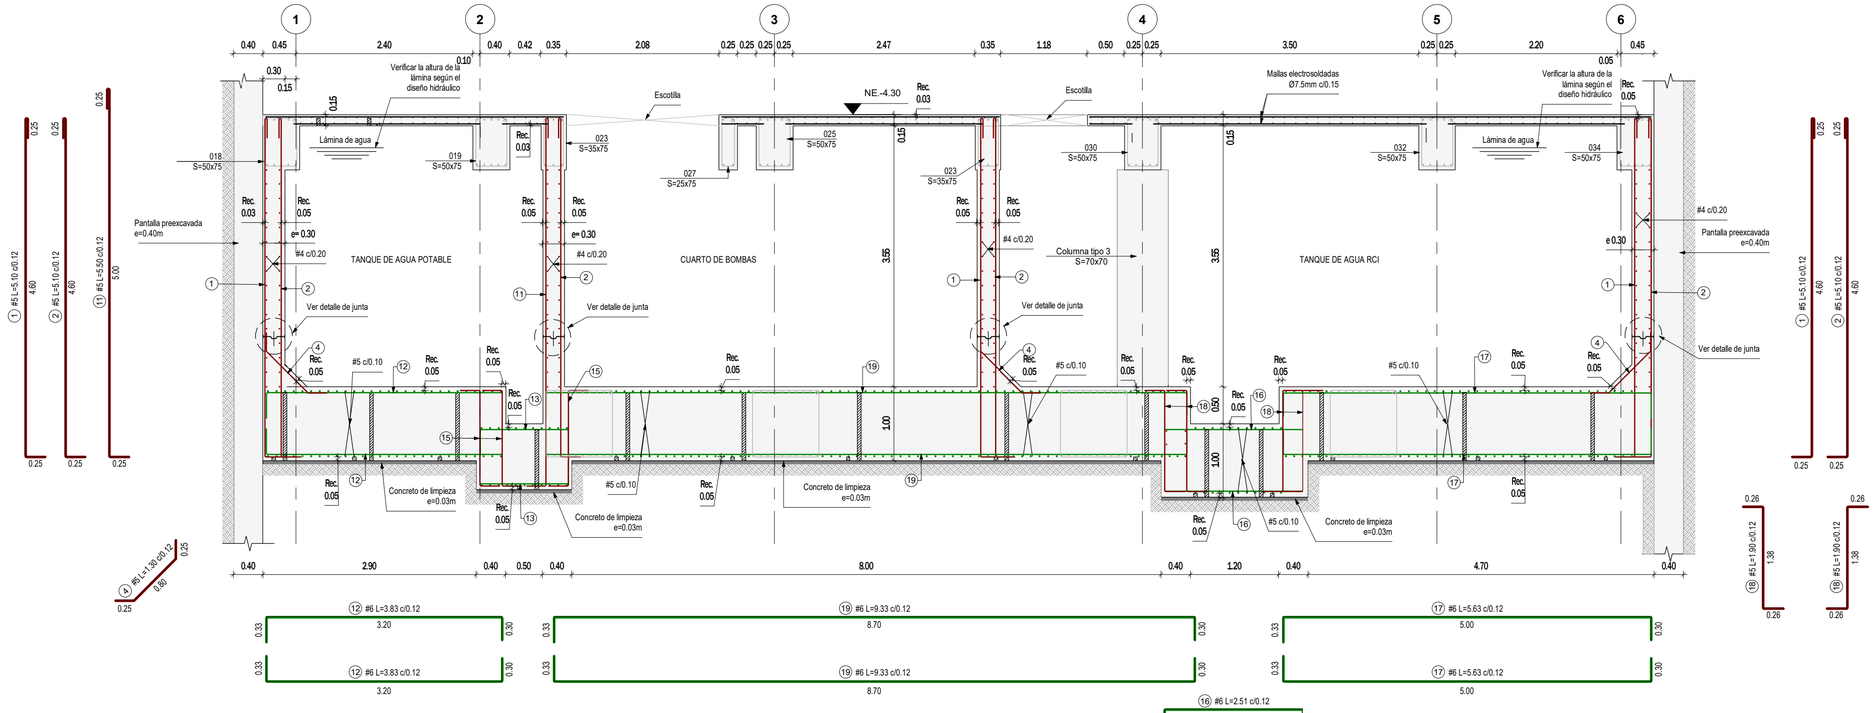

CORTE TQ4
Escala 1 : 50

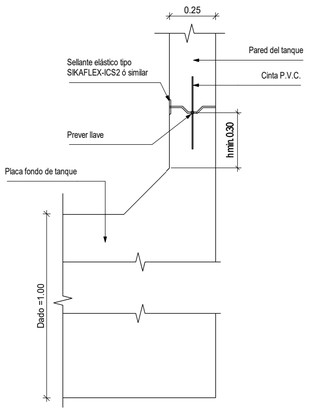

JUNTA MURO TANQUE
Escala 1 : 20

NOTAS

1. Ver detalles generales en el PL. N° 01.02
2. Ver planta de localización de pilotes plano PL. N°05.00
3. Ver despiece de vigas en el PL N° 16.00

CONCRETO

PILOTES	DADOS	TANQUE
f'c=35 MPa	f'c=35 MPa	f'c=35 MPa
f'c=350 kg/cm²	f'c=350 kg/cm²	f'c=350 kg/cm²
f'c=3000 psi	f'c=5000 psi	f'c=5000 psi

NOTA:
Este plano debe ser revisado y aprobado por el Ingeniero de suelos.

VºBº INGENIERO DE SUELOS

VERSIÓN : 0

PLANO Nº 16.01

Aycardi Estructural

GERENTE DE PROYECTO
LUIS ENRIQUE AYCARDI F.
MAT. 2520212794 CND

INGENIERO
DANIEL E. QUICANO C.

MODELADOR
PAULA ANDREA MONTOYA RENDÓN

MODIFICACIONES	FECHA
Emisión Inicial	21-11-2025

HUMANISE STUDIO

EAN-0519- AES-01-EST

Calle 71 #9-84

CORTES TANQUE DE AGUA

EAN-0519 -AES-01-EST-B2-PL-581 16.01

REVISOR ESTRUCTURAL
JULIO CESAR SANMIGUEL CAMACHO
MAT. 25202-57738 CND

PLANO Nº 16.01 VERSIÓN : 0