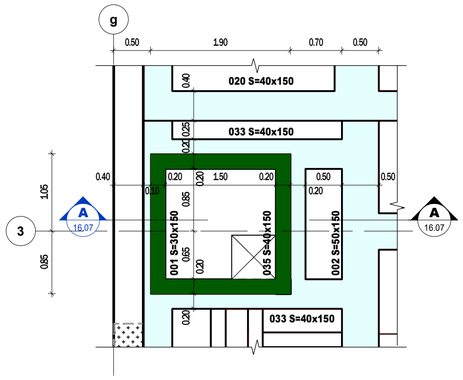

PLANTA DE POZO
CIMENTACIÓN 1
Escala 1 : 50

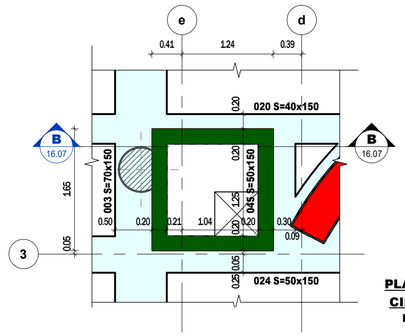

PLANTA DE POZO
CIMENTACIÓN 2
Escala 1 : 50

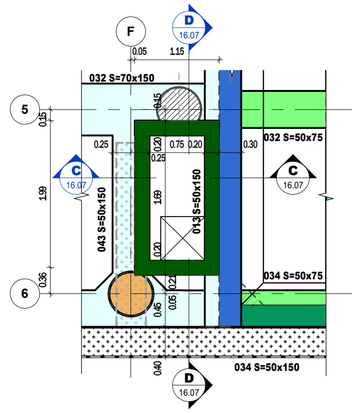

PLANTA DE POZO
CIMENTACIÓN 3
Escala 1 : 50

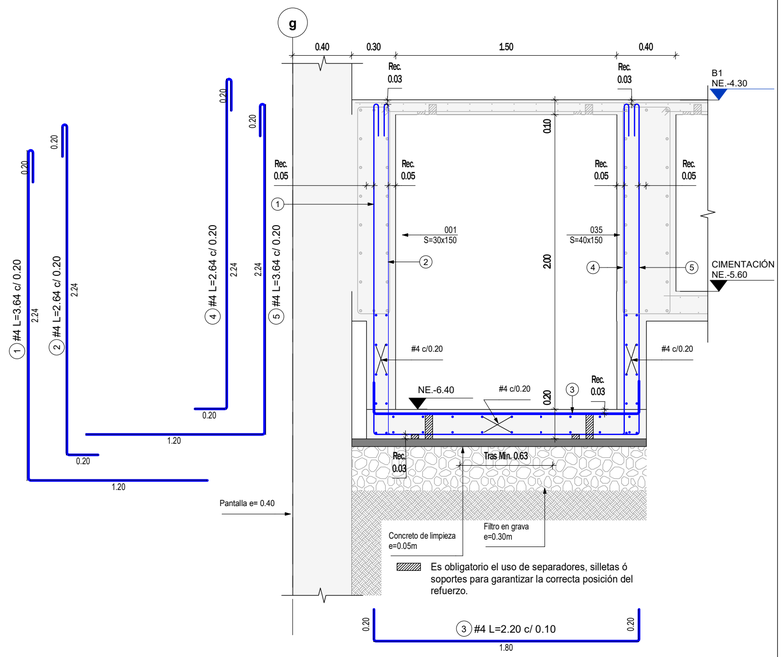

CORTE A-A
Escala 1 : 25

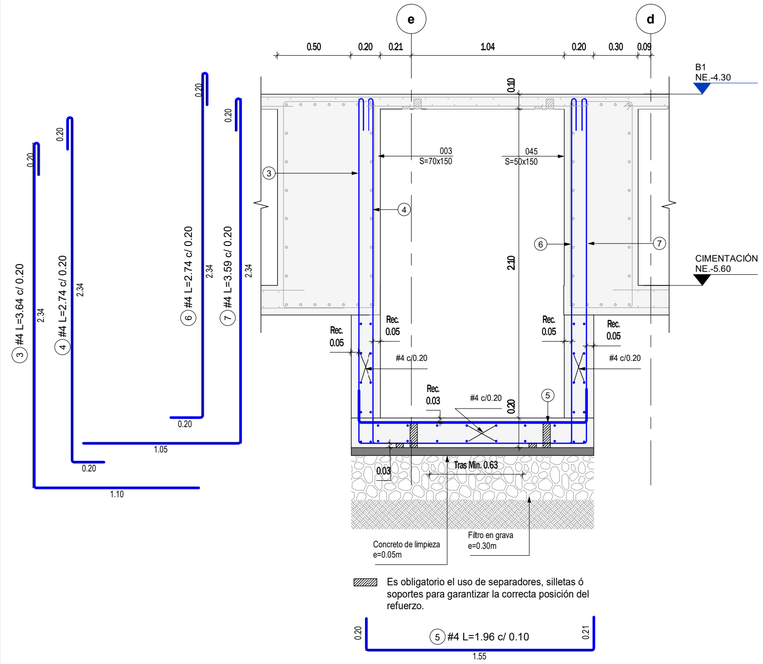

CORTE B-B
Escala 1 : 25

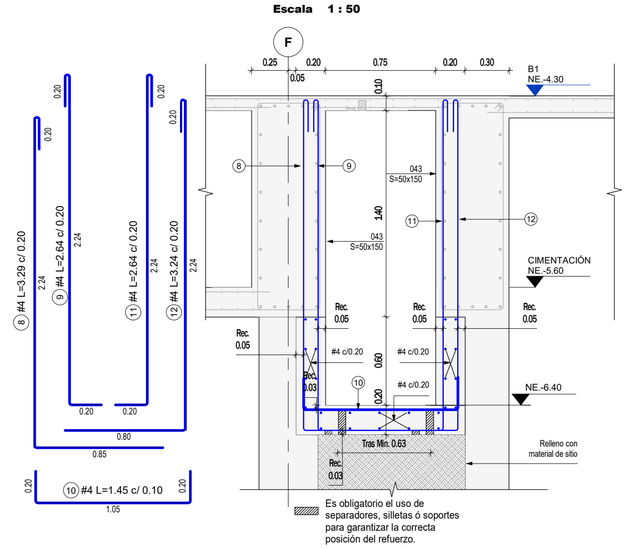

CORTE C-C
Escala 1 : 25

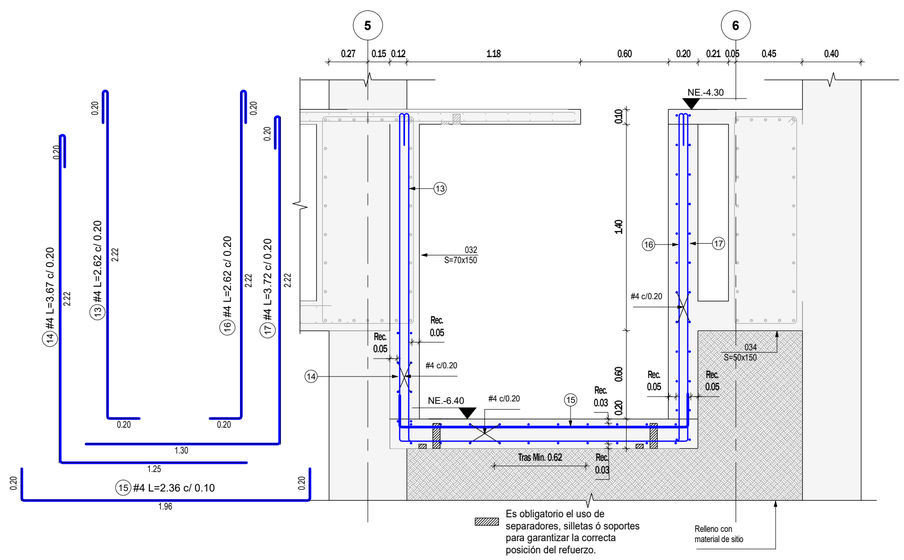

CORTE D-D
Escala 1 : 25

CONCRETO

f'c=35 MPa
f'c=350 kg/cm²
f'c=5000 psi

CONVENCIONES

- Indica pilotes
- Indica muro e=20
- Indica muro e=30
- Indica muro e=50
- Indica viga h=150

NOTAS

1. Ver detalles generales en el PL. 01.02
2. Ver planta de cimentación en el PL. N° 06.00

VERSIÓN : 0

PLANO N° 16.07

Aycardi Estructural

GERENTE DE PROYECTO
LUIS ENRIQUE AYCARDI F.
MAT. 2520212794 CND

INGENIERO
DANIEL E. QUICANO C.

MODELADOR
PAULA ANDREA MONTOYA RENDÓN

MODIFICACIONES	FECHA
Emisión Inicial	21-11-2025

HUMANISE STUDIO

EAN-0519- AES-01-TQ

Calle 71 #9-84

POZOS EYECTORES DE CIMENTACIÓN

EAN-0519 -AES-01-TQ-B2-PL-587 16.07

REVISOR ESTRUCTURAL
JULIO CESAR SANMIGUEL CAMACHO
MAT. 25202-57738 CND

PLANO N° 16.07 VERSIÓN : 0