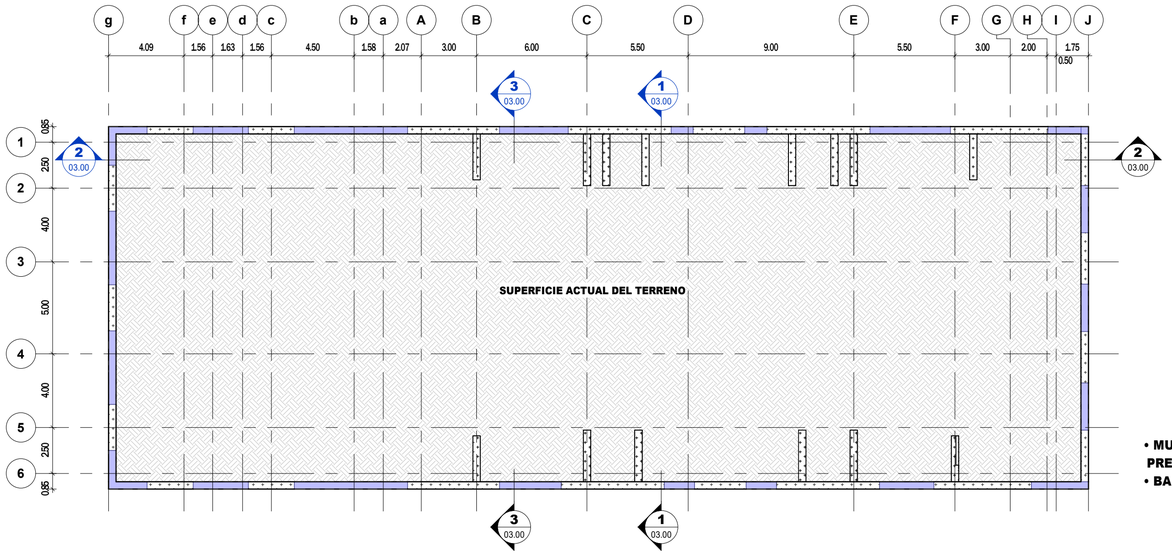

PLANTA PASO 1
Escala 1 : 200

- **MUROS PANTALLA PREEXCAVADA**
- **BARRETES**

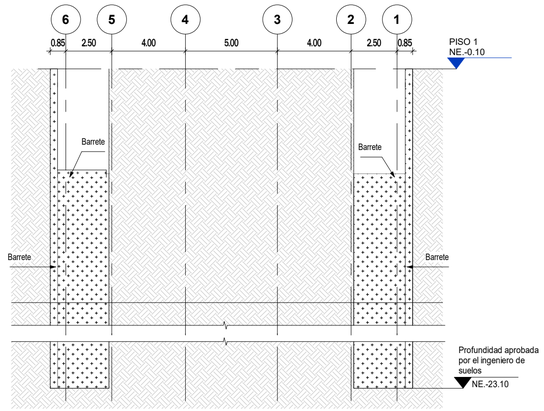

CORTE 1 PASO 1
Escala 1 : 200

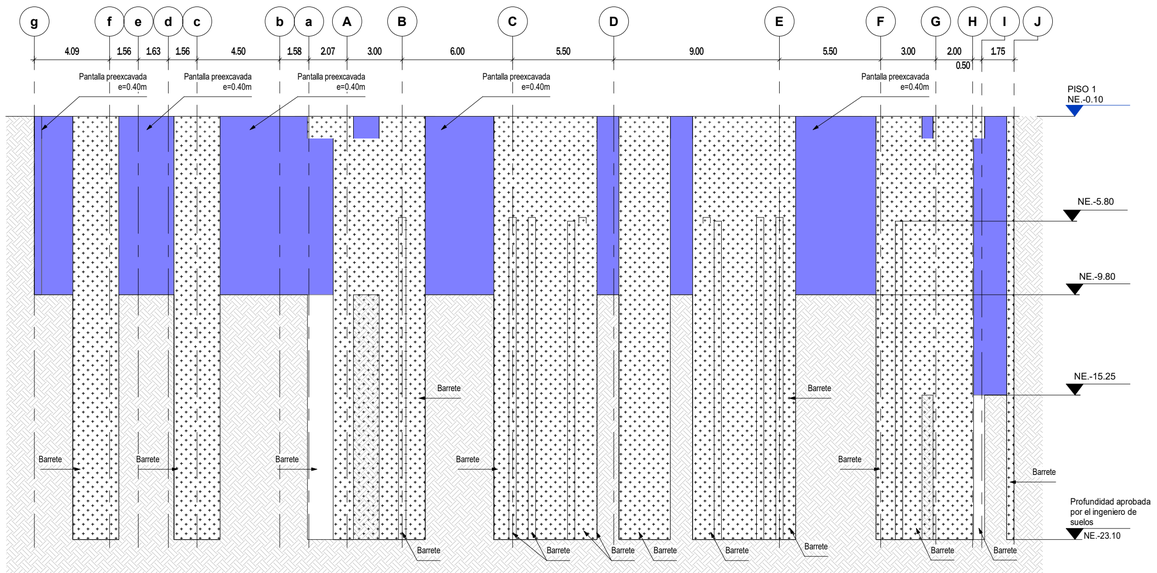

CORTE 2 PASO 1
Escala 1 : 200

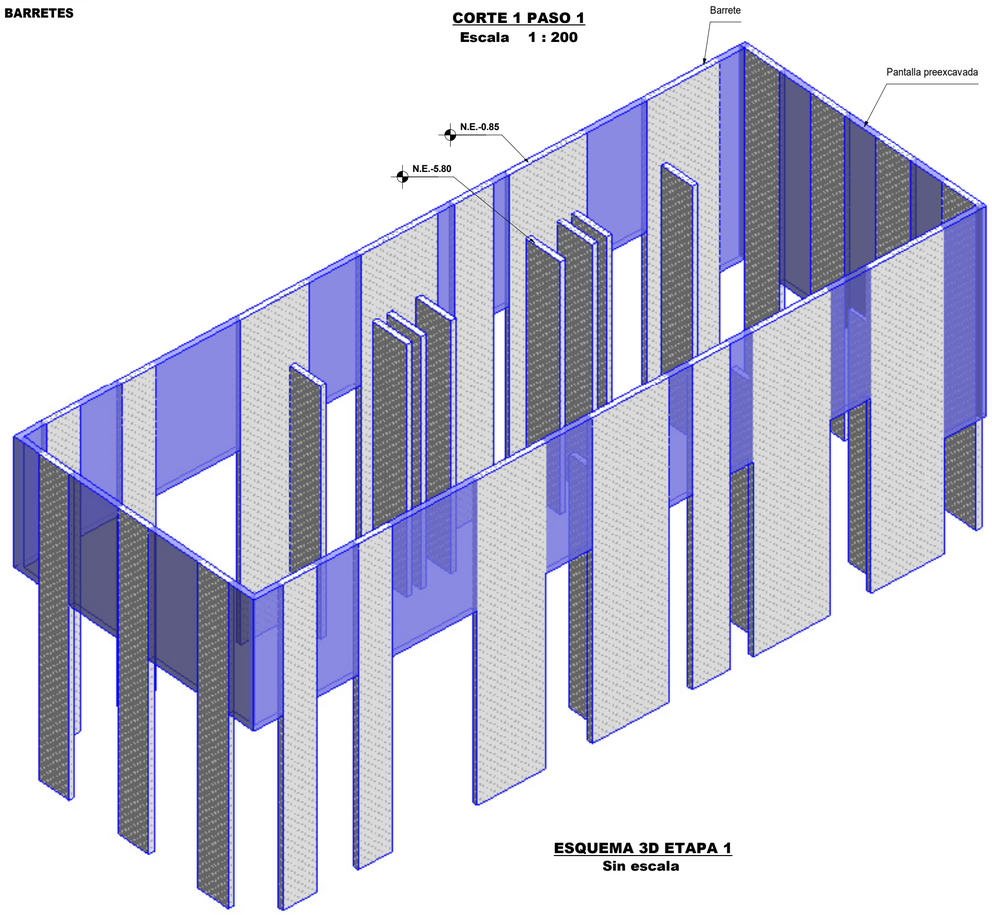

ESQUEMA 3D ETAPA 1
Sin escala

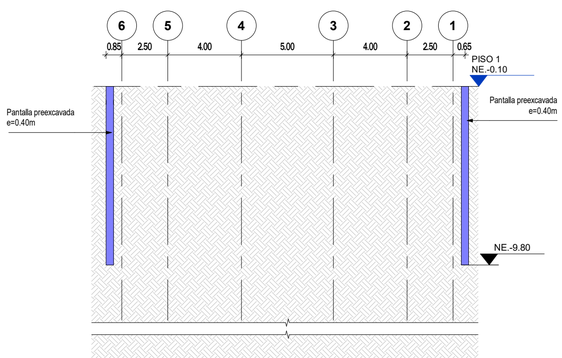

CORTE 3 PASO 1
Escala 1 : 200

CONVENCIONES

- Indica barretes
- Indica pantalla preexcavada

NOTAS

1. Ver planta de localización de pantallas y barretes en PL N° 02.00

VERSIÓN : 0

PLANO N° 03.00

Aycardi Estructural

GERENTE DE PROYECTO
LUIS ENRIQUE AYCARDI F.
MAT. 2520212794 CND

INGENIERO
DANIEL E. QUICANO C.

MODELADOR
PAULA ANDREA MONTOYA RENDÓN

MODIFICACIONES	FECHA
Emisión Inicial	21-11-2025

HUMANISE STUDIO

EAN-0519- AES-01-EST

Calle 71 #9-84

SECUENCIA DE PROCESO CONSTRUCTIVO PASO 1

EAN-0519 -AES-01-EST-CIM-PL-202 03.00

REVISOR ESTRUCTURAL
JULIO CESAR SANMIGUEL CAMACHO
MAT. 25202-57738 CND

PLANO N° 03.00 VERSIÓN : 0