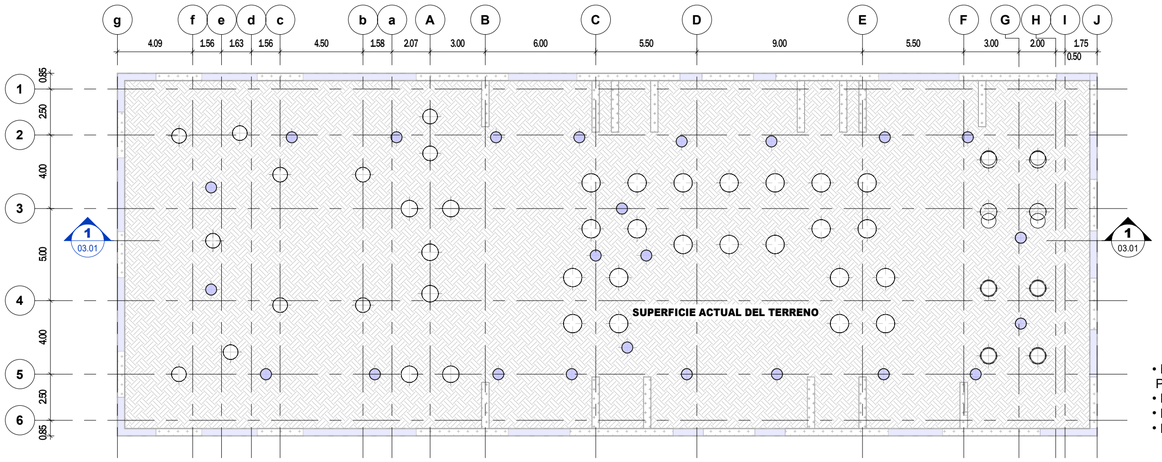

PLANTA PASO 2
Escala 1 : 200

- MUROS PANTALLA PREEXCAVADA
- BARRETES
- **PILOTES CONSTRUCTIVOS**
- **PILOTES DEFINITIVOS**

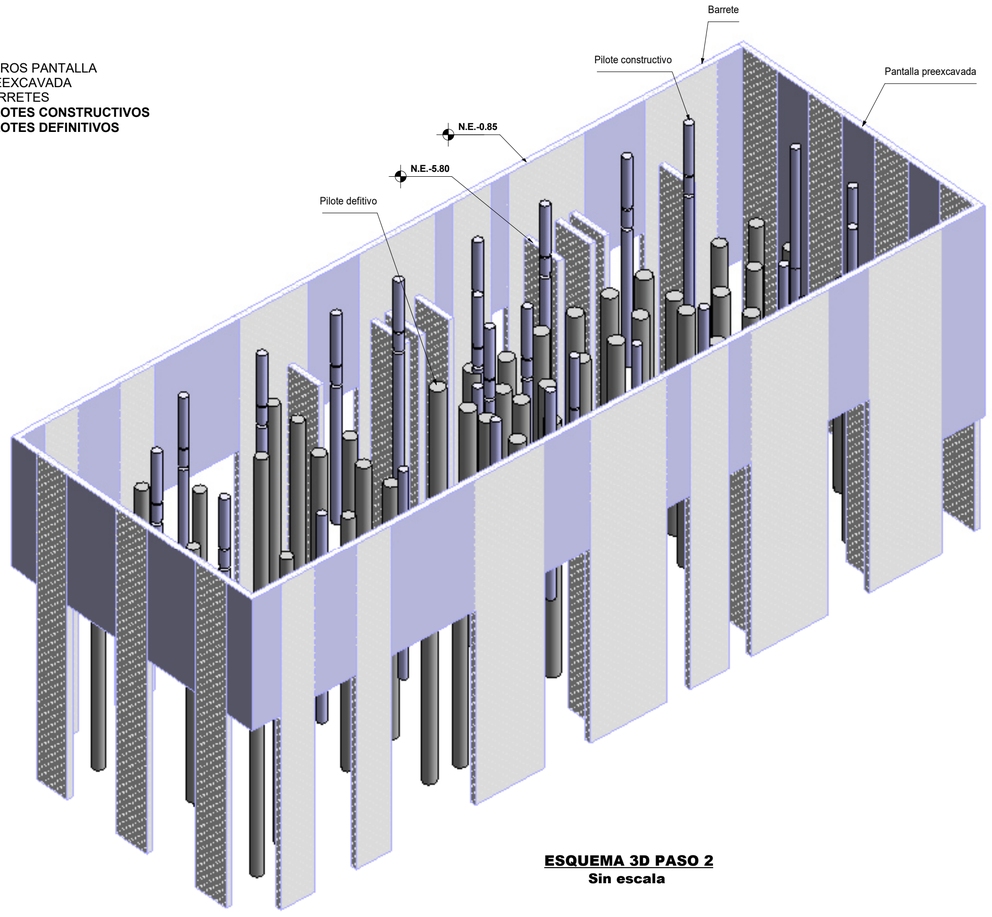

ESQUEMA 3D PASO 2
Sin escala

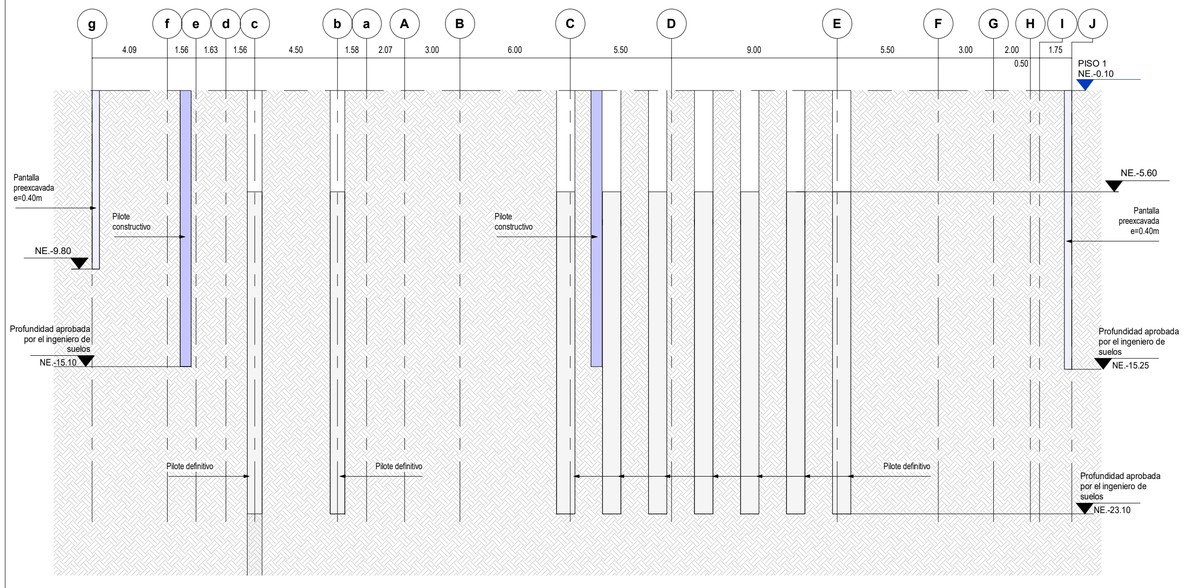

CORTE 1 PASO 2
Escala 1 : 200

CONVENCIONES

- Indica pilotes definitivos
- Indica pilotes constructivos
- Indica barretes
- Indica pantalla preexcavada

NOTAS

1. Ver planta de localización de pilotes, pantallas y barretes en PL N° 02.00

VERSIÓN : 0

PLANO N° 03.01

Aycardi Estructural

GERENTE DE PROYECTO
LUIS ENRIQUE AYCARDI F.
MAT. 2520212794 CND

INGENIERO
DANIEL E. QUICANO C.

MODELADOR
PAULA ANDREA MONTOYA RENDÓN

MODIFICACIONES	FECHA
Emisión Inicial	21-11-2025

HUMANISE STUDIO

EAN-0519- AES-01-EST

Calle 71 #9-84

SECUENCIA PROCESO CONSTRUCTIVO PASO 2

EAN-0519 -AES-01-EST-CIM-PL-203 03.01

REVISOR ESTRUCTURAL
JULIO CESAR SANMIGUEL CAMACHO
MAT. 25202-57738 CND

PLANO N° 03.01 VERSIÓN : 0