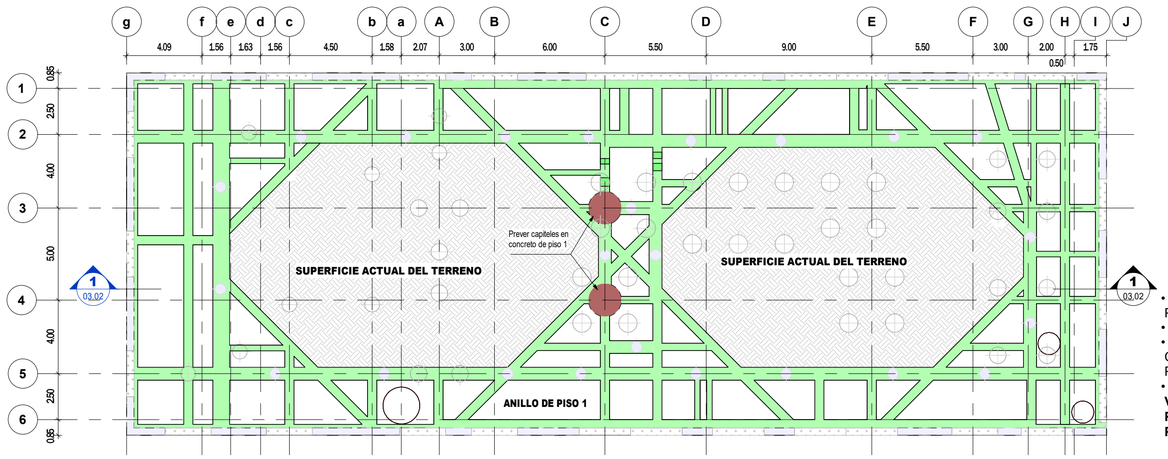

- MUROS PANTALLA PREEXCAVADA
- BARRETES
- PILOTES CONSTRUCTIVOS PILOTES DEFINITIVOS
- **CONSTRUCCIÓN DE VIGAS ANDEN Y VIGAS PUNTAL DEL ANILLO DE PISO 1**

PLANTA PASO 3
Escala 1 : 200

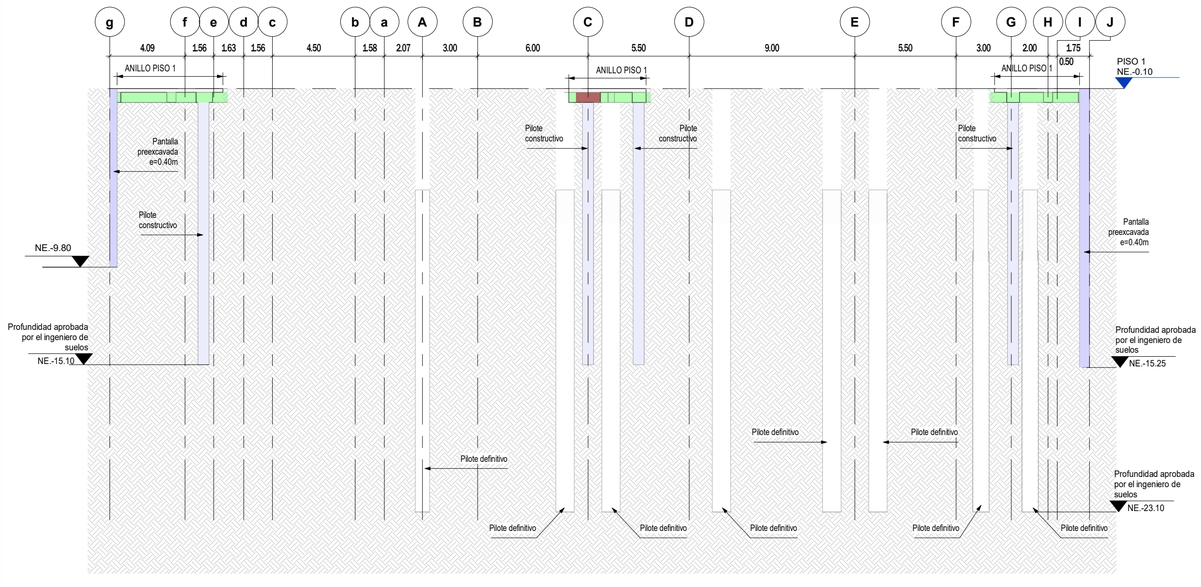

CORTE 1 PASO 3
Escala 1 : 200

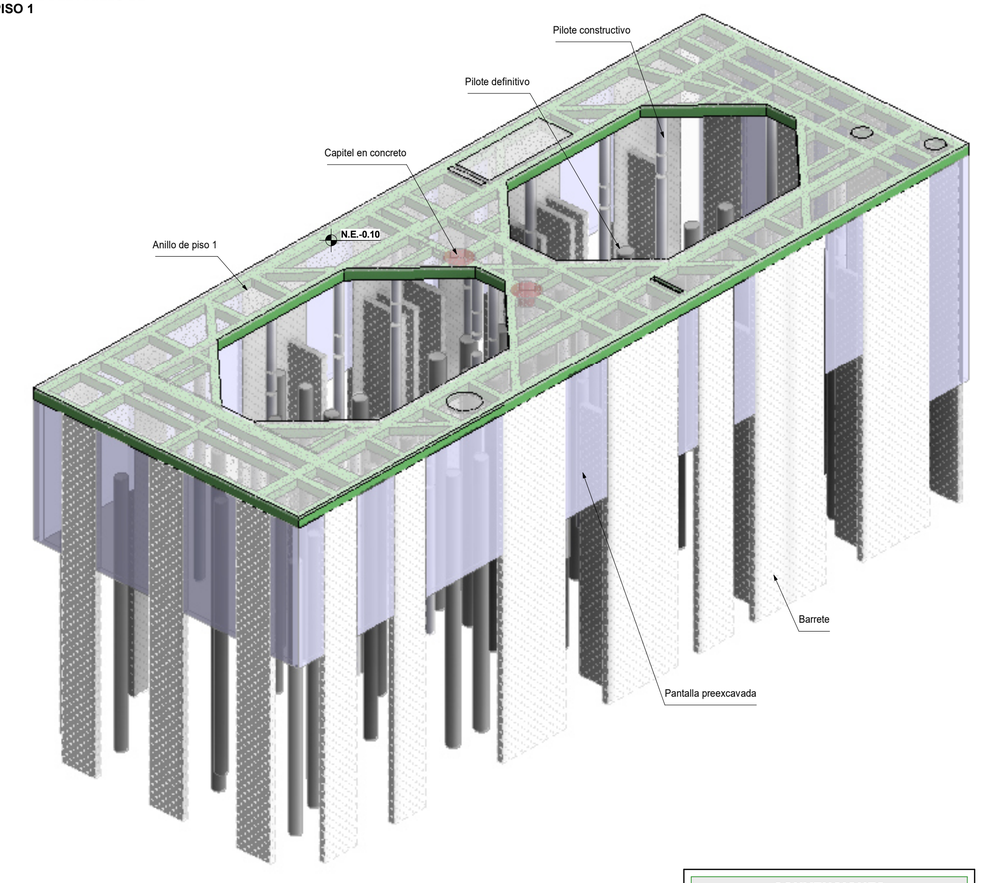

ESQUEMA 3D PASO 3
Sin escala

CONVENCIONES

- Indica pilotes definitivos
- Indica pilotes constructivos
- Indica pantalla preexcavada
- Indica barrete
- Indica viga
- Indica capitel

NOTAS

1. Ver planta de piso 1 etapa 1 (Anillo) en PL N° 07.00

VERSIÓN : 0

PLANO N° 03.02

Aycardi Estructural

GERENTE DE PROYECTO
LUIS ENRIQUE AYCARDI F.
MAT. 2520212794 CND

INGENIERO
DANIEL E. QUICANO C.

MODELADOR
PAULA ANDREA MONTOYA RENDÓN

MODIFICACIONES	FECHA
Emisión Inicial	21-11-2025

HUMANISE STUDIO

EAN-0519- AES-01-EST

Calle 71 #9-84

SECUENCIA PROCESO CONSTRUCTIVO PASO 3

EAN-0519 -AES-01-EST-CIM-PL-204 03.02

REVISOR ESTRUCTURAL
JULIO CESAR SANMIGUEL CAMACHO
MAT. 25202-57738 CND

PLANO N° 03.02 VERSIÓN : 0