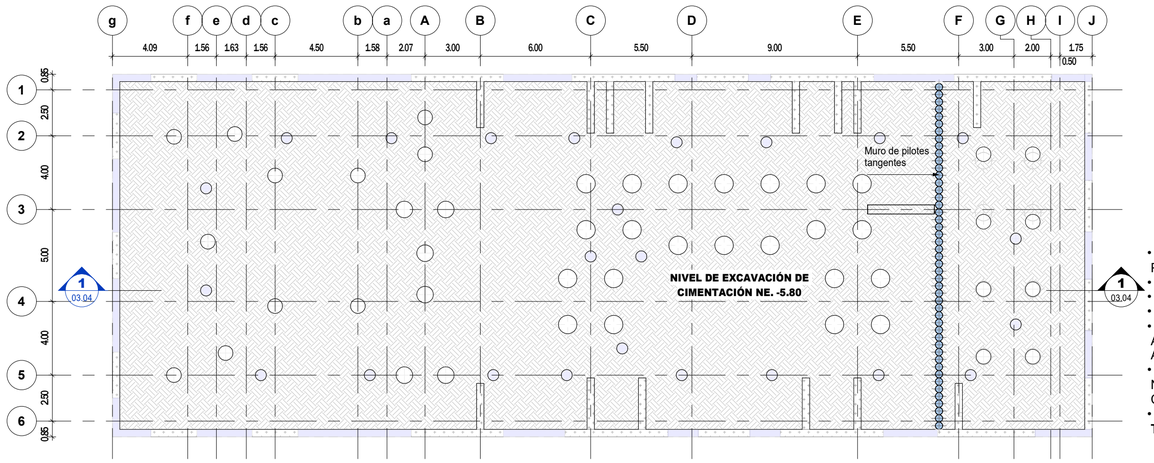

- MUROS PANTALLA PREEXCAVADA
- BARRETES
- PILOTES CONSTRUCTIVOS
- PILOTES DEFINITIVOS
- CONSTRUCCIÓN DE VIGAS ANDEN Y VIGAS PUNTAL ANILLO PISO 1
- EXCAVACIÓN HASTA EL NIVEL INFERIOR DE CIMENTACIÓN
- **CONSTRUCCIÓN PILOTES TANGENTES**

PLANTA PASO 5
Escala 1 : 200

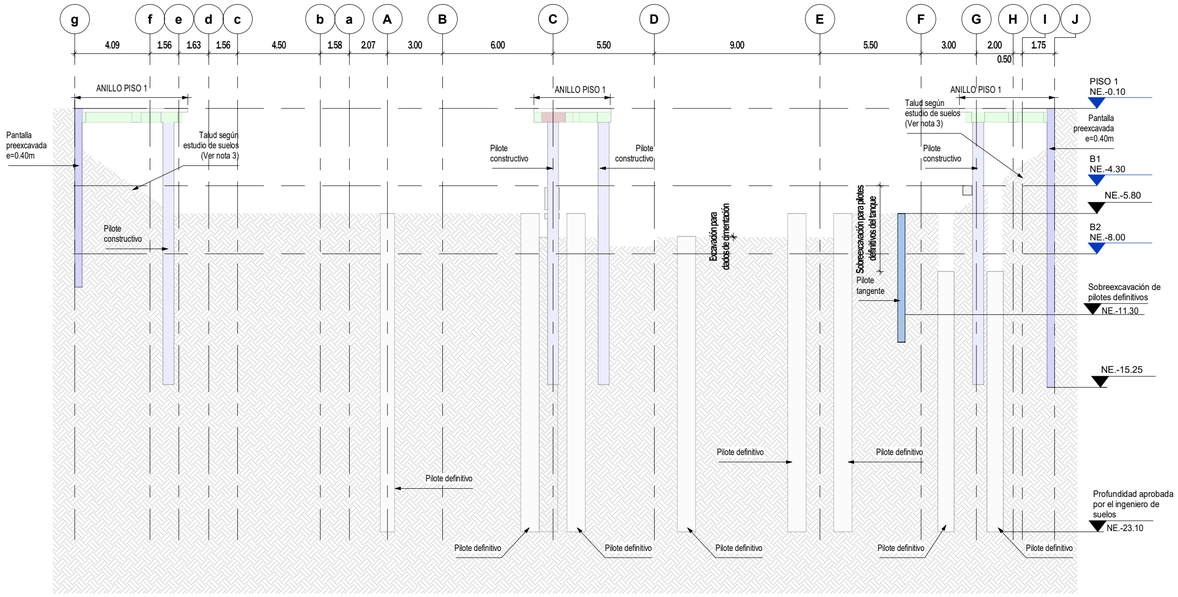

CORTE 1 PASO 5
Escala 1 : 200

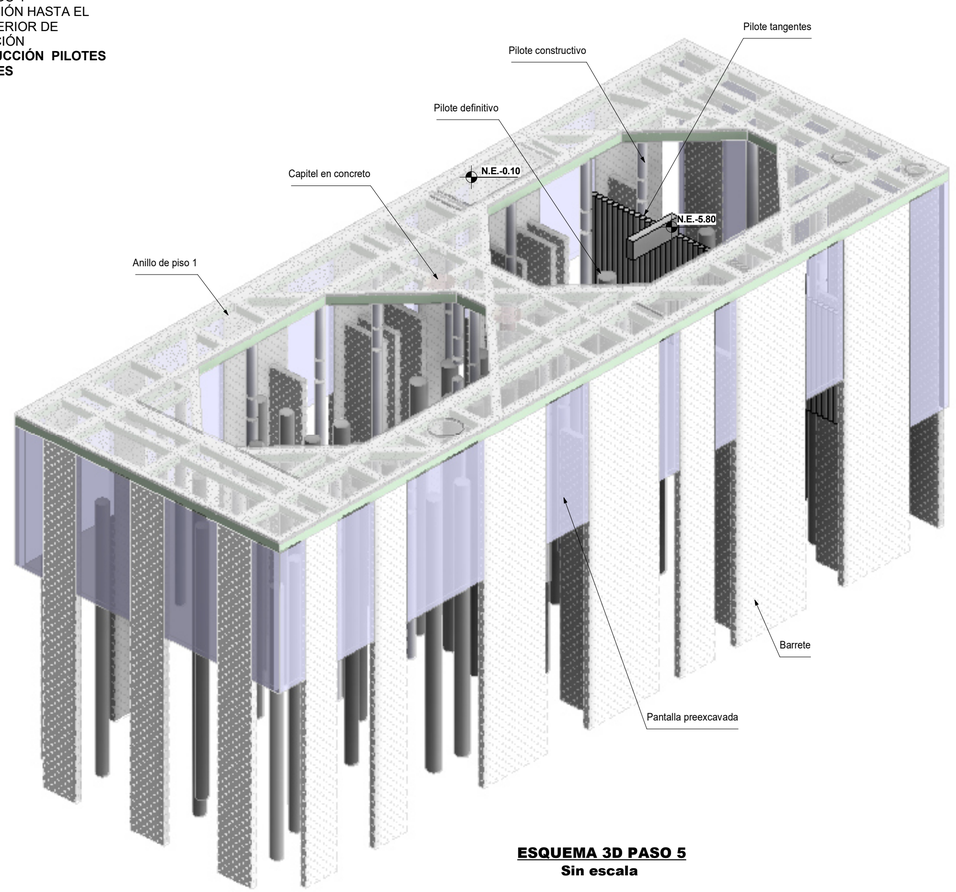

ESQUEMA 3D PASO 5
Sin escala

CONVENCIONES

- Indica pilotes definitivos
- Indica pilotes constructivos
- Indica barretes
- Indica pantalla preexcavada
- Indica pilotes tangentes

NOTAS

1. Ver planta de cimentación en PL N° 06.00
2. Ver planta de localización de pilotes, pantallas y barretes en PL N° 02.00
3. Las áreas de excavacion, franjas, secuencias, alternancias, taludes, niveles entre otros deben ser definidos por el ingeniero de suelos.

VERSIÓN : 0

PLANO N° 03.04

Aycardi Estructural

GERENTE DE PROYECTO
LUIS ENRIQUE AYCARDI F.
MAT. 2520212794 CND

INGENIERO
DANIEL E. QUICANO C.

MODELADOR
PAULA ANDREA MONTOYA RENDÓN

MODIFICACIONES	FECHA
Emisión Inicial	21-11-2025

HUMANISE STUDIO

EAN-0519- AES-01-EST

Calle 71 #9-84

SECUENCIA PROCESO CONSTRUCTIVO PASO 5

EAN-0519 -AES-01-EST-CIM-PL-206 03.04

REVISOR ESTRUCTURAL
JULIO CESAR SANMIGUEL CAMACHO
MAT. 25202-57738 CND

PLANO N° 03.04 VERSIÓN : 0