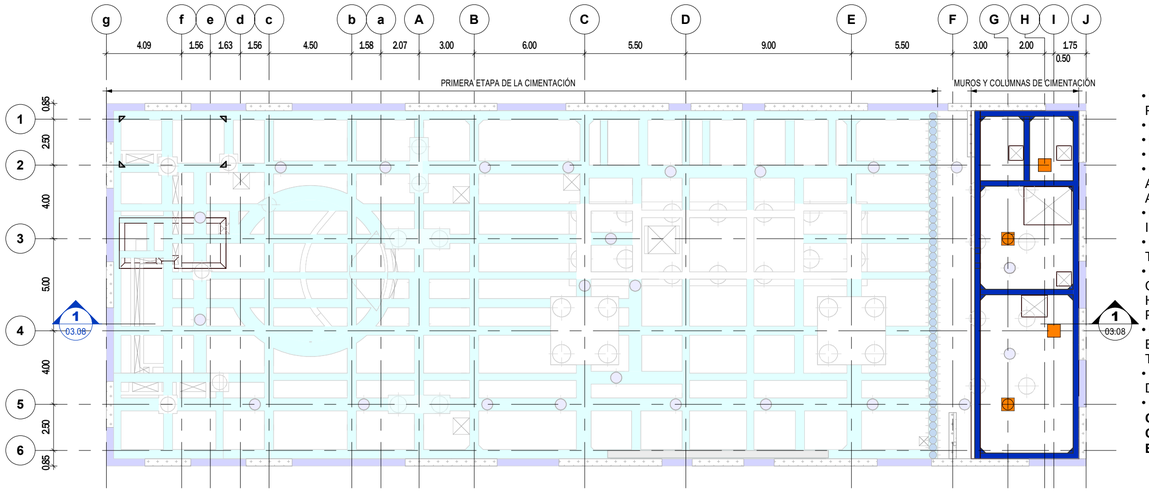

- MUROS PANTALLA PREEXCAVADA
- BARRETES
- PILOTES CONSTRUCTIVOS
- PILOTES DEFINITIVOS
- CONSTRUCCIÓN DE VIGAS ANDEN Y VIGAS PUNTAL ANILLO PISO 1
- EXCAVACIÓN HASTA NIVEL INFERIOR DE CIMENTACIÓN
- CONSTRUCCIÓN PILOTES TANGENTES
- CONSTRUCCIÓN DE CIMENTACIÓN DEL EJE g HASTA EL EJE DE LOS PILOTES TANGENTES
- EXCAVACIÓN PARA TANQUE ENTRE EL EJE DE PILOTES TANGENTES Y EJE J
- APUNTALAMIENTO TEMPORAL DE ZONA DE TANQUE
- **CONSTRUCCIÓN DE CIMENTACIÓN, MUROS, COLUMNAS ZONA DE TANQUE ENTRE NIVELES B2 Y B1**

PLANTA PASO 9
Escala 1 : 200

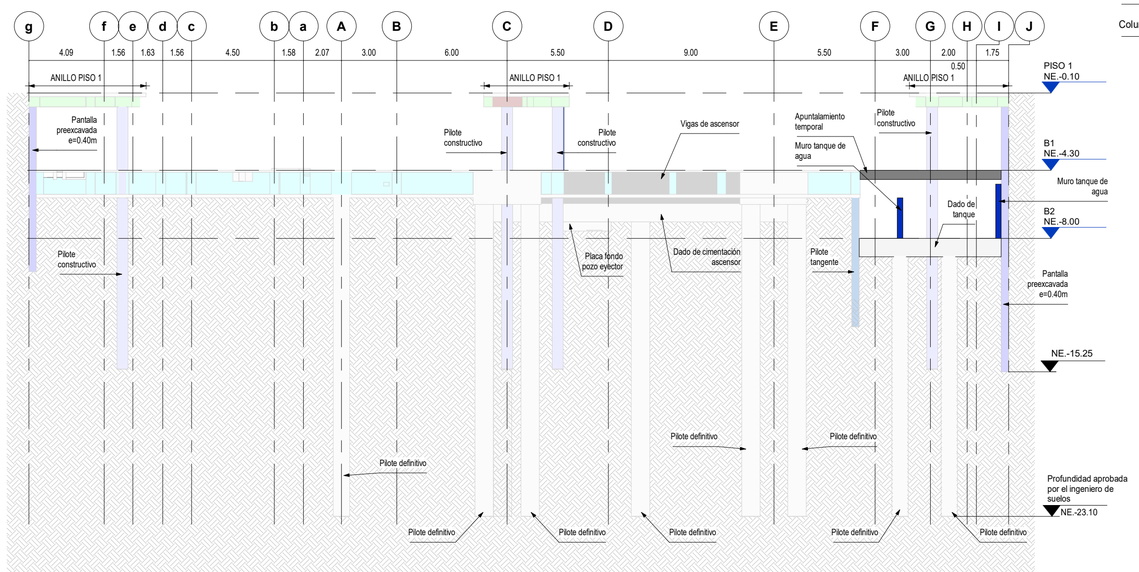

CORTE 1 PASO 9
Escala 1 : 200

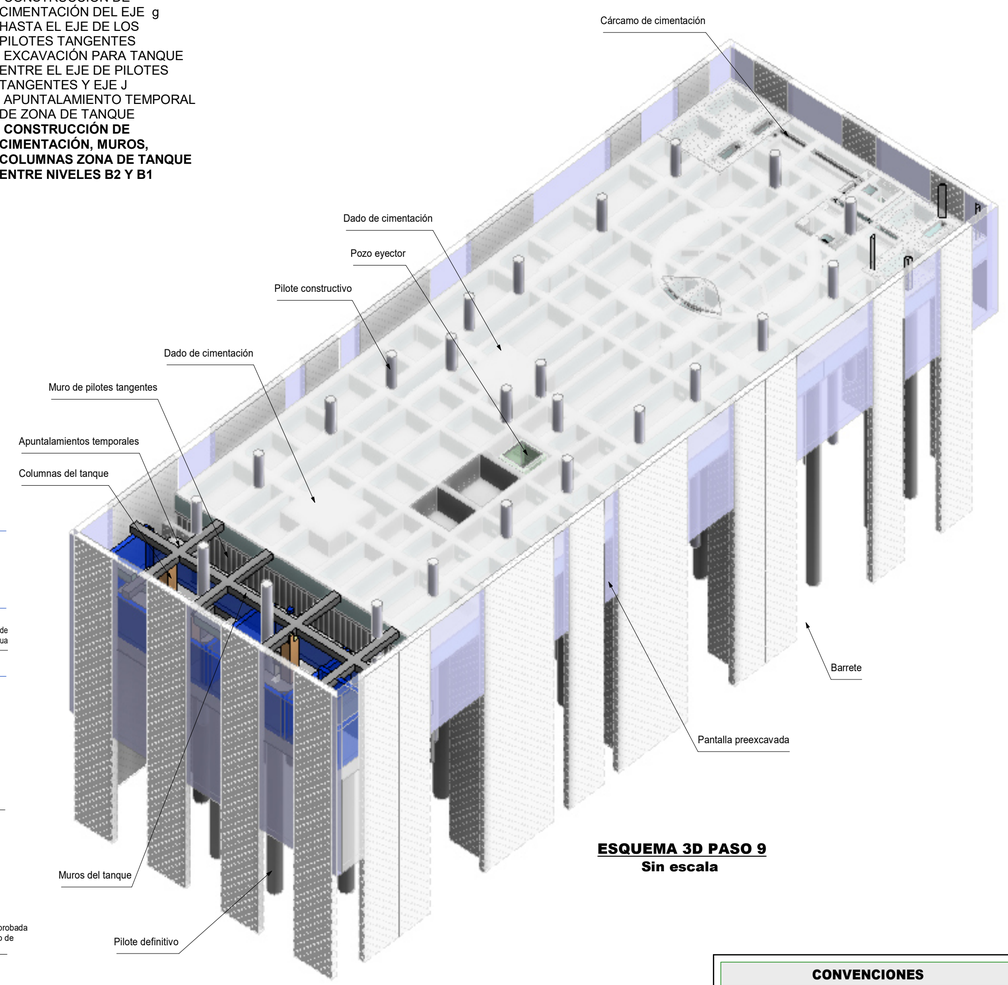

ESQUEMA 3D PASO 9
Sin escala

CONVENCIONES

- Indica pilotes definitivos
- Indica pilotes constructivos
- Indica pilotes tangentes
- Indica barretes
- Indica pantalla preexcavada
- Indica vigas cimentación
- Indica vigas aéreas
- Indica columnas
- Indica muros tanque
- Indica apuntalamiento temporal

NOTAS

1. Ver planta de cimentación en PL N° 06.00 y planta de localización de pilotes, pantallas y barretes en PL N° 02.00
2. Ver planta de cimentación del tanque de agua en el PL N° 16.00
3. Ver despiece de tanque de agua en el PL N° 16.00 y 16.01
4. Ver planta de localización de muros y columnas en el PL N° 04.00

VERSIÓN : 0

PLANO N° 03.08

Aycardi Estructural

GERENTE DE PROYECTO
LUIS ENRIQUE AYCARDI F.
MAT. 2520212794 CND

INGENIERO
DANIEL E. QUICANO C.

MODELADOR
PAULA ANDREA MONTOYA RENDÓN

MODIFICACIONES	FECHA
Emisión Inicial	21-11-2025

HUMANISE STUDIO

EAN-0519- AES-01-EST

Calle 71 #9-84

SECUENCIA PROCESO CONSTRUCTIVO PASO 9

EAN-0519 -AES-01-EST-CIM-PL-210 03.08

REVISOR ESTRUCTURAL
JULIO CESAR SANMIGUEL CAMACHO
MAT. 25202-57738 CND

PLANO N° 03.08 VERSIÓN : 0