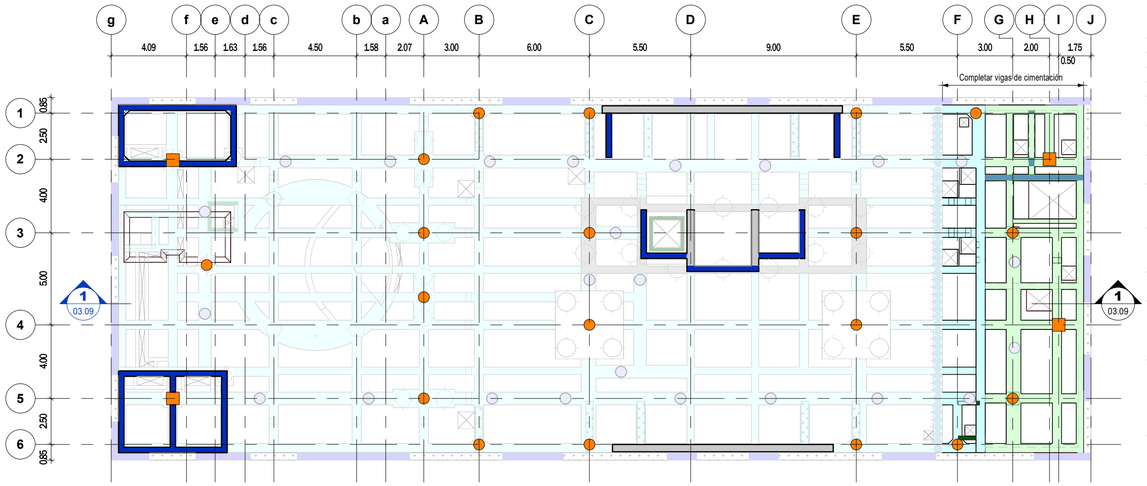

PLANTA PASO 10
Escala 1 : 200

- MUROS PANTALLA PREEXCAVADA
- BARRETES
- PILOTES CONSTRUCTIVOS
- PILOTES DEFINITIVOS
- CONSTRUCCIÓN DE VIGAS ANDEN Y VIGAS PUNTAL ANILLO PISO 1
- EXCAVACIÓN HASTA NIVEL INFERIOR DE CIMENTACIÓN
- CONSTRUCCIÓN PILOTES TANGENTES
- CONSTRUCCIÓN DE CIMENTACIÓN DEL EJE g HASTA EL EJE DE LOS PILOTES TANGENTES
- EXCAVACIÓN PARA TANQUE ENTRE EL EJE DE PILOTES TANGENTES Y EJE J
- APUNTALAMIENTO TEMPORAL DE ZONA DE TANQUE
- CONSTRUCCIÓN DE CIMENTACIÓN, MUROS, COLUMNAS ZONA DE TANQUE ENTRE NIVELES B2 Y B1
- **DESMONTE DE APUNTALAMIENTOS TEMPORALES DE CIMENTACIÓN Y CONSTRUCCIÓN DE CIMENTACIÓN ENTRE EJES F Y J**
- **CONSTRUCCIÓN DE MUROS Y COLUMNAS DE B1 A PISO 1**

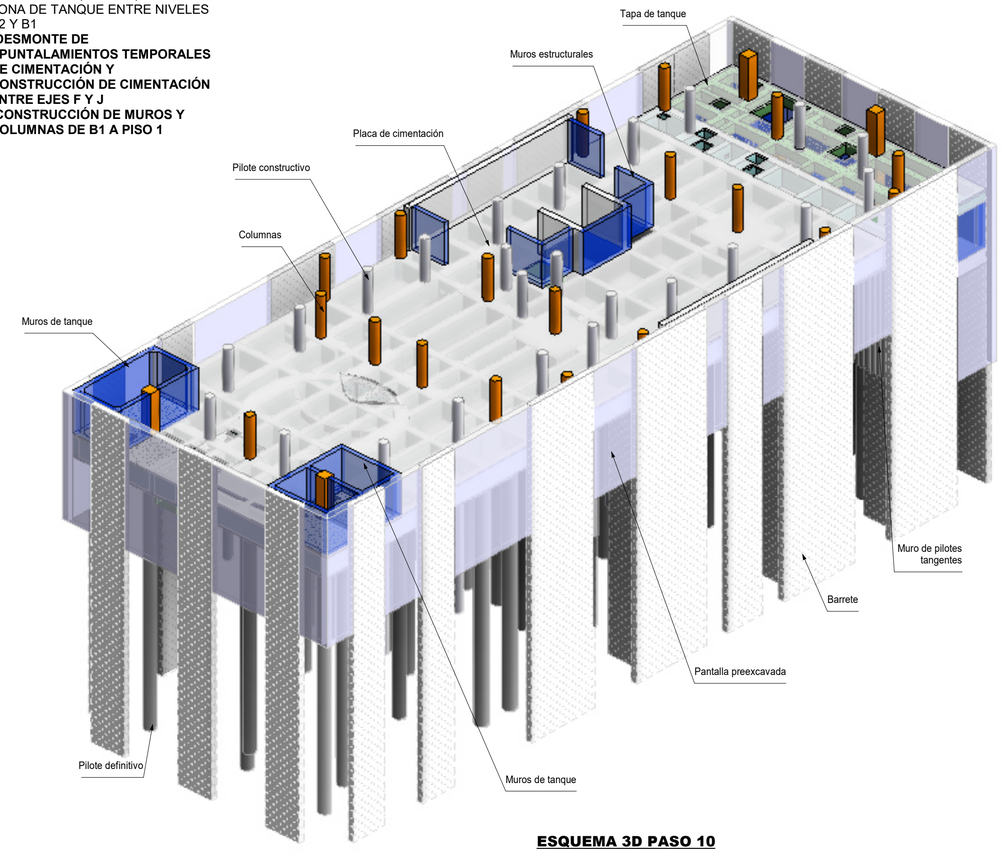

ESQUEMA 3D PASO 10
Sin escala

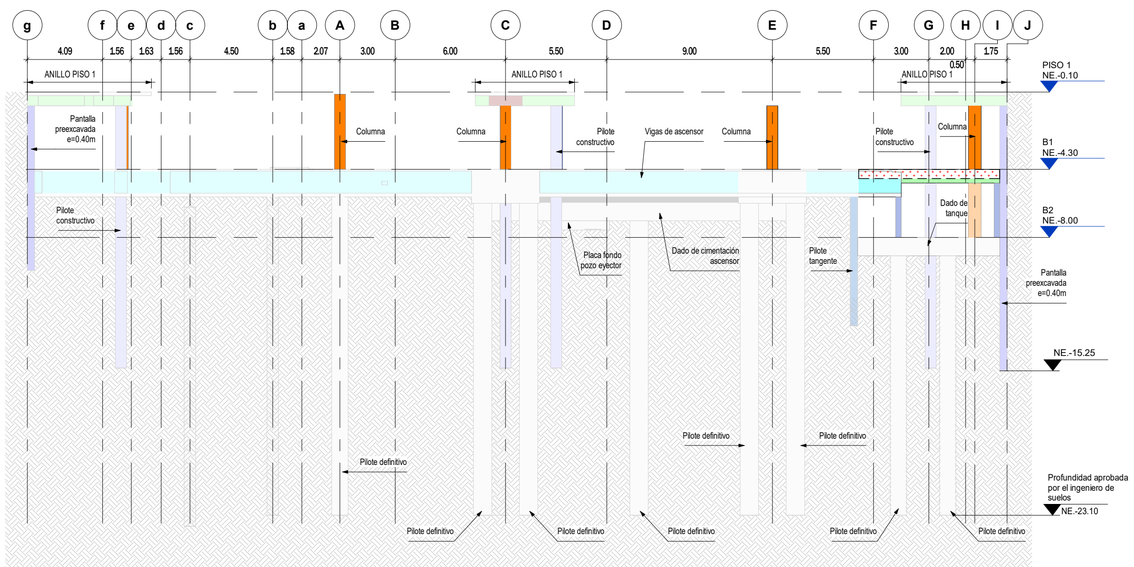

CORTE 1 PASO 10
Escala 1 : 200

CONVENCIONES

- Indica pilotes
- Indica pilotes constructivos
- Indica pilotes tangentes
- Indica barretes
- Indica pantalla preexcavada
- Indica vigas cimentación
- Indica columnas
- Indica muros de tanques y muros de la torre
- Indica vigas de cimentación sobre tanque
- Indica muros de la torre

NOTAS

1. Ver planta de cimentación en PL N° 06.00
2. Ver planta de localización de pilotes, pantallas y barretes en PL N° 02.00
3. Ver planta de localización de muros y columnas en el PL N° 04.00

VERSIÓN : 0

PLANO N° 03.09

Aycardi Estructural

GERENTE DE PROYECTO
LUIS ENRIQUE AYCARDI F.
MAT. 2520212794 CND

INGENIERO
DANIEL E. QUICANO C.

MODELADOR
PAULA ANDREA MONTOYA RENDÓN

MODIFICACIONES	FECHA
Emisión Inicial	21-11-2025

HUMANISE STUDIO

EAN-0519- AES-01-EST

Calle 71 #9-84

SECUENCIA PROCESO CONSTRUCTIVO PASO 10

EAN-0519 -AES-01-EST-CIM-PL-211 03.09

REVISOR ESTRUCTURAL
JULIO CESAR SANMIGUEL CAMACHO
MAT. 25202-57738 CND

PLANO N° 03.09 VERSIÓN : 0