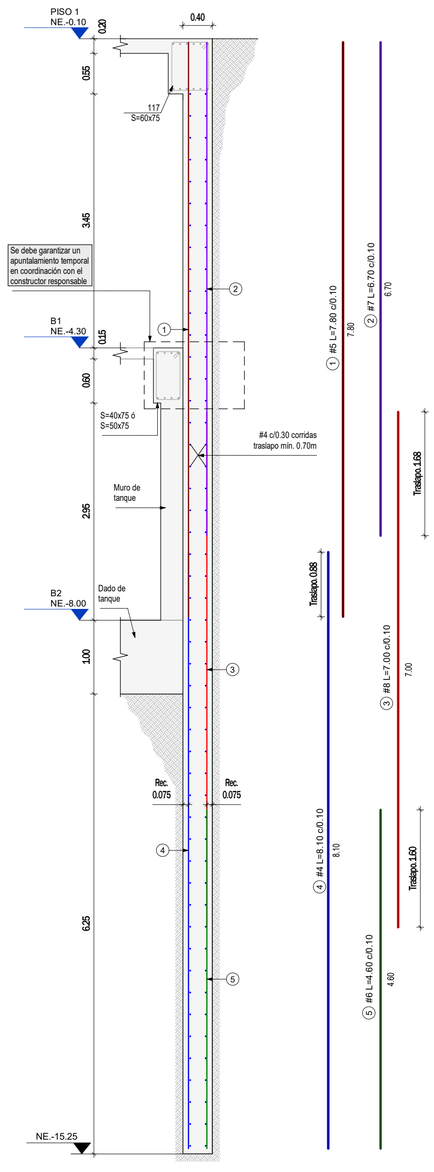

NOTA: Usar distanciadores para garantizar la correcta posición del refuerzo

DESPIECE DE PANTALLA TIPO 1

Escala 1 : 50

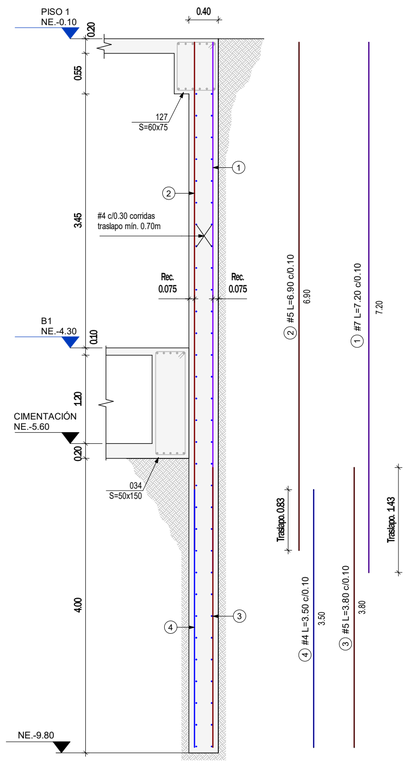

NOTA: Usar distanciadores para garantizarla correcta posición del refuerzo

DESPIECE DE PANTALLA TIPO 2

Escala 1 : 50

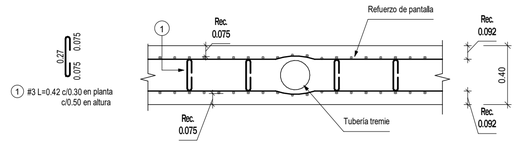

DETALLE DE TUBERÍA TREMIE PARA PANTALLA

Escala 1 : 25

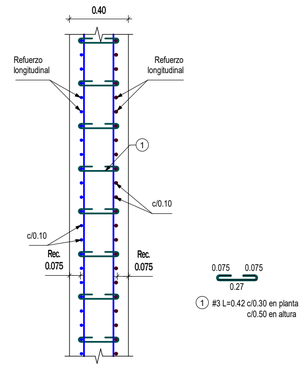

SECCIÓN PANTALLA PRE-EXCAVADA

Escala 1 : 25

CONCRETO

f'c=28 MPa
f'c=280 kg/cm²
f'c=4000 psi

NOTAS

1. Ver detalles generales en PL N° 01.02 y 01.03
2. Ver planta de localización de pilotes, pantallas y barretes en PL N° 02.00
3. Se ha diseñado las pantallas y los barretes para una sobrecarga q=2.0 ton/m²

NOTA:
Este plano debe ser revisado y aprobado por el Ingeniero de suelos.

VºBº INGENIERO DE SUELOS

VERSIÓN : 0

PLANO N° 02.01

Aycardi Estructural

GERENTE DE PROYECTO
LUIS ENRIQUE AYCARDI F.
MAT. 2520212794 CND

INGENIERO
DANIEL E. QUICANO C.

MODELADOR
PAULA ANDREA MONTOYA RENDÓN

MODIFICACIONES	FECHA
Emisión Inicial	21-11-2025

HUMANISE STUDIO

EAN-0519- AES-01-EST

Calle 71 #9-84

DESPIECE DE PANTALLAS

EAN-0519 -AES-01-EST-CIM-PL-503 02.01

REVISOR ESTRUCTURAL
JULIO CESAR SANMIGUEL CAMACHO
MAT. 25202-57738 CND

PLANO N° 02.01 VERSIÓN : 0