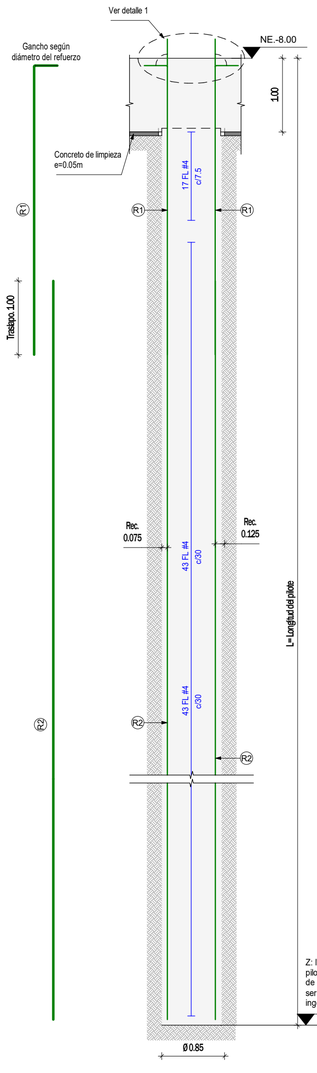

DESPIECE PILOTE TIPO 1
Escala 1 : 50

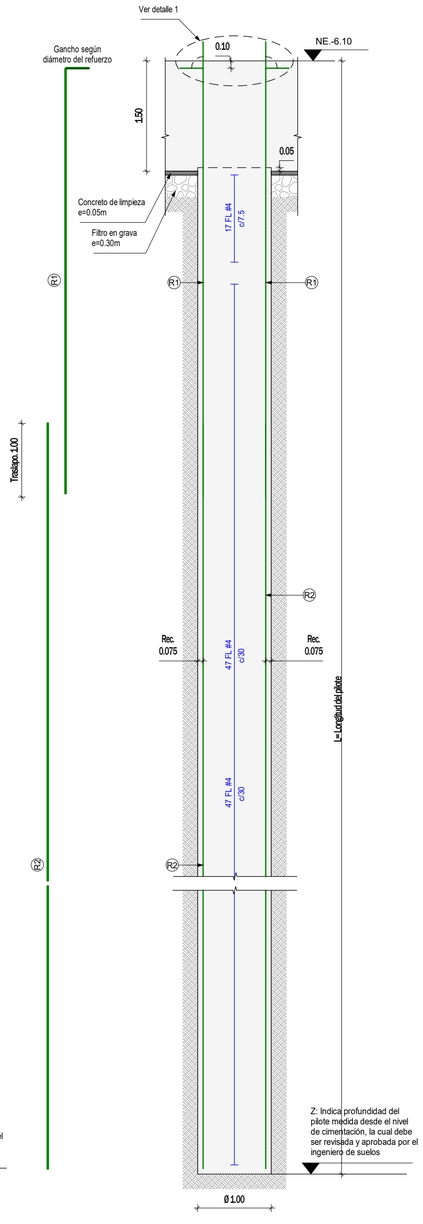

DESPIECE PILOTE TIPO 2
Escala 1 : 50

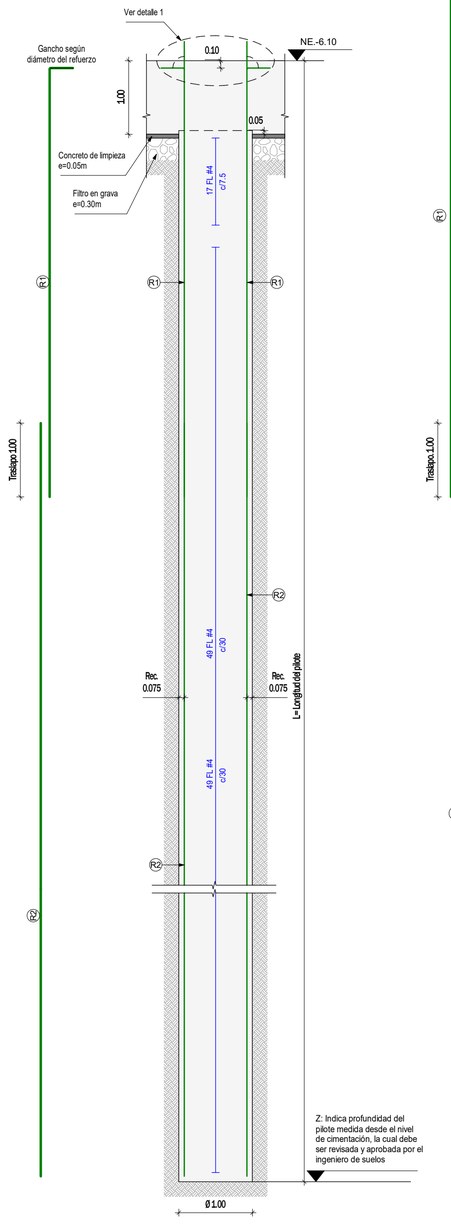

DESPIECE PILOTE TIPO 3
Escala 1 : 50

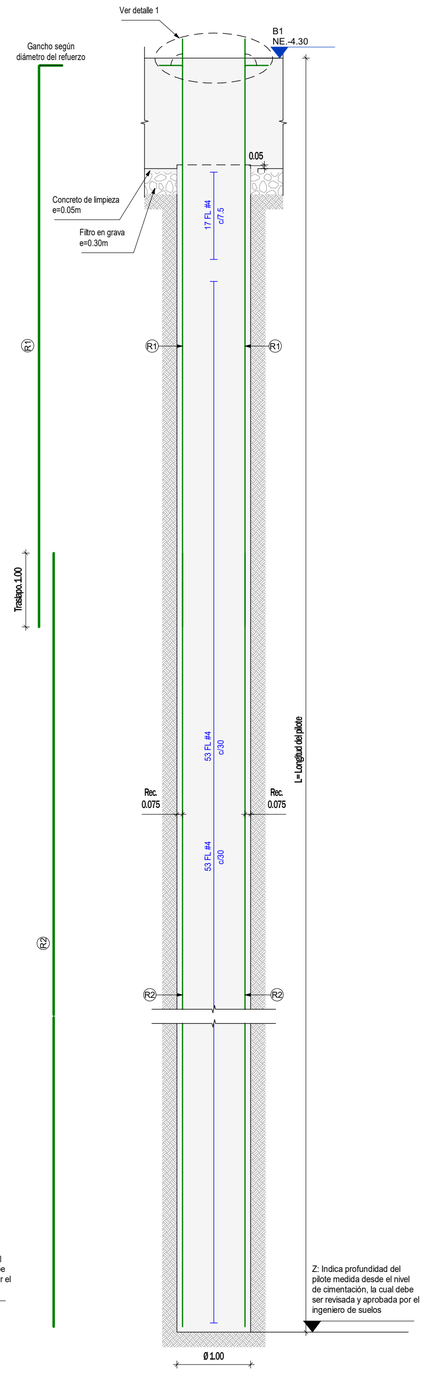

DESPIECE PILOTES TIPO 4, 5 y 6
Escala 1 : 50

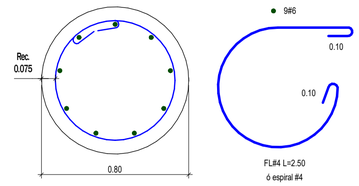

SECCIÓN PILOTE Ø0.80
Escala 1 : 20

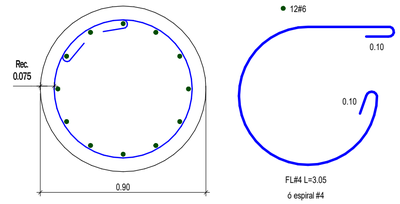

SECCIÓN PILOTE Ø0.90
Escala 1 : 20

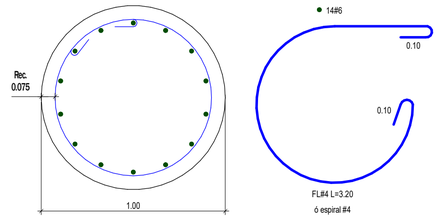

SECCIÓN PILOTE Ø1.00
Escala 1 : 20

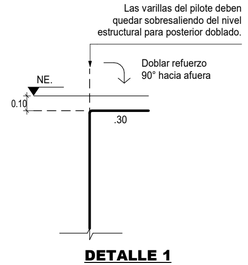

DETALLE 1
Escala 1 : 25

CUADRO RESUMEN DE REFUERZO DE PILOTES																			
Tipo Pilote		UNID	Refuerzo Longitudinal							Refuerzo Transversal								RESUMEN		
			Z [m]	L (m)	Cant	Barra	R1 (m)	R2 (m)	R3 (m)	Tramo F1				Tramo F2				V_C (m^3)	W_{RL} (kg)	W_{RT} (kg)
1	Ø 0.8 m	8	23.0	15.00	9	# 6	4.3	12.00	0.00	17	# 4	c/ 0.075	L= 2.50 m	43	# 4	c/ 0.30	L= 2.50 m	60.3	2641	1200
2	Ø 1.0 m	2	23.0	16.90	14	# 6	6.1	12.00	0.00	17	# 4	c/ 0.075	L= 3.20 m	47	# 4	c/ 0.30	L= 3.20 m	26.5	1140	410
3	Ø 1.0 m	12	23.0	16.90	14	# 6	6.1	12.00	0.00	17	# 4	c/ 0.075	L= 3.20 m	49	# 4	c/ 0.30	L= 3.20 m	159.3	6842	2534
4	Ø 0.8 m	11	23.0	18.70	9	# 6	7.9	12.00	0.00	17	# 4	c/ 0.075	L= 2.50 m	53	# 4	c/ 0.30	L= 2.50 m	103.4	4433	1925
5	Ø 0.9 m	6	23.0	18.70	12	# 6	7.9	12.00	0.00	17	# 4	c/ 0.075	L= 3.05 m	53	# 4	c/ 0.30	L= 3.05 m	71.4	3224	1281
6	Ø 0.9 m	8	23.0	18.70	12	# 6	7.9	12.00	0.00	17	# 4	c/ 0.075	L= 3.05 m	53	# 4	c/ 0.30	L= 3.05 m	95.2	4298	1708
	Total	*47*																***516.1***	***22578***	***9058***

V_C: Volúmen de concreto pilotes Se calcula con la longitud "L" que se indica en el corte típico.
W_{RL}: Peso Refuerzo Longitudinal
W_{RT}: Peso Refuerzo Transversal
NOTA: Éstas cantidades no incluyen desperdicios

CONCRETO

f'c=28 MPa
f'c=280 kg/cm²
f'c=4000 psi

NOTAS

1. Ver detalles generales en PL N° 01.02 y 01.03
2. Ver planta de localización de pilotes, pantallas y barretes en PL N° 02.00

NOTA:
La longitud ó profundidad del pilote deberá ser revisada y aprobada en obra por el Ingeniero de Suelos para garantizar que la capacidad del elemento sea la establecida en el estudio de suelos.

VºBº INGENIERO DE SUELOS

VERSIÓN : 0

PLANO N° 02.02

Aycardi Estructural

GERENTE DE PROYECTO
LUIS ENRIQUE AYCARDI F.
MAT. 2520212794 CND

INGENIERO
DANIEL E. QUICANO C.

MODELADOR
PAULA ANDREA MONTOYA RENDÓN

MODIFICACIONES	FECHA
Emisión Inicial	21-11-2025

HUMANISE STUDIO

EAN-0519- AES-01-EST

Calle 71 #9-84

DESPIECE DE PILOTES

EAN-0519 -AES-01-EST-CIM-PL-504 02.02

REVISOR ESTRUCTURAL
JULIO CESAR SANMIGUEL CAMACHO
MAT. 25202-57738 CND

PLANO N° 02.02 VERSIÓN : 0