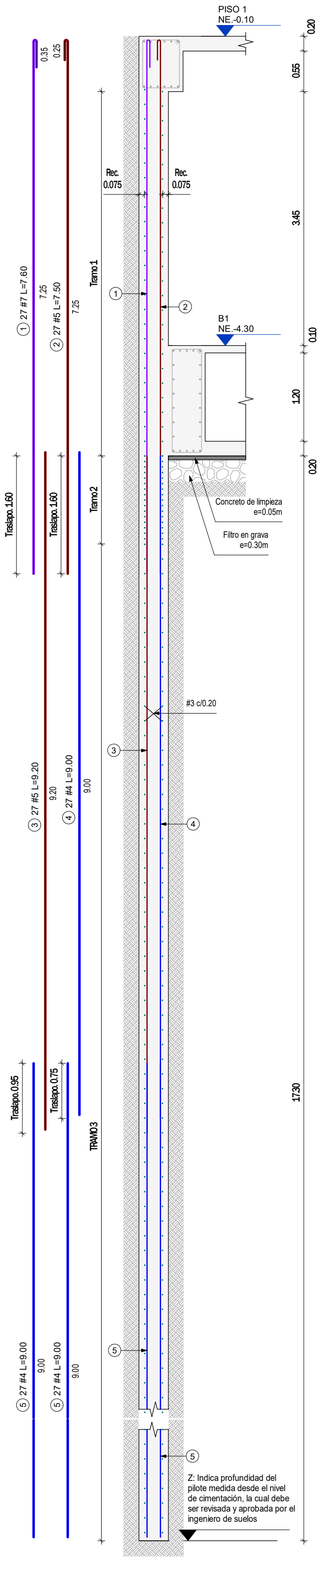

DESPIECE BARRETES TIPO 1
Escala 1 : 50

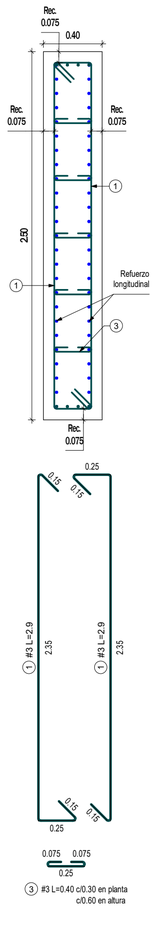

SECCIÓN BARRETE TIPO 1 S=40x250
Escala 1 : 25

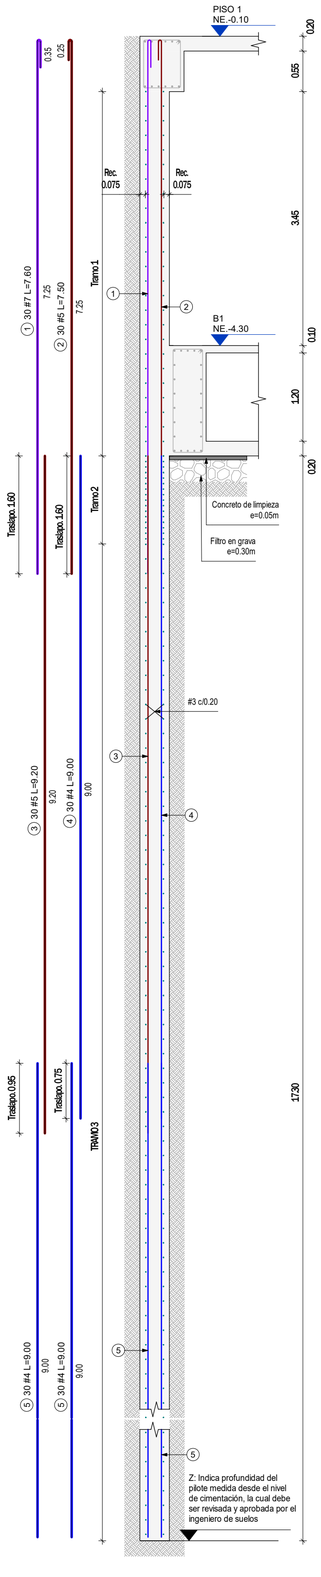

DESPIECE BARRETES TIPO 2
Escala 1 : 50

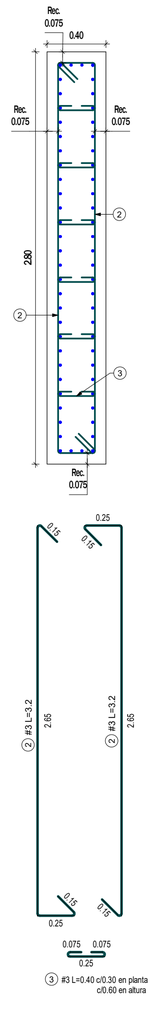

SECCIÓN BARRETE TIPO 2 S=40x280
Escala 1 : 25

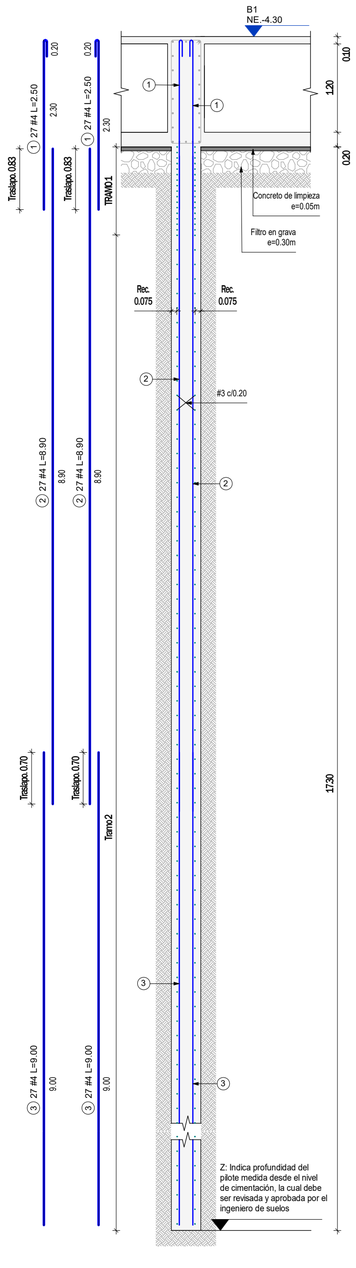

DESPIECE BARRETES TIPO 3
Escala 1 : 50

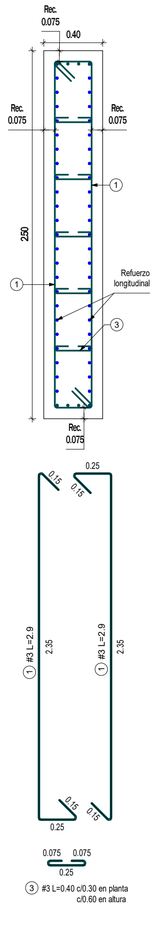

SECCIÓN BARRETE TIPO 3 S=40x250
Escala 1 : 25

NOTA:
La longitud ó profundidad del pilote deberá ser revisada y aprobada en obra por el Ingeniero de Suelos para garantizar que la capacidad del elemento sea la establecida en el estudio de suelos.

VºBº INGENIERO DE SUELOS

NOTAS

1. Ver detalles generales en PL N° 01.02 y 01.03
2. Ver planta de localización de pilotes, pantallas y barretes en PL N° 02.00
3. Se ha diseñado las pantallas y los barretes para una sobrecarga q=2.0 ton/m²

CONCRETO

f'c=28 MPa
f'c=280 kg/cm²
f'c=4000 psi

VERSIÓN : 0

PLANO Nº 02.04

Aycardi Estructural

GERENTE DE PROYECTO
LUIS ENRIQUE AYCARDI F.
MAT. 2520212794 CND

INGENIERO
DANIEL E. QUICANO C.

MODELADOR
PAULA ANDREA MONTOYA RENDÓN

MODIFICACIONES	FECHA
Emisión Inicial	21-11-2025

HUMANISE STUDIO

EAN-0519- AES-01-EST

Calle 71 #9-84

DESPIECE DE BARRETES

EAN-0519 -AES-01-EST-CIM-PL-506 02.04

REVISOR ESTRUCTURAL
JULIO CESAR SANMIGUEL CAMACHO
MAT. 25202-57738 CND

PLANO Nº 02.04 VERSIÓN : 0