Tipo	Sección a (m)	Sección h (m)	UNID	Refuerzo Longitudinal columna Sección 1 Z [m]	L [m]	Cant	Barra	R1	Cant	Barra	R2	Cant	Barra	R3	Cant	Barra	R4	Refuerzo Longitudinal pilote Sección 2 Cant	Barra	R5	Cant	Barra	R6
Tipo 1	0.4 m	2.5 m	13	23.0	23.0	37	#7	7.6	37	#5	7.5	37	#5	9.2	37	#4	9	54	#4	9			
Tipo 2	0.4 m	2.8 m	10	23.0	23.0	30	#7	7.6	30	#5	7.5	30	#5	9.2	30	#4	9	60	#4	9			
Tipo 3	0.4 m	2.5 m	4	23.0	18.6	54	#4	2.8	54	#4	8.9	54	#4	9									
Tipo 4	0.4 m	2.8 m	10	23.0	18.6	60	#4	2.8	60	#4	8.9	60	#4	9									
Tipo 5	0.4 m	2.8 m	6	23.0	23.0	30	#7	7.45	30	#5	8.05	30	#8	8.9	30	#4	8.9	30	#6	9	30	#4	9
			43																				

Tipo	Tramo 1 Refuerzo Principal				Tramo 1 Refuerzo Suplementario				Tramo 2 Refuerzo Principal				Tramo 2 Refuerzo Suplementario				Tramo 3 Refuerzo Principal				Tramo 3 Refuerzo Suplementario				RESUMEN V_C (m³)	W_{RL} (kg)	W_{RT} (kg)
Tipo 1	52	#3	c/ 0.200	L= 2.90 m	45	# 3	c/ 0.600	L= 0.40 m	34	# 3	c/ 0.075	L= 2.90 m	85	# 3	c/ 0.075	L= 0.40 m	164	# 3	c/ 0.200	L= 2.90 m	140	# 3	c/ 0.200	L= 0.40 m	299.0	26784	6064
Tipo 2	52	# 3	c/ 0.200	L= 3.20 m	54	# 3	c/ 0.200	L= 0.40 m	34	# 3	c/ 0.075	L= 3.20 m	102	# 3	c/ 0.075	L= 0.40 m	164	# 3	c/ 0.200	L= 3.20 m	168	# 3	c/ 0.200	L= 0.40 m	257.6	22892	5206
Tipo 3	34	# 3	c/ 0.075	L= 2.90 m	85	# 3	c/ 0.075	L= 0.40 m	164	# 3	c/ 0.200	L= 2.90 m	140	# 3	c/ 0.200	L= 0.40 m									74.4	4471	1488
Tipo 4	34	# 3	c/ 0.075	L= 3.20 m	102	# 3	c/ 0.075	L= 0.40 m	164	# 3	c/ 0.200	L= 3.20 m	168	# 3	c/ 0.200	L= 0.40 m									208.3	12420	4153
Tipo 5	84	# 3	c/ 0.200	L= 3.20 m	90	# 3	c/ 0.200	L= 0.40 m	34	# 3	c/ 0.075	L= 3.20 m	102	# 3	c/ 0.075	L= 0.40 m	132	# 3	c/ 0.200	L= 3.20 m	138	# 3	c/ 0.200	L= 0.40 m	154.6	19639	3132
																									993.9	***86207***	***20042***

CUADRO RESUMEN DE REFUERZO DE BARRETES

V_C: Volúmen de concreto barretes Se calcula con la longitud "L" que se indica en el corte típico.

W_{RL}: Peso Refuerzo Longitudinal

NOTA: Éstas cantidades no incluyen desperdicios

W_{RT}: Peso Refuerzo Transversal

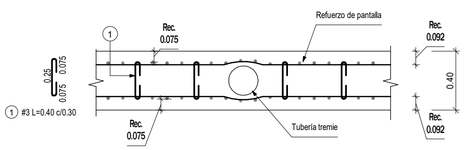

DETALLE DE TUBERÍA TREMIE PARA BARRETES
Escala 1 : 25

CONCRETO

f'c=28 MPa
f'c=280 kg/cm²
f'c=4000 psi

NOTAS

1. Ver detalles generales en PL N° 01.02 y 01.03
2. Ver planta de localización de pilotes, pantallas y barretes en PL N° 02.00
3. Se ha diseñado las pantallas y los barretes para una sobrecarga q=2.0 ton/m²

NOTA:
La longitud ó profundidad del pilote deberá ser revisada y aprobada en obra por el Ingeniero de Suelos para garantizar que la capacidad del elemento sea la establecida en el estudio de suelos.

VºBº INGENIERO DE SUELOS

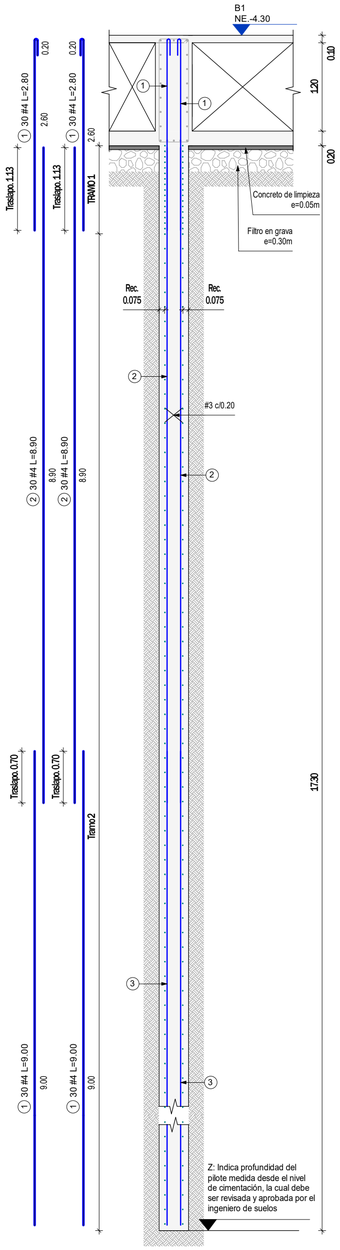

DESPIECE BARRETES TIPO 4
Escala 1 : 50

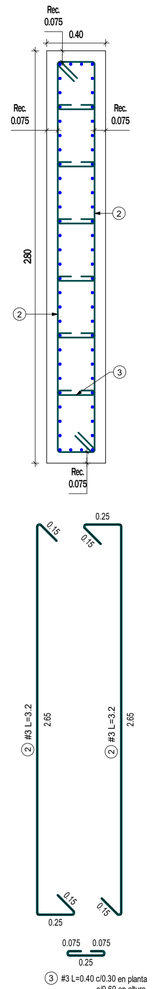

SECCIÓN BARRETE TIPO 4
S=40x280
Escala 1 : 25

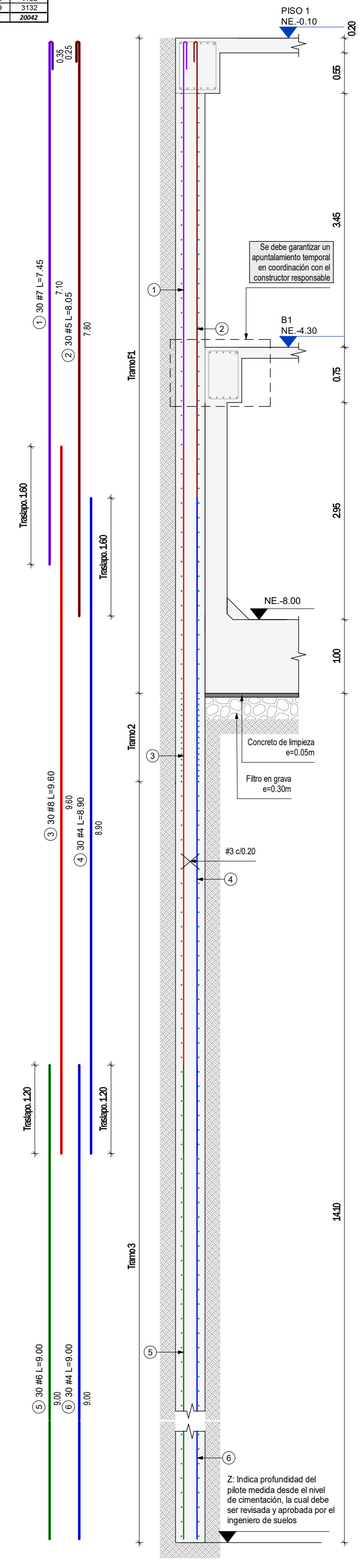

DESPIECE BARRETES TIPO 5
Escala 1 : 50

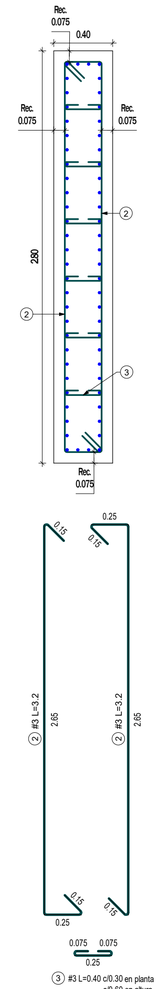

SECCIÓN BARRETE TIPO 5
S=40x280
Escala 1 : 25

VERSIÓN : 0

PLANO Nº 02.05

Aycardi Estructural

GERENTE DE PROYECTO
LUIS ENRIQUE AYCARDI F.
MAT. 2520212794 CND

INGENIERO
DANIEL E. QUICANO C.

MODELADOR
PAULA ANDREA MONTOYA RENDÓN

MODIFICACIONES	FECHA
Emisión Inicial	21-11-2025

HUMANISE STUDIO

EAN-0519- AES-01-EST

Calle 71 #9-84

DESPIECE DE BARRETES

EAN-0519 -AES-01-EST-CIM-PL-507 02.05

REVISOR ESTRUCTURAL
JULIO CESAR SANMIGUEL CAMACHO
MAT. 25202-57738 CND

PLANO Nº 02.05 VERSIÓN : 0