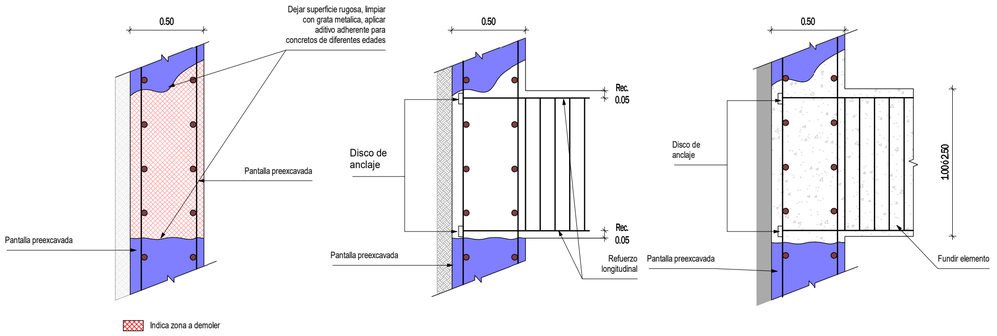

Demoler cuidadosamente conservando el refuerzo existente

Armar viga teniendo en cuenta que se debe colocar varillas de refuerzo longitudinal dentro de la pantalla con disco de anclaje

Fundir tramo del elemento que está en contacto con la pantalla con el mismo concreto de la placa

PASO 1 **PASO 2** **PASO 3**

DETALLE 1 - VINCULACIÓN VIGAS DE CIMENTACIÓN PERPENDICULARES A LA PANTALLA PRE-EXCAVADA CON DISCO DE ANCLAJE

Sin escala

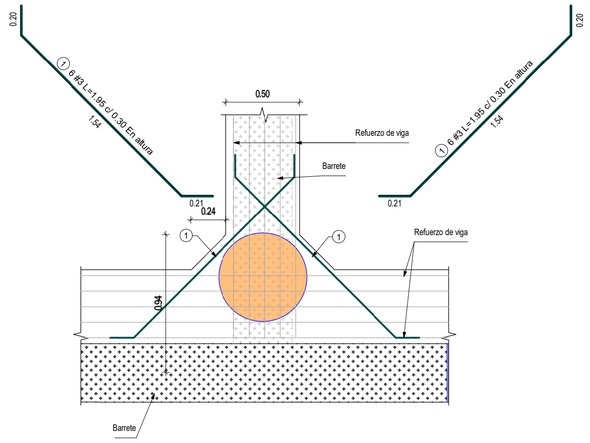

DETALLE 1 VIGAS CIMENTACIÓN h=1.50m

Escala 1 : 25

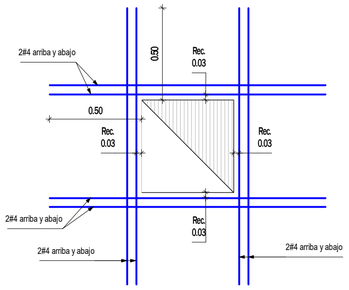

DETALLE TÍPICO REFUERZO ADICIONAL PARA DUCTOS

Escala 1 : 20

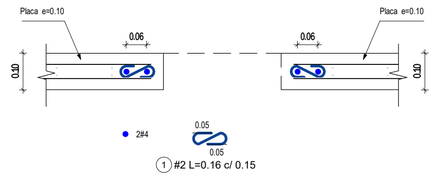

ALZADO REFUERZO ADICIONAL EN DUCTOS

Escala 1 : 10

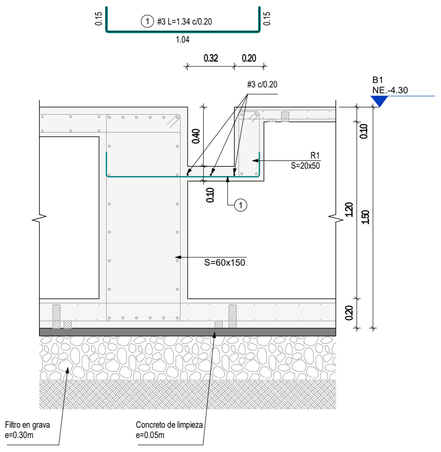

CORTE TÍPICO DE CÁRCAMO

Escala 1 : 25

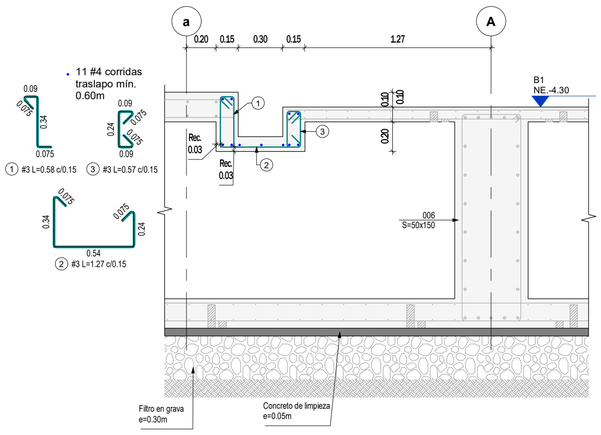

CORTE TÍPICO CÁRCAMO ZONA ANFITEATRO

Escala 1 : 25

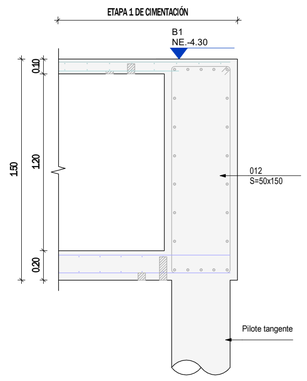

CORTE 1 - 1 ETAPA 1

Escala 1 : 25

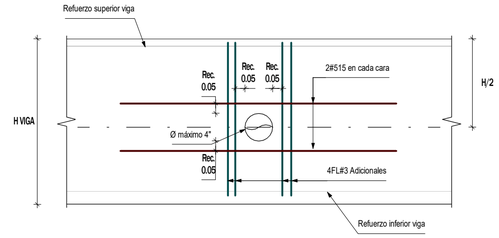

NOTA: La separación mínima entre centros de pases es de 12" y deberan ser cordinados y aprobados por la estructura.

DETALLE PASE EN VIGAS DE CIMENTACIÓN

Escala 1 : 20

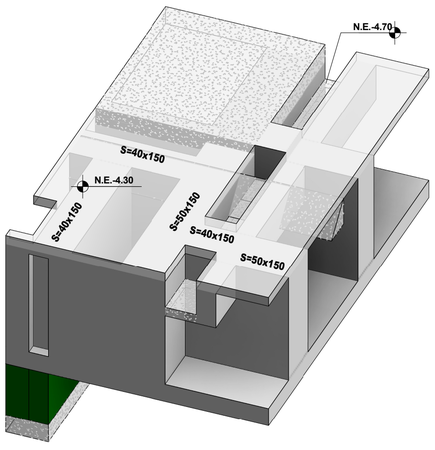

ESQUEMA 3D CÁRCAMO EN CIMENTACIÓN

Sin escala

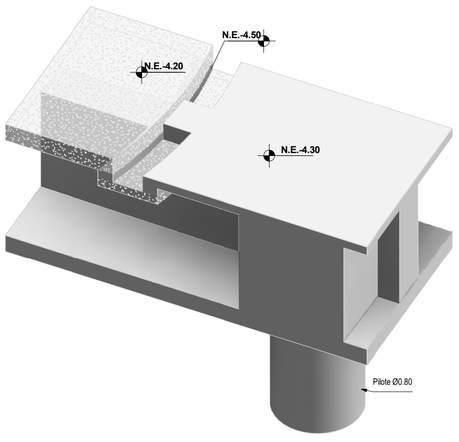

ESQUEMA 3D CARCAMO ZONA DE ANFITEATRO

Sin escala

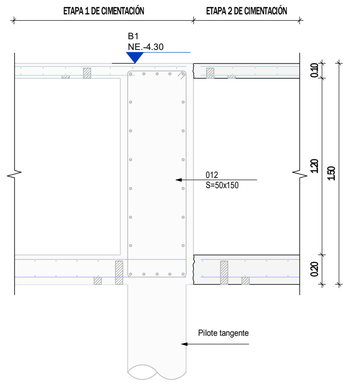

CORTE 1 - 1 ETAPA 2

Escala 1 : 25

VERSIÓN : 0

PLANO N° 06.02

Aycardi Estructural

GERENTE DE PROYECTO
LUIS ENRIQUE AYCARDI F.
MAT. 2520212794 CND

INGENIERO
DANIEL E. QUICANO C.

MODELADOR
PAULA ANDREA MONTOYA RENDÓN

MODIFICACIONES	FECHA
Emisión Inicial	21-11-2025

HUMANISE STUDIO

EAN-0519- AES-01-EST

Calle 71 #9-84

CORTES Y ESQUEMAS 3D

EAN-0519 -AES-01-EST-CIM-PL-518 06.02

REVISOR ESTRUCTURAL
JULIO CESAR SANMIGUEL CAMACHO
MAT. 25202-57738 CND

PLANO N° 06.02 VERSIÓN : 0