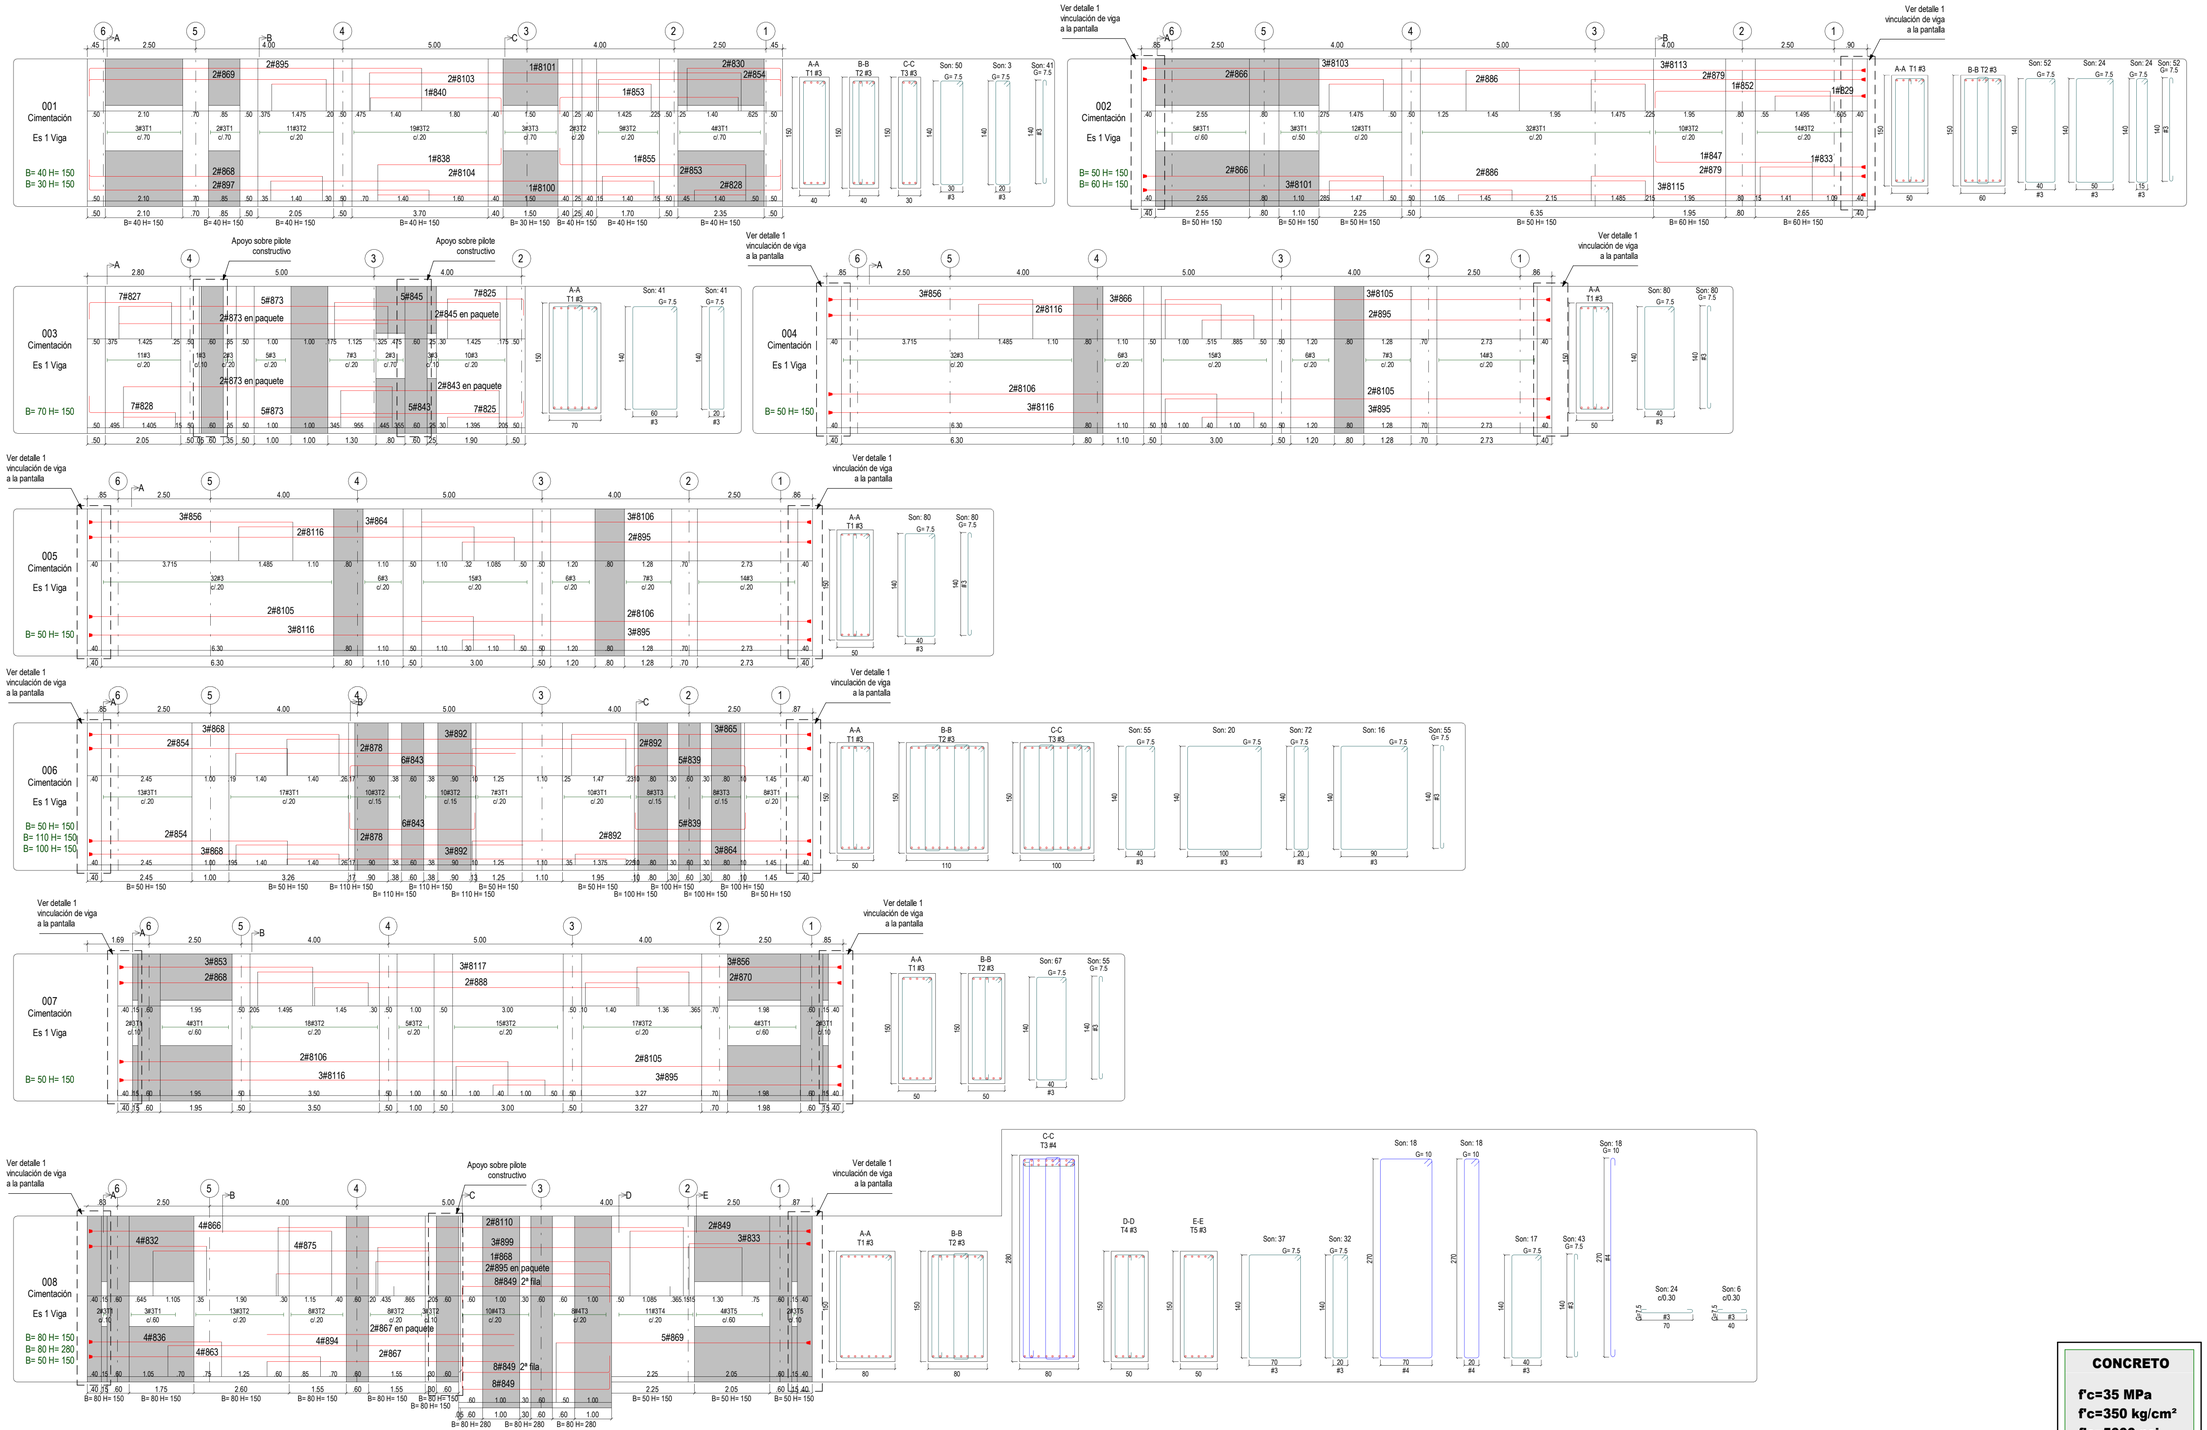

CONCRETO

f'c=35 MPa
f'c=350 kg/cm²
f'c=5000 psi

CONVENCIONES

Indica disco de anclaje

NOTAS

1. Ver detalle de vigas altas en PL N° 01.02
2. Ver detalles generales en PL N° 01.02 y 01.03
3. Ver planta de cimentación en PL N° 06.00
4. Ver detalle 1 vinculación de viga a pantalla en el PL N° 06.02
5. Ver detalle 3 vinculación viga a pilote constructivo en el PL N° 06.04

VERSIÓN : 0

PLANO N° 06.03

Aycardi Estructural

GERENTE DE PROYECTO
LUIS ENRIQUE AYCARDI F.
MAT. 2520212794 CND

INGENIERO
DANIEL E. QUICANO C.

MODELADOR
PAULA ANDREA MONTOYA RENDÓN

MODIFICACIONES	FECHA
Emisión Inicial	21-11-2025

HUMANISE STUDIO

EAN-0519- AES-01-EST

Calle 71 #9-84

DESPIECES DE VIGAS DE CIMENTACIÓN

EAN-0519 -AES-01-EST-CIM-PL-519 06.03

REVISOR ESTRUCTURAL
JULIO CESAR SANMIGUEL CAMACHO
MAT. 25202-57738 CND

PLANO N° 06.03 VERSIÓN : 0