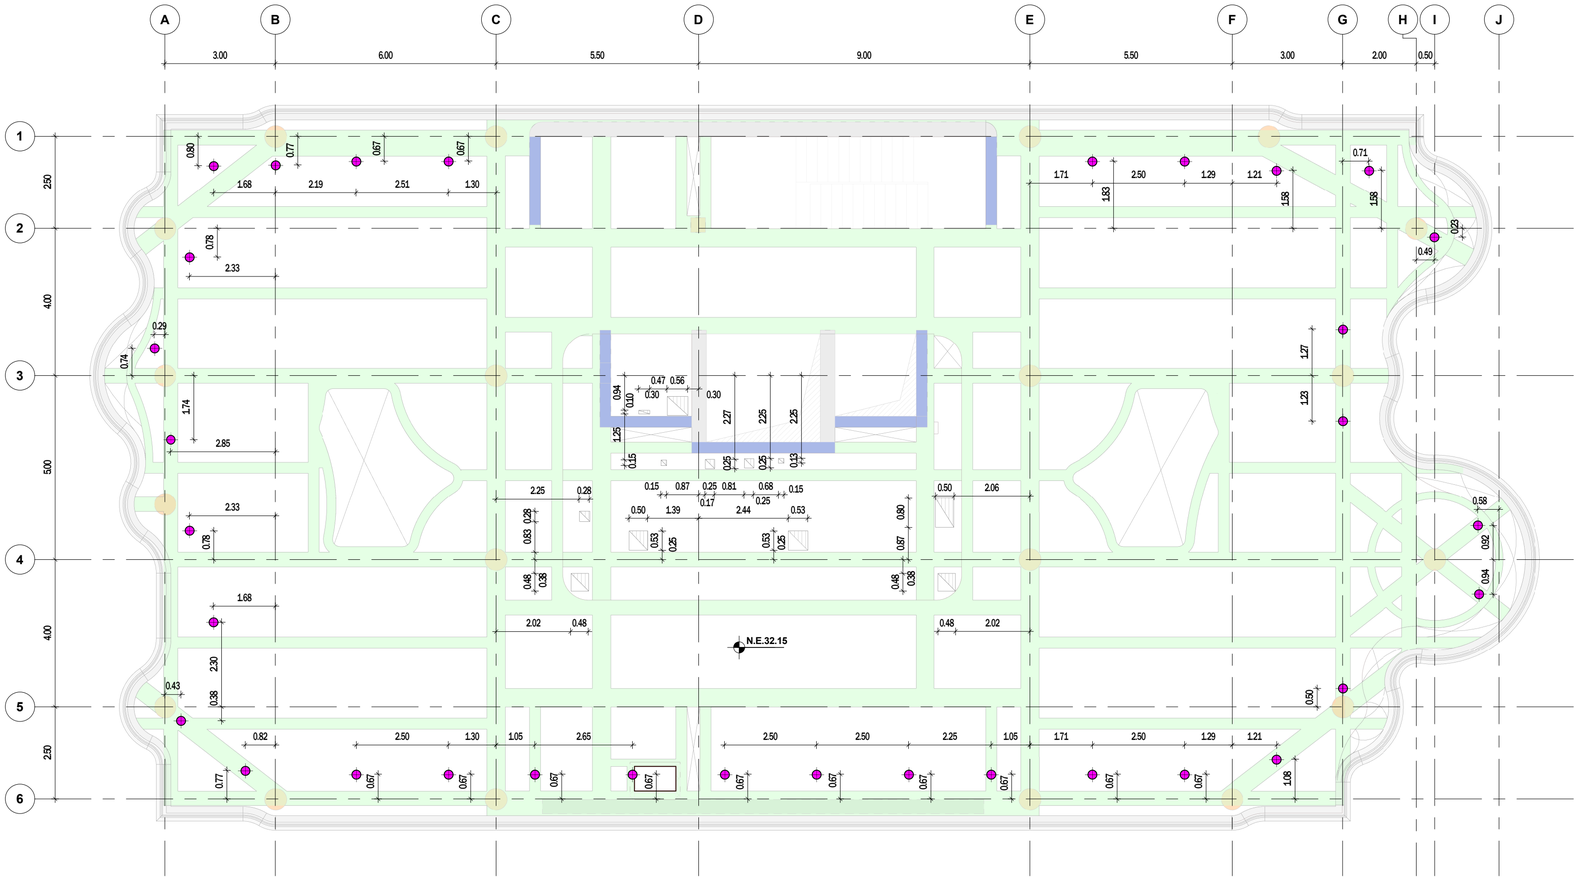

PLANTA DE LOCALIZACIÓN DE PUNTOS DE ANCLAJE Y DUCTOS DE CUBIERTA

Escala 1 : 100

CONVENCIONES

Indica punto de anclaje para mantenimiento de fachada. Los embebidos seran indicados en el plano de diseño elaborado por el proveedor de los anclajes.

NOTAS

1. Ver planta de cubierta en PL N° 14.00

VERSIÓN : 0

PLANO N° 14.02

Aycardi Estructural

GERENTE DE PROYECTO
LUIS ENRIQUE AYCARDI F.
MAT. 2520212794 CND

INGENIERO
DANIEL E. QUICANO C.

MODELADOR
PAULA ANDREA MONTOYA RENDÓN

MODIFICACIONES	FECHA
Emisión Inicial	21-11-2025

HUMANISE STUDIO

EAN-0519- AES-01-EST

Calle 71 #9-84

PLANTA DE LOCALIZACIÓN DE PUNTOS DE ANCLAJE Y DUCTOS DE CUBIERTA

EAN-0519 -AES-01-EST-CUB-PL-574 14.02

REVISOR ESTRUCTURAL
JULIO CESAR SANMIGUEL CAMACHO
MAT. 25202-57738 CND

PLANO N° 14.02 VERSIÓN : 0