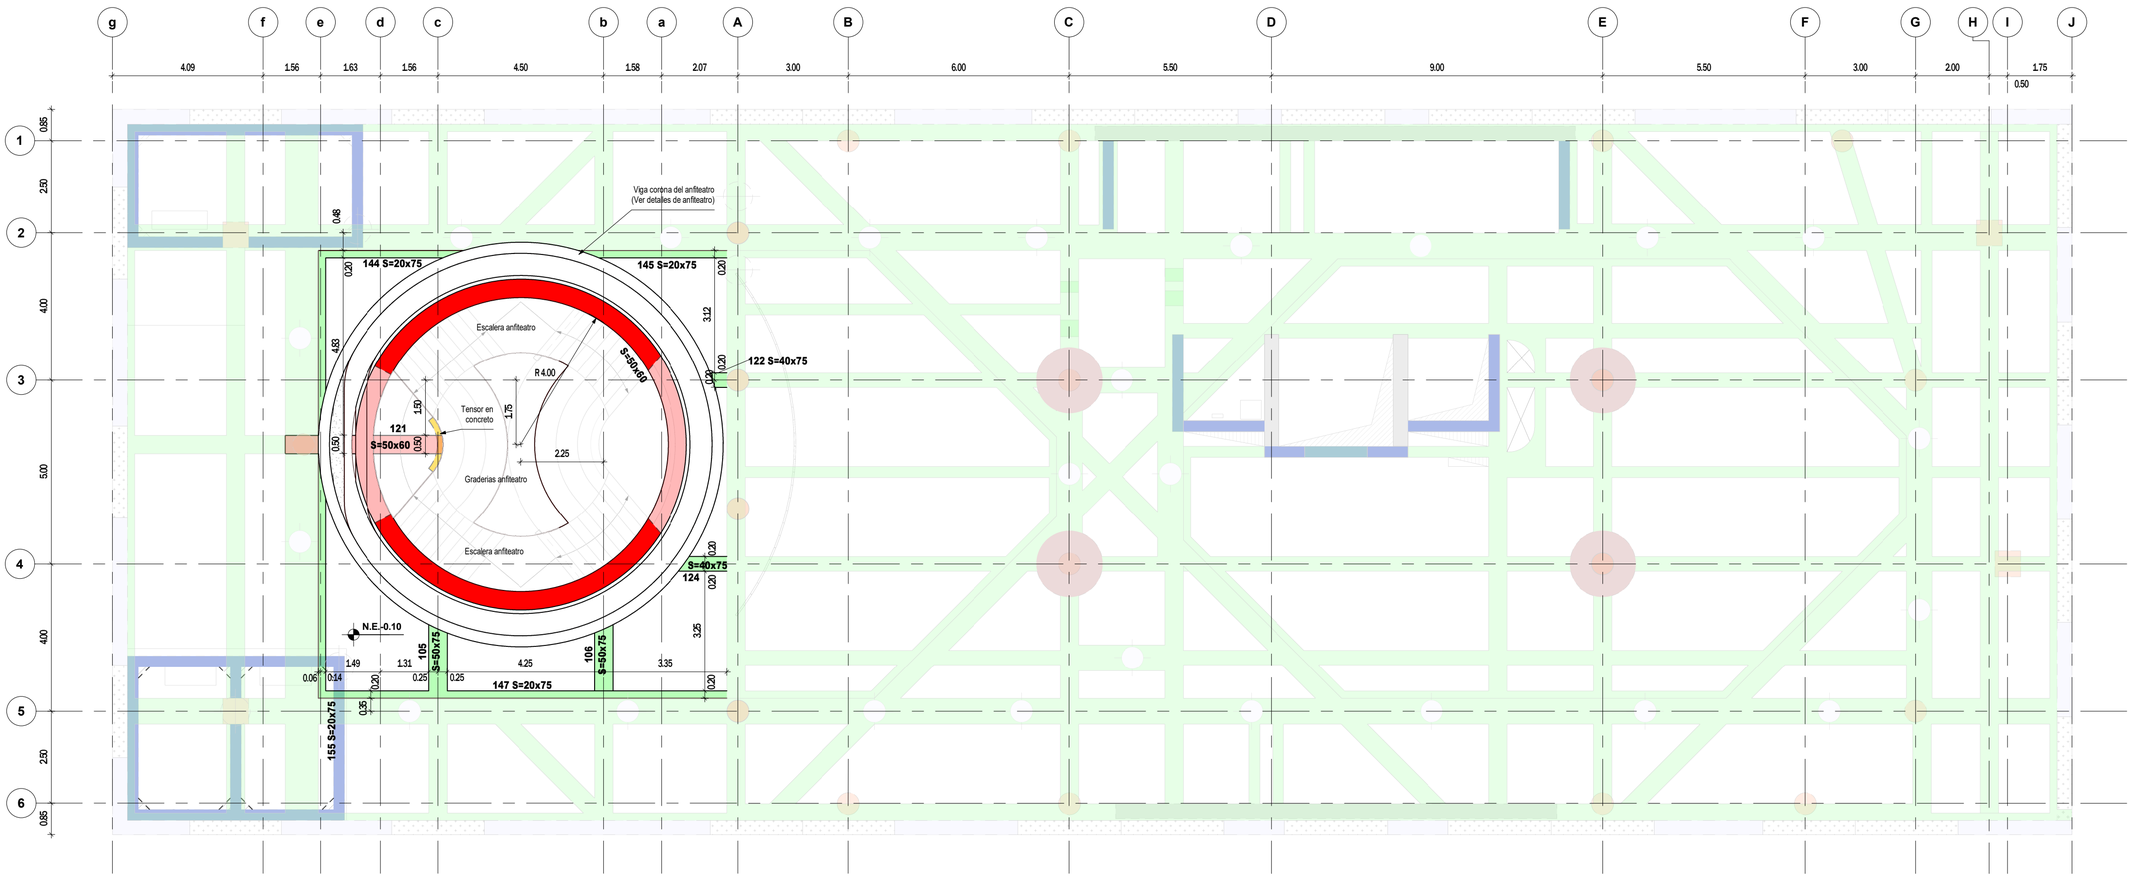

PLANTA DE PISO 1 ETAPA 4 (COMPLEMENTO ANFITEATRO)
Escala 1 : 100

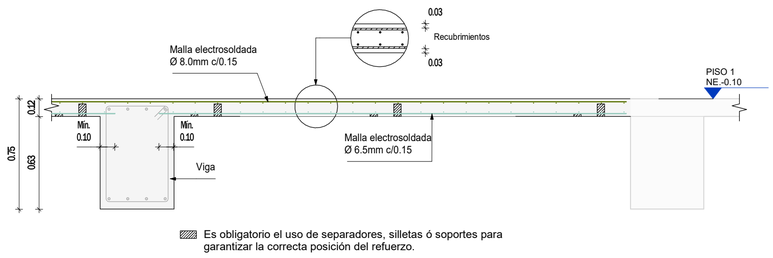

CORTE TÍPICO DE PLACA
Escala 1 : 25

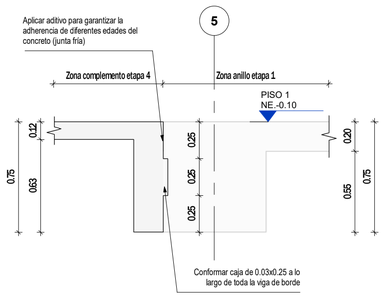

DETALLE 1 VINCULACIÓN DE VIGAS ETAPA 1 Y ETAPA 4
Escala 1 : 25

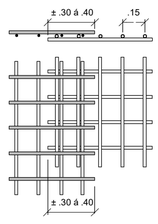

DETALLE TRASLAPO MALLAS
Escala 1 : 25

CONCRETO

f'c=35 MPa
f'c=350 kg/cm²
f'c=5000 psi

CONVENCIONES

- Indica pilotes constructivos
- Indica columna S=Ø60
- Indica capitel Ø180
- Indica muro e=30
- Indica muro e=40
- Indica muro e=50
- Indica viga h=60
- Indica viga h=75
- Indica demolición cuidadosa sin conservar el refuerzo

NOTAS

1. Ver detalles generales en PL N° 01.02 y 01.03
2. Ver cortes y esquema 3D en el PL N° 07.07

VERSIÓN : 0

PLANO N° 07.06

Aycardi Estructural

GERENTE DE PROYECTO
LUIS ENRIQUE AYCARDI F.
MAT. 2520212794 CND

INGENIERO
DANIEL E. QUICANO C.

MODELADOR
PAULA ANDREA MONTOYA RENDÓN

MODIFICACIONES	FECHA
Emisión Inicial	21-11-2025

HUMANISE STUDIO

EAN-0519- AES-01-EST

Calle 71 #9-84

PLANTA DE PISO 1 ETAPA 4 (COMPLEMENTO ANFITEATRO)

EAN-0519 -AES-01-EST-N01-PL-107 07.06

REVISOR ESTRUCTURAL
JULIO CESAR SANMIGUEL CAMACHO
MAT. 25202-57738 CND

PLANO N° 07.06 VERSIÓN : 0