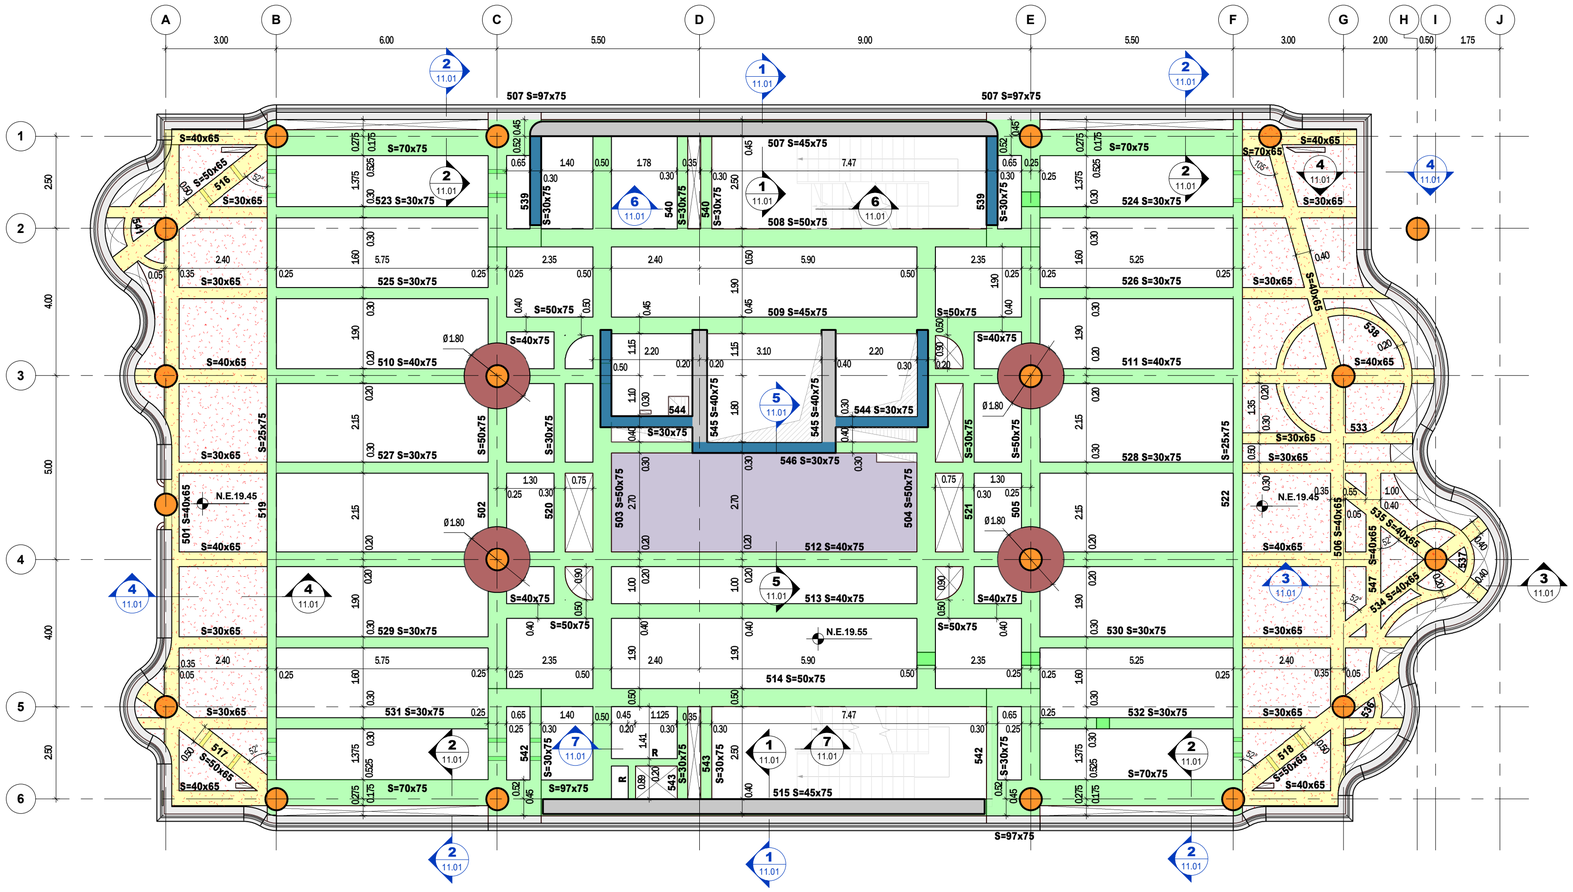

PLANTA DE PISO 5
Escala 1 : 100

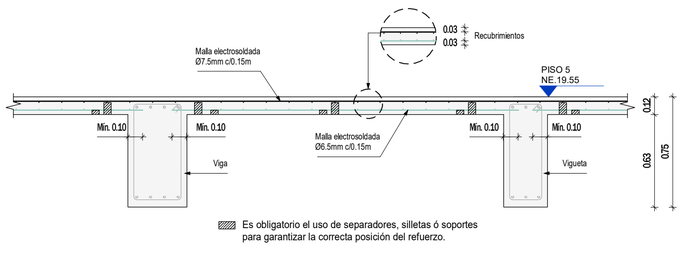

CORTE TÍPICO DE PLACA
Escala 1 : 25

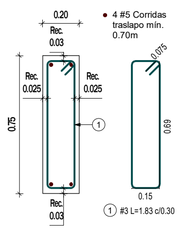

RIOSTRA (R) S=20x75
Escala 1 : 20

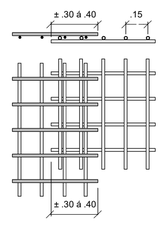

DETALLE TRASLAPO MALLAS
Escala 1 : 25

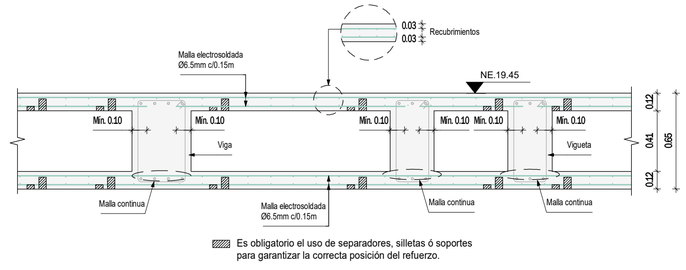

CORTE TÍPICO DE PLACA ZONA BALCONES
Escala 1 : 25

CONCRETO

f'c=35 MPa
f'c=350 kg/cm²
f'c=5000 psi

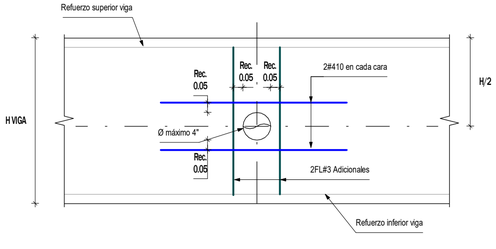

DETALLE PASE EN VIGAS AEREAS
Escala 1 : 20

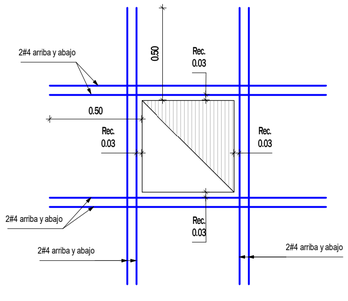

DETALLE TÍPICO REFUERZO ADICIONAL PARA DUCTOS
Escala 1 : 20

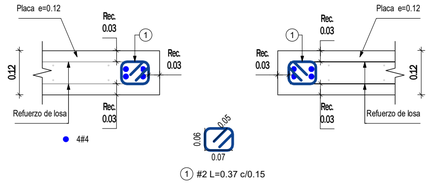

ALZADO REFUERZO ADICIONAL EN DUCTOS
Escala 1 : 10

CONVENCIONES

- Indica columna S=Ø60
- Indica capitel Ø180
- Indica muro e=30
- Indica muro e=40
- Indica viga h=75
- Indica viga h=65
- Indica pase en viga h=75
- Indica pase en viga h=65
- Indica zona con refuerzo especial (Ver corte 5 - 5)
- Indica zona de balcones NE. +19.45 (Ver corte típico zona de balcones)

NOTAS

1. Ver detalles generales en el PL. 01.02 y 01.03
2. Ver cortes en el PL N° 11.1
3. Ver esquemas 3D en el PL N° 11.2
4. Ver despieces de vigas en los PL. N° 11.03 a 11.06
5. Previo a la fundida del concreto se deben instalar los sistemas de anclaje embebidos para el soporte de los capiteles cerámicos. Ver diseños de ESTAHL.

VERSIÓN : 0

PLANO N° 11.00

Aycardi Estructural

GERENTE DE PROYECTO
LUIS ENRIQUE AYCARDI F.
MAT. 2520212794 CND

INGENIERO
DANIEL E. QUICANO C.

MODELADOR
PAULA ANDREA MONTOYA RENDÓN

MODIFICACIONES	FECHA
Emisión Inicial	21-11-2025

HUMANISE STUDIO

EAN-0519- AES-01-EST

Calle 71 #9-84

PLANTA DE PISO 5

EAN-0519 -AES-01-EST-N05-PL-112 11.00

REVISOR ESTRUCTURAL
JULIO CESAR SANMIGUEL CAMACHO
MAT. 25202-57738 CND

PLANO N° 11.00 VERSIÓN : 0