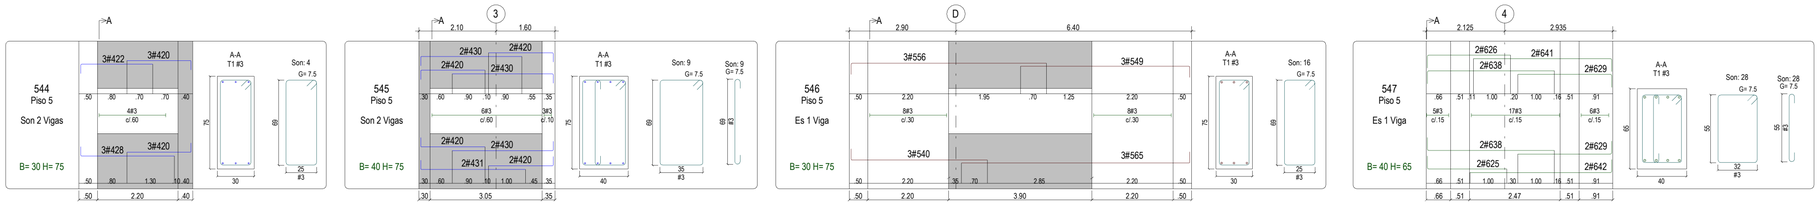


**NOTAS**

1. Ver detalles generales en PL N° 01.02 y 01.03
2. Ver planta de piso 5 en PL N°11.00

VERSIÓN : 0

PLANO N° 11.06

Aycardi Estructural

GERENTE DE PROYECTO

LUIS ENRIQUE AYCARDI F.
**MAT. 2520212794 CND**

INGENIERO

DANIEL E. QUICANO C.

MODELADOR

PAULA ANDREA MONTOYA RENDÓN

| MODIFICACIONES | FECHA |
|---|---|
| Emisión Inicial | 21-11-2025 |
| | |
| | |
| | |
| | |
| | |

**HUMANISE STUDIO**

EAN-0519- AES-01-EST

Calle 71 #9-84

**DESPIECE DE VIGAS PISO 5**

EAN-0519 -AES-01-EST-N05-PL-561 11.06

REVISOR ESTRUCTURAL

JULIO CESAR SANMIGUEL CAMACHO
MAT. 25202-57738 CND

PLANO N° 11.06

VERSIÓN : 0