


## PLANTA DE PISO 6
**Escala 1 : 100**

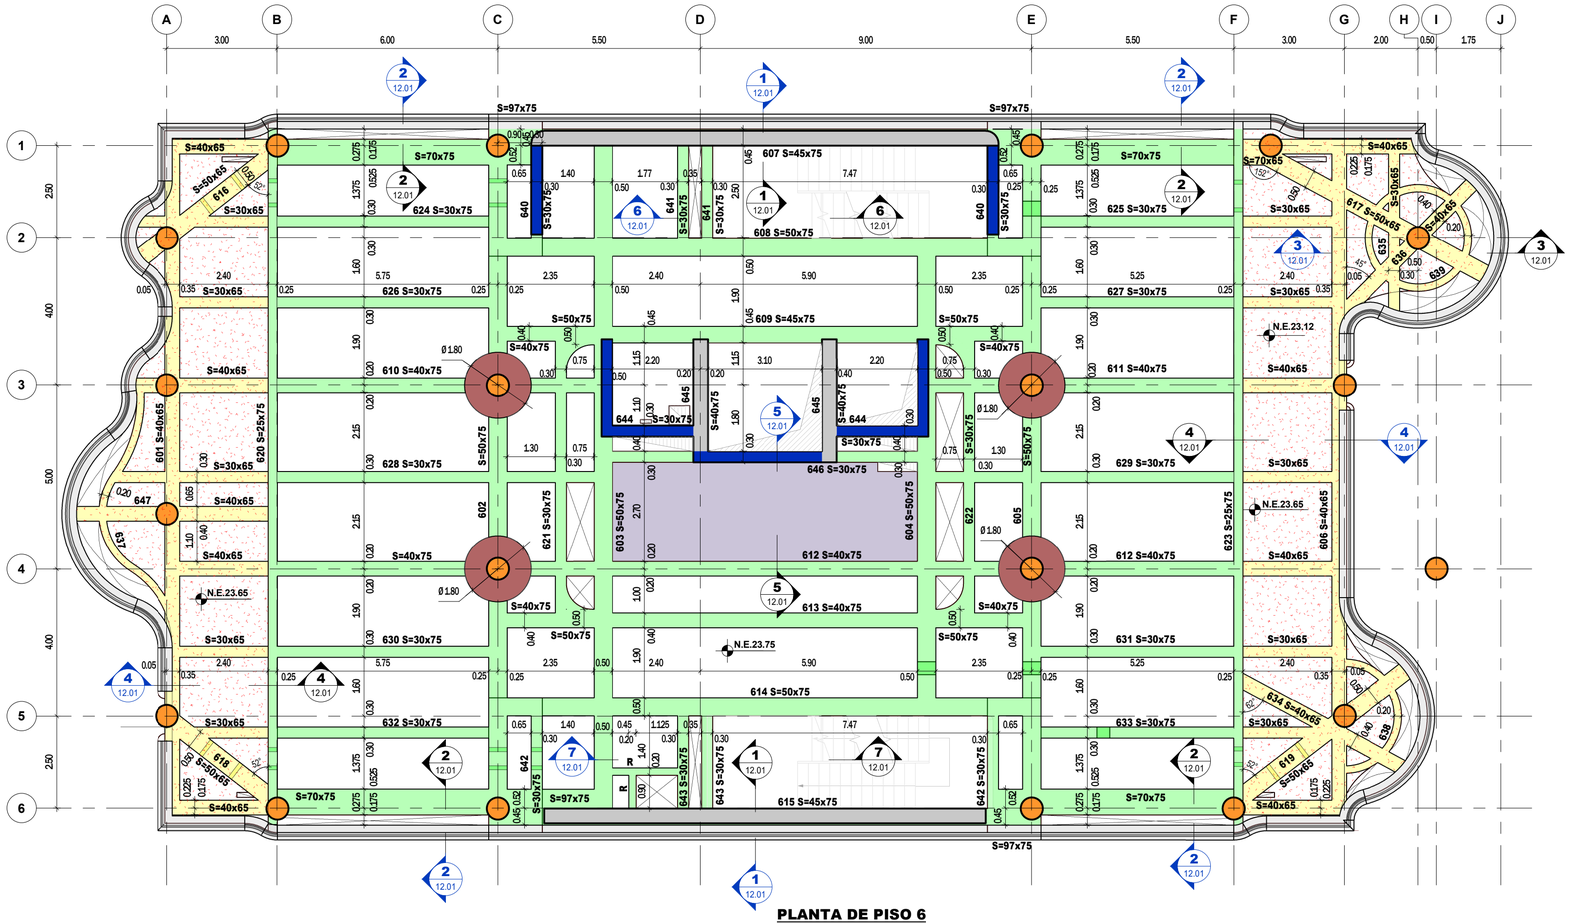


## CORTE TÍPICO DE PLACA
**Escala 1 : 25**




## RIOSTRA (R) S=20x75
**Escala 1 : 20**

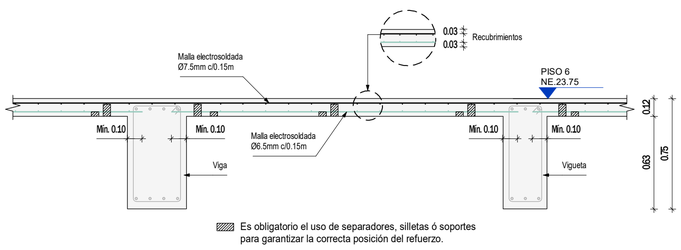


## DETALLE TRASLAPO MALLAS
**Escala 1 : 25**

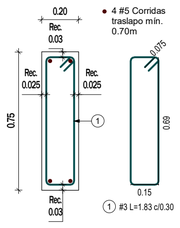


## CORTE TÍPICO DE PLACA ZONA BALCONES
**Escala 1 : 25**

**CONCRETO**

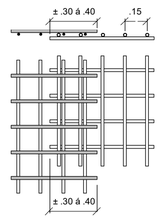**f'c=35 MPa**
**f'c=350 kg/cm²**
**f'c=5000 psi**

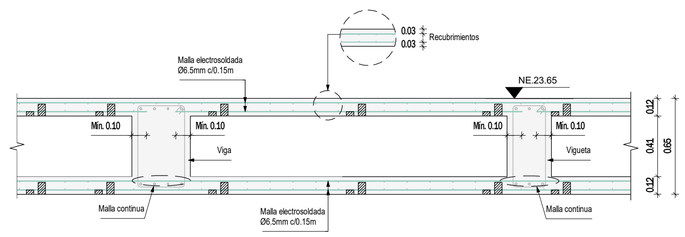


## DETALLE PASE EN VIGAS AEREAS
**Escala 1 : 20**




## DETALLE TÍPICO REFUERZO ADICIONAL PARA DUCTOS
**Escala 1 : 20**

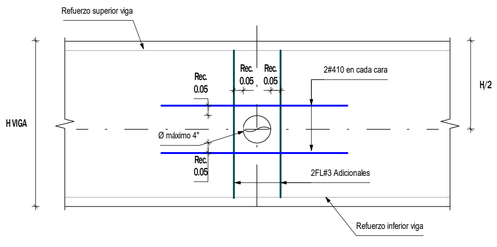


## ALZADO REFUERZO ADICIONAL EN DUCTOS
**Escala 1 : 10**

**CONVENCIONES**

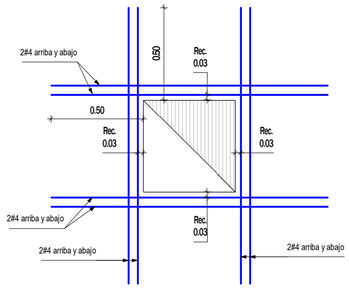- Indica columna S=Ø60
- Indica capitel Ø180
- Indica muro e=30
- Indica muro e=40
- Indica viga h=75
- Indica viga h=65
- Indica pase en viga h=75
- Indica pase en viga h=65
- Indica zona con refuerzo especial (Ver corte 5 - 5)
- Indica zona de balcones NE. +23.65 (Ver corte típico zona de balcones)

**NOTAS**

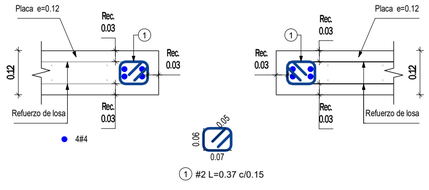1. Ver detalles generales en el PL. 01.02 y 01.03
2. Ver cortes en el PL N° 12.01
3. Ver esquemas 3D en el PL N° 12.02
4. Ver despieces de vigas en los PL. N° 12.03 - 12.06
5. Previo a la fundida del concreto se deben instalar los sistemas de anclajes embebidos para el soporte de los capiteles cerámicos. Ver diseños de ESTAHL

VERSIÓN : 0

PLANO N° 12.00

Aycardi Estructural

GERENTE DE PROYECTO
LUIS ENRIQUE AYCARDI F.
**MAT. 2520212794 CND**

INGENIERO
DANIEL E. QUICANO C.

MODELADOR
PAULA ANDREA MONTOYA RENDÓN

| MODIFICACIONES | FECHA |
|---|---|
| Emisión Inicial | 21-11-2025 |
| | |
| | |
| | |
| | |
| | |

**HUMANISE STUDIO**

EAN-0519- AES-01-EST

Calle 71 #9-84

**PLANTA DE PISO 6**

EAN-0519 -AES-01-EST-N06-PL-113 12.00

REVISOR ESTRUCTURAL
JULIO CESAR SANMIGUEL CAMACHO
MAT. 25202-57738 CND

PLANO N° 12.00 VERSIÓN : 0