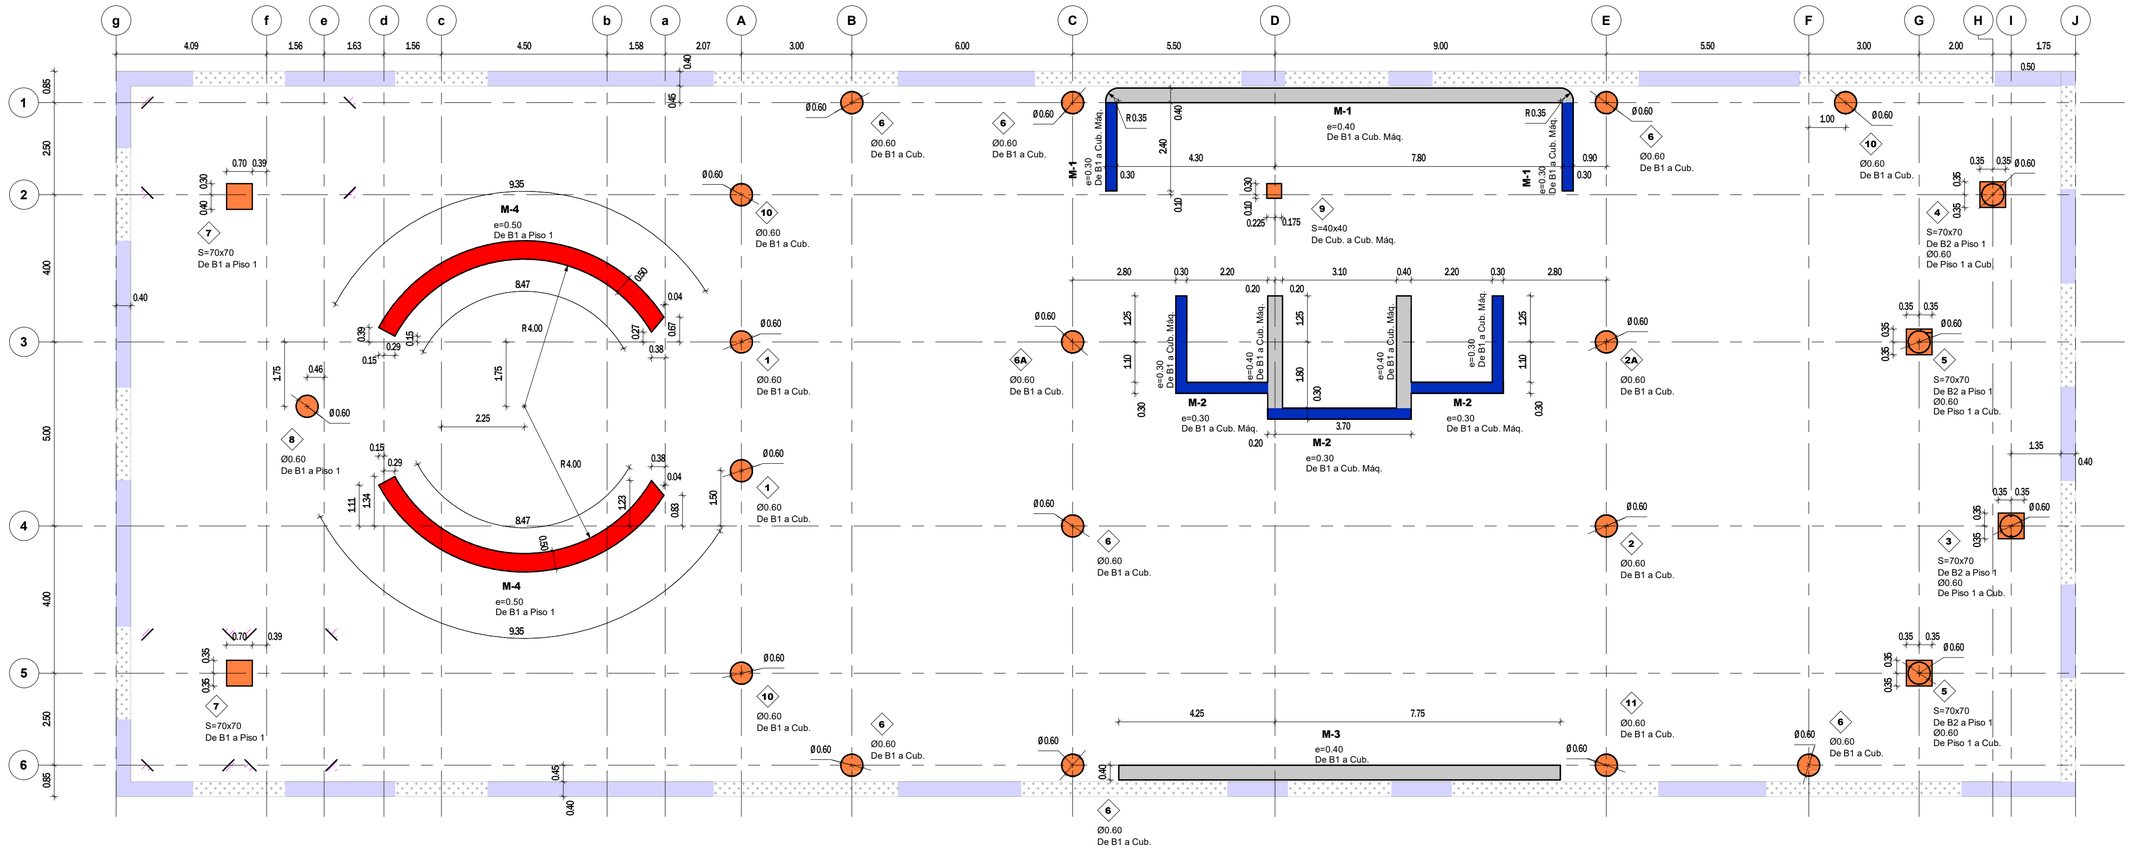

PLANTA DE LOCALIZACIÓN Y DESARROLLO DE MUROS Y COLUMNAS
Escala 1 : 100

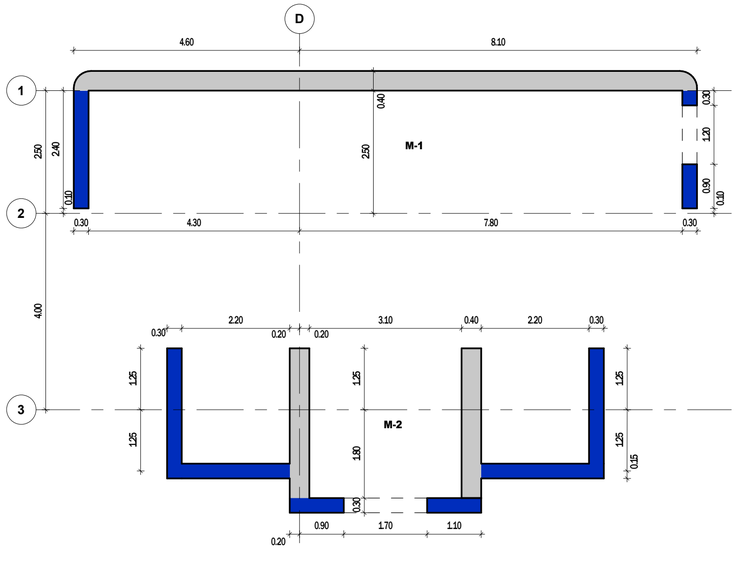

PLANTA DE LOALIZACIÓN DE VANOS EN MUROS
Escala 1 : 75

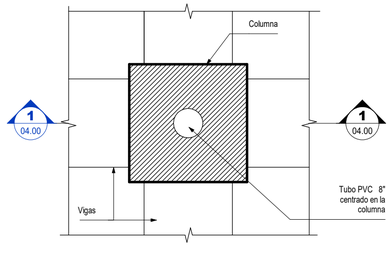

PLANTA NUDO EN COLUMNA EN PROCESO CONSTRUCTIVO
Escala 1 : 25

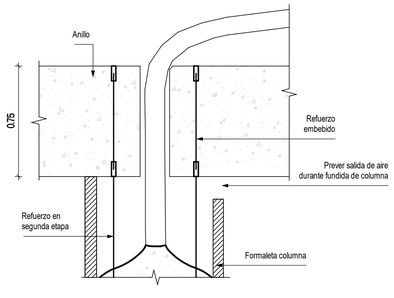

CORTE 1 - 1 ETAPA 1
Escala 1 : 25

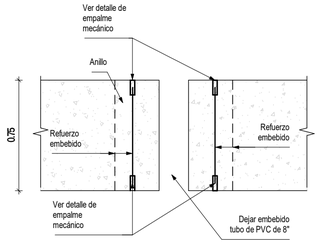

CORTE 1 - 1 ETAPA 1
Escala 1 : 25

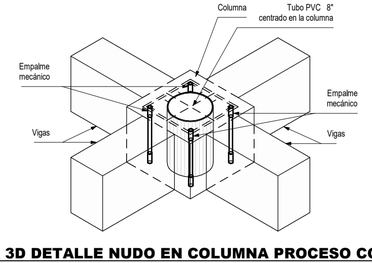

ESQUEMA 3D DETALLE NUDO EN COLUMNA PROCESO CONSTRUCTIVO
Sin escala

CONCRETO

De cimentación a piso 4	De piso 4 a cubierta
f'c=42 MPa	**f'c=35 MPa**
f'c=420 kg/cm²	**f'c=350 kg/cm²**
f'c=6000 psi	**f'c=5000 psi**

CONVENCIONES

- # Indica tipo de columna
- M-M-# Indica tipo de muro
- Indica barrete
- Indica pantalla preexcavada 0.40
- Indica columna S=Ø0.60
- Indica muro e=0.30
- Indica muro e=0.40
- Indica muro e=0.50

NOTAS

1. Ver detalles generales en el PL. N° 01.02 y 01.03
2. Ver despieces de columnas en el PL. N° 04.01 y 04.04
3. Ver despieces de muros en los PL. N° 04.05 y 04.07

NOTA

El constructor deberá garantizar el cumplimiento de las tolerancias máximas definidas en la NSR-10

VERSIÓN : 0

PLANO N° 04.00

Aycardi Estructural

GERENTE DE PROYECTO
LUIS ENRIQUE AYCARDI F.
MAT. 2520212794 CND

INGENIERO
DANIEL E. QUICANO C.

MODELADOR
PAULA ANDREA MONTOYA RENDÓN

MODIFICACIONES	FECHA
Emisión Inicial	21-11-2025

HUMANISE STUDIO

EAN-0519- AES-01-EST

Calle 71 #9-84

PLANTA LOCALIZACIÓN DE MUROS Y COLUMNAS

EAN-0519 -AES-01-EST-PL-102 04.00

REVISOR ESTRUCTURAL
JULIO CESAR SANMIGUEL CAMACHO
MAT. 25202-57738 CND

PLANO N° 04.00 VERSIÓN : 0