PLANTA DE CIMENTACIÓN
Escala 1 : 100

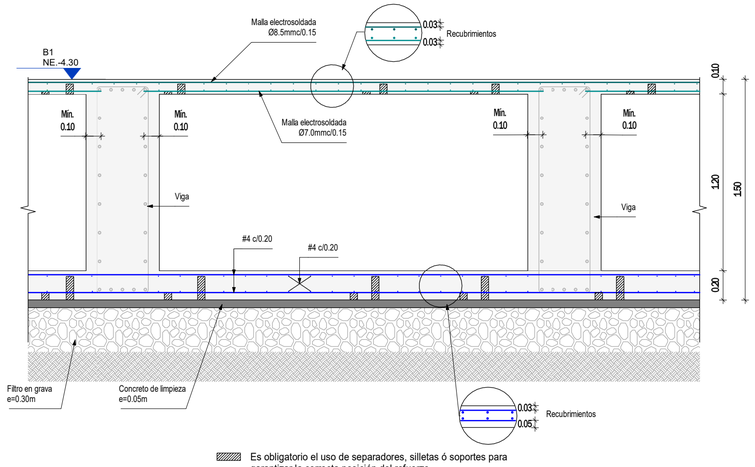

Es obligatorio el uso de separadores, silletas ó soportes para garantizar la correcta posición del refuerzo.

CORTE TÍPICO PLACA CIMENTACIÓN
Escala 1 : 25

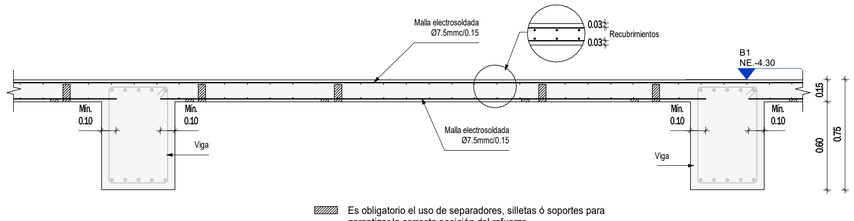

Es obligatorio el uso de separadores, silletas ó soportes para garantizar la correcta posición del refuerzo.

CORTE TÍPICO DE PLACA CIMENTACIÓN ZONA DE TANQUE
Escala 1 : 25

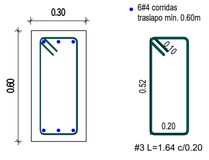

RIOSTRA R S=30x60
Escala 1 : 20

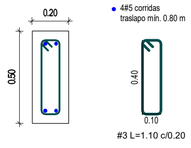

RIOSTRA R1 S=20x50
Escala 1 : 20

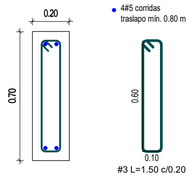

RIOSTRA R2 S=20x70
Escala 1 : 20

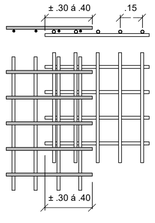

DETALLE TRASLAPO MALLAS
Escala 1 : 25

CONCRETO

f'c=35 MPa
f'c=350 kg/cm²
f'c=5000 psi

NOTA:
Este plano debe ser revisado y aprobado por el Ingeniero de suelos.

VºBº INGENIERO DE SUELOS

CONVENCIONES

- Indica tipo de dado
- Indica pilotes
- Indica pilotes tangenciales
- Indica pilotes constructivos
- Indica barretes
- Indica pantalla preexcavada
- Indica columnas
- Indica dados
- Indica muro e=20
- Indica muro e=30
- Indica muro e=40
- Indica muro e=50
- Indica viga h=75
- Indica viga h=150
- Indica viga h=280
- Indica pase de viga h=75
- Indica pase de viga h=150
- Indica cárcamos
- Indica placa e=0.15m
- Indica placa e=0.20m

NOTAS

1. Ver detalles generales en el PL. 01.02 y 01.03
2. Ver esquema 3D de cimentación en el PL N° 06.01
3. Ver cortes de carcamos y detalles en el PL N° 06.02
4. Ver despieces de vigas en los PL. N° 06.03 a 06.07
5. Ver despiece de dados en el PL N° 06.08 y 06.09
6. Ver planos de anfiteatro en los PL N° 05.00 a 05.03
7. Ver despiece de tanuques en los PL N° 16.00 a 16.03

VERSIÓN : 0

PLANO N° 06.00

Aycardi Estructural

GERENTE DE PROYECTO
LUIS ENRIQUE AYCARDI F.
MAT. 2520212794 CND

INGENIERO
DANIEL E. QUICANO C.

MODELADOR
PAULA ANDREA MONTOYA RENDÓN

MODIFICACIONES	FECHA
Emisión Inicial	21-11-2025

HUMANISE STUDIO

EAN-0519- AES-01-EST

Calle 71 #9-84

PLANTA DE CIMENTACIÓN

EAN-0519 -AES-01-EST-PL-103 06.00

REVISOR ESTRUCTURAL
JULIO CESAR SANMIGUEL CAMACHO
MAT. 25202-57738 CND

PLANO N° 06.00 VERSIÓN : 0