COLUMNA TIPO 6
Son 7
ESC gen. 1:100
ESC secc. 1:25

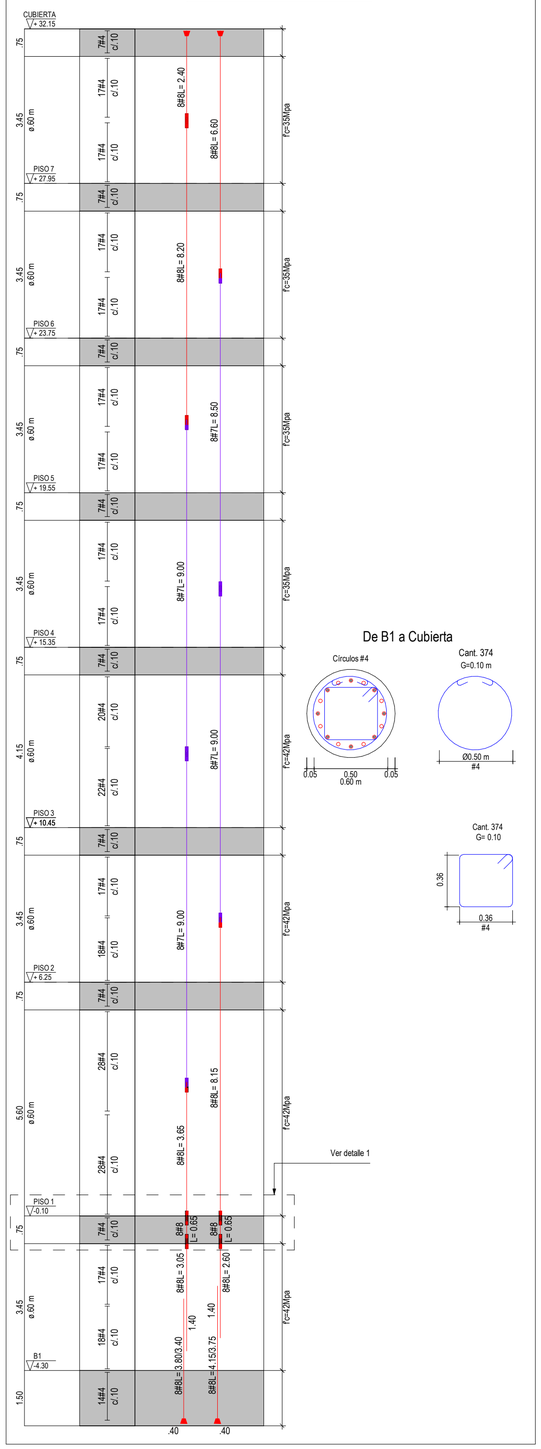


COLUMNA TIPO 6A
Es 1
ESC gen. 1:100
ESC secc. 1:25

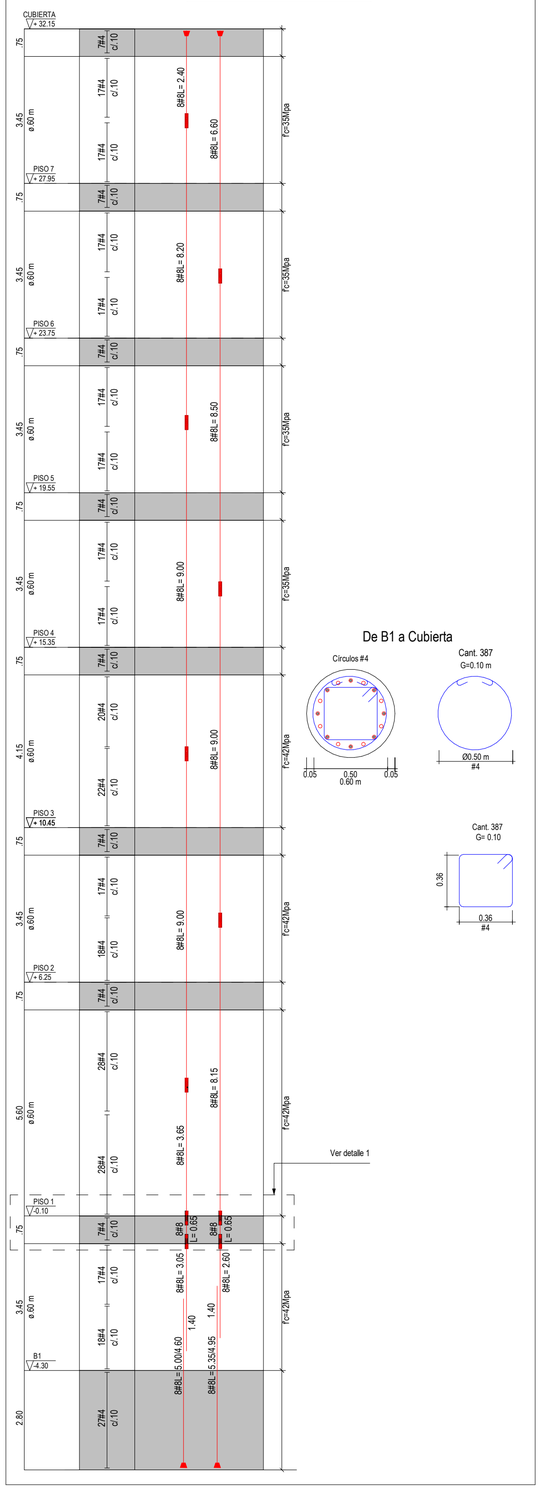


COLUMNA TIPO 7
Son 2
ESC gen. 1:100
ESC secc. 1:25

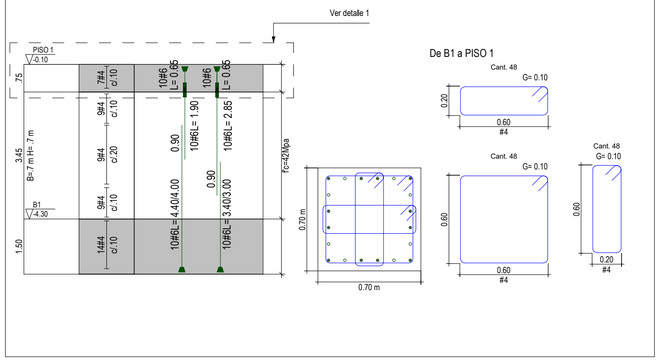


**CONVENCIONES**

Indica disco de anclaje

Indica empalme mecánico

**NOTAS**

1. Ver detalles generales en plano PL N° 01.02 y 01.03.
2. Ver planta localización e identificación de muros y columnas en PL. N° 04.00
3. Ver detalle 1 en PL.N°04.00

VERSIÓN : 0

PLANO N° 04.03

Aycardi Estructural

GERENTE DE PROYECTO
LUIS ENRIQUE AYCARDI F.
**MAT. 2520212794 CND**

INGENIERO
DANIEL E. QUICANO C.

MODELADOR
PAULA ANDREA MONTOYA RENDÓN

| MODIFICACIONES | FECHA |
|---|---|
| Emisión Inicial | 21-11-2025 |
| | |
| | |
| | |
| | |
| | |

**HUMANISE STUDIO**

EAN-0519- AES-01-EST

Calle 71 #9-84

**DESPIECE DE COLUMNAS**

EAN-0519 -AES-01-EST-PL-510 04.03

REVISOR ESTRUCTURAL
JULIO CESAR SANMIGUEL CAMACHO
MAT. 25202-57738 CND

PLANO N° 04.03 VERSIÓN : 0