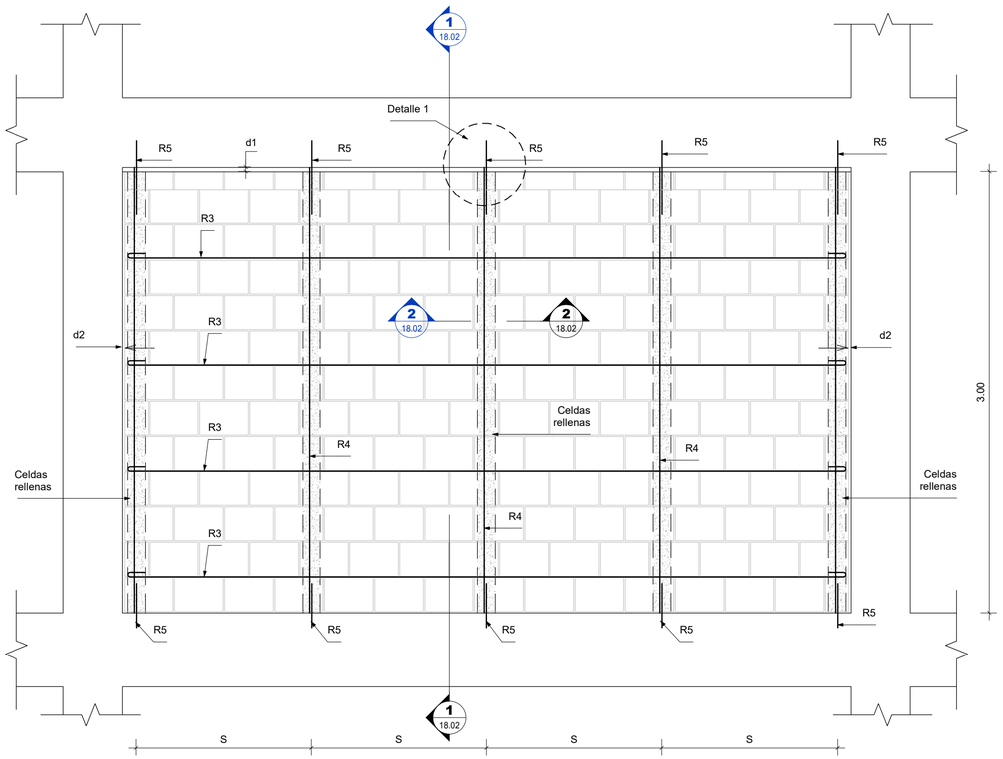

ELEVACIÓN DE MUROS INTERIORES (APLICA PARA H=3.00m)
Escala 1 : 25

S	2.00m Separación máxima entre refuerzo
R3	Son 2 Ø4mm c/ 3 Hiladas
R4	1#3 L=luz libre - 0.05m
R5	1#4 L=0.60m anclada 0.10m con resina epóxica
d1	Dilatación 0.01m (dejar icopor o similar de 0.01m)
d2	Dilatación 0.015m (dejar icopor o similar de 0.015m)

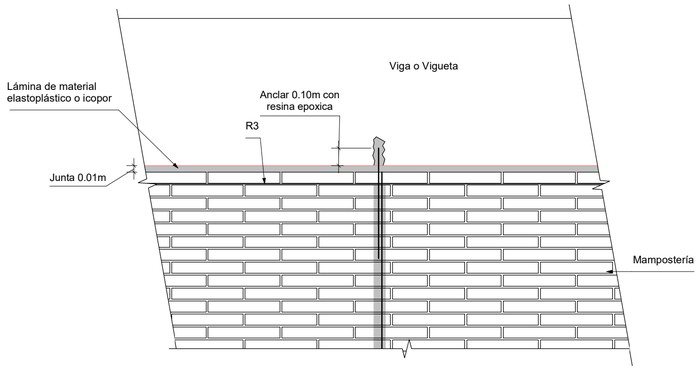

R3 2 Ø 4mm c/ 6 hiladas

DETALLE 1 - DETALLE SUPERIOR DE LADRILLO CON BLOQUE DE ICOPOR
Escala 1 : 20

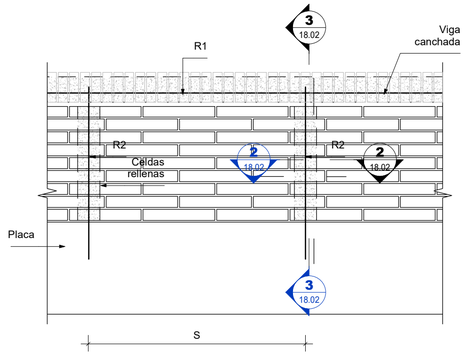

S	2.00m Separación máxima entre refuerzo
R1	Refuerzo viga cinta 2#3, flejes Ø¼" c/0.30
R2	Refuerzo antepecho 1#4 L= Variable anclada 0.10m con resina epóxica

ANTEPECHOS Y PARAPETOS
Escala 1 : 20

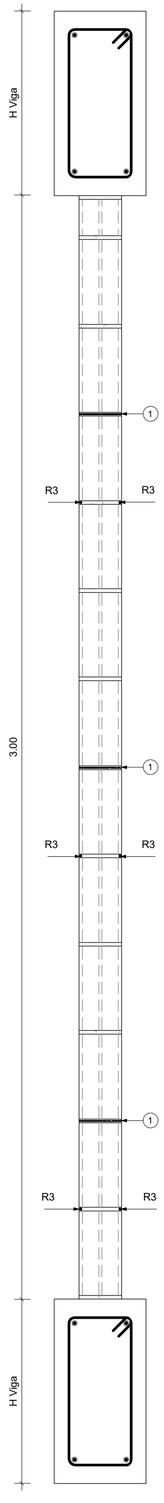

CORTE 1 - 1 - ALZADO REFUERZO EN MUROS DE MAMPOSTERÍA BLOQUE GRAN FORMATO
Escala 1 : 10

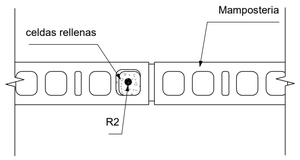

CORTE 2 - 2
Escala 1 : 10

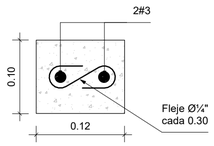

DETALLE VIGA CINTA
Escala 1 : 5

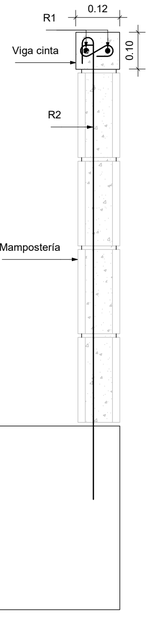

CORTE 3 - 3 SIN ENCHAPE
Escala 1 : 10

NOTAS:
- Previo a la construcción de los muros no estructurales deberá revisarse el trazado de las redes dispuestas en los muros.

Grado de desempeño:
BUENO

NOTA:
Este plano debe ser revisado y aprobado por el Constructor del proyecto.

VºBº CONSTRUCTOR:

VERSIÓN : 0

PLANO Nº 18.02

Aycardi Estructural

GERENTE DE PROYECTO
LUIS ENRIQUE AYCARDI F.
MAT. 2520212794 CND

INGENIERO
DANIEL E. QUICANO C.

MODELADOR
FELIPE SALINAS RODRÍGUEZ

MODIFICACIONES	FECHA
Emisión Inicial	21-11-2025

HUMANISE STUDIO

EAN-0519-

Calle 71 #9-84

DETALLES DE ELEMENTOS NO ESTRUCTURALES

EAN-0519-PL-5104 18.02

REVISOR ESTRUCTURAL
JULIO CESAR SANMIGUEL CAMACHO
MAT. 25202-57738 CND

PLANO Nº 18.02 VERSIÓN : 0