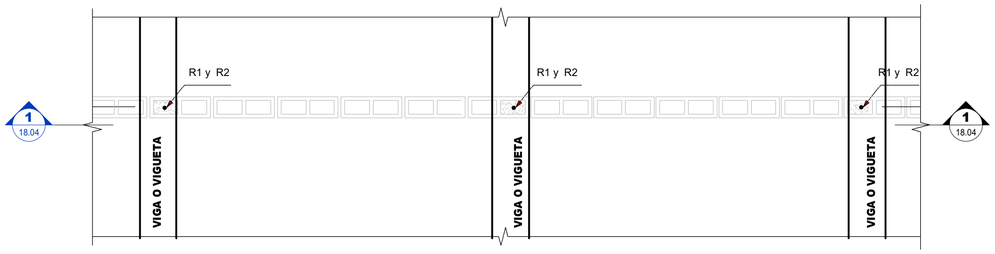

DISPOSICION TIPO 1 DE MUROS EN BLOQUE
Escala 1 : 20

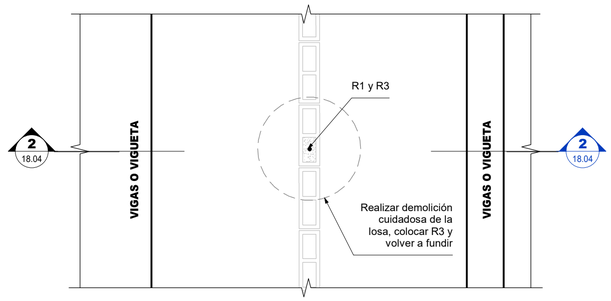

DISPOSICION TIPO 2 DE MUROS EN BLOQUE
Escala 1 : 20

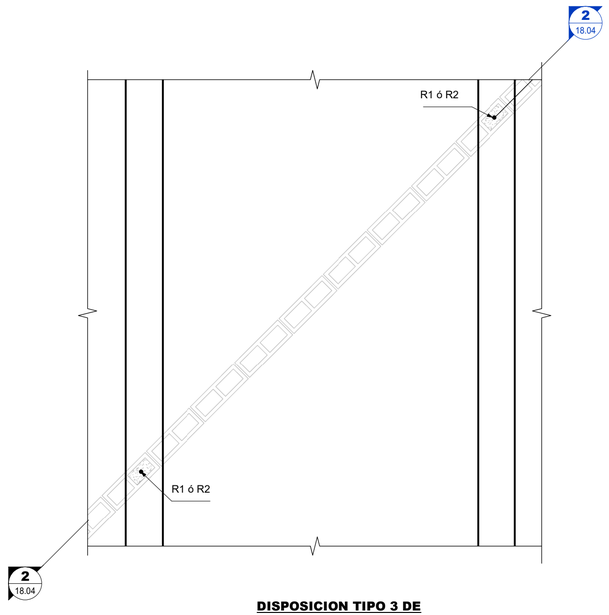

DISPOSICION TIPO 3 DE MUROS EN BLOQUE
Escala 1 : 20

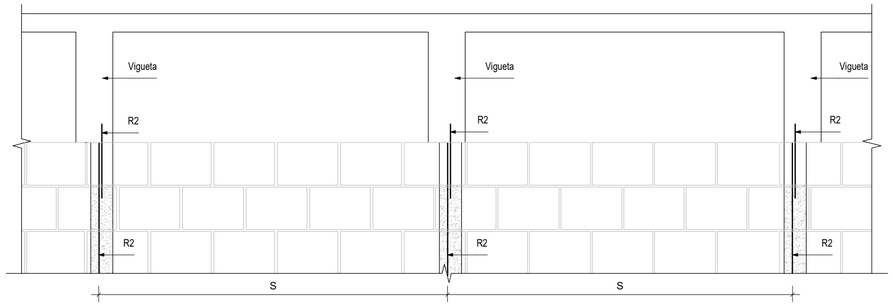

S Separación máxima entre refuerzo de 1.00m

R1 1#4 L=luz libre -0.05m

R2 1#4 L=0.40 m anclada 0.10 m con resina epóxica

CORTE 1 - 1
Escala 1 : 20

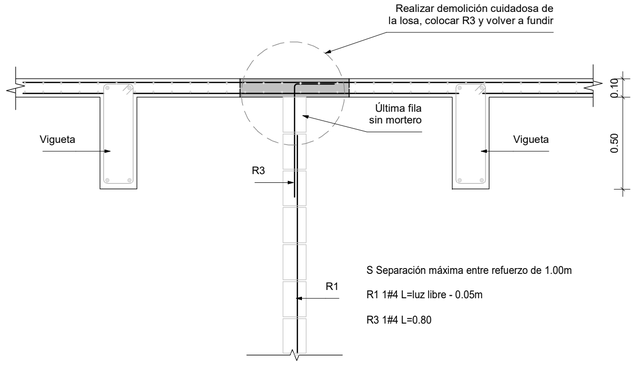

S Separación máxima entre refuerzo de 1.00m

R1 1#4 L=luz libre - 0.05m

R3 1#4 L=0.80

CORTE 2 - 2
Escala 1 : 20

Grado de desempeño:
BUENO

NOTAS:

1. Ver cuadro de especificaciones de mampostería en PL N° 18.00 y 18.01
2. Previo a la construccón de los muros no estructurales deberá revisarse el trazado de las redes dispuestas en los muros.

NOTA:
Este plano debe ser revisado y aprobado por el Constructor del proyecto.

VºBº CONSTRUCTOR:

VERSIÓN : 0

PLANO Nº 18.04

Aycardi Estructural

GERENTE DE PROYECTO
LUIS ENRIQUE AYCARDI F.
MAT. 2520212794 CND

INGENIERO
DANIEL E. QUICANO C.

MODELADOR
FELIPE SALINAS RODRÍGUEZ

MODIFICACIONES	FECHA
Emisión Inicial	21-11-2025

HUMANISE STUDIO

EAN-0519-

Calle 71 #9-84

DETALLES DE ELEMENTOS NO ESTRUCTURALES

EAN-0519-PL-5106 18.04

REVISOR ESTRUCTURAL
JULIO CESAR SANMIGUEL CAMACHO
MAT. 25202-57738 CND

PLANO N° 18.04 VERSIÓN : 0