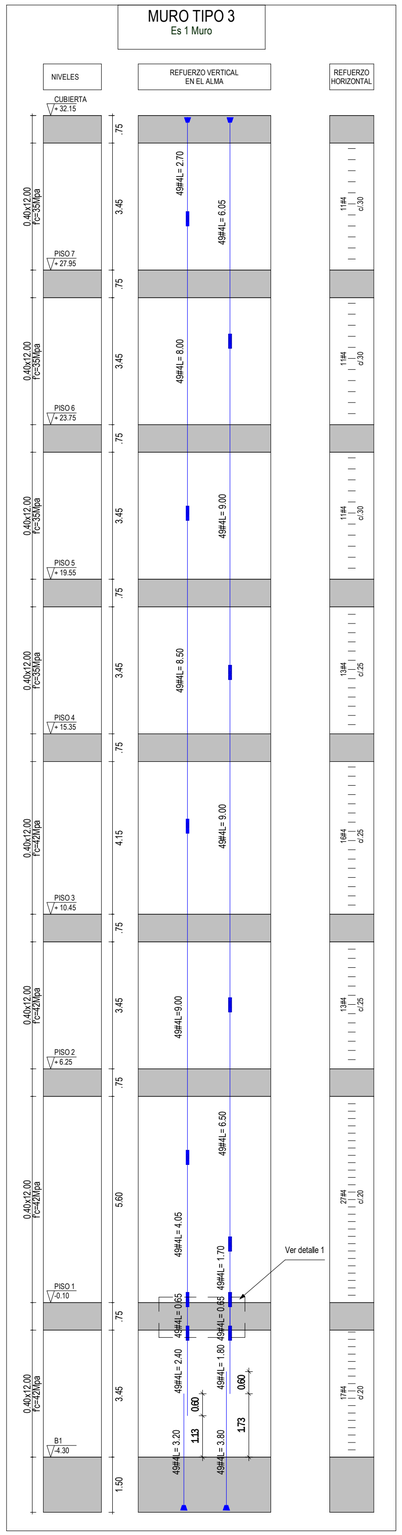

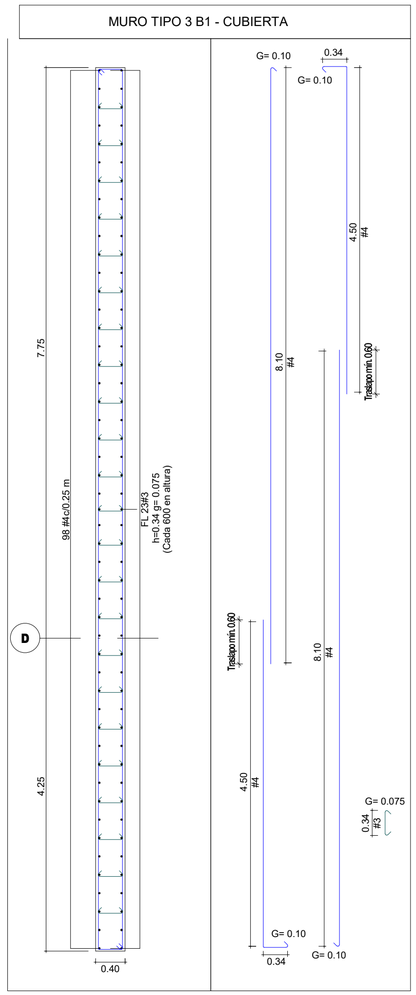

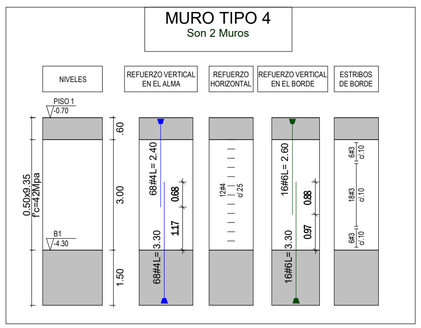

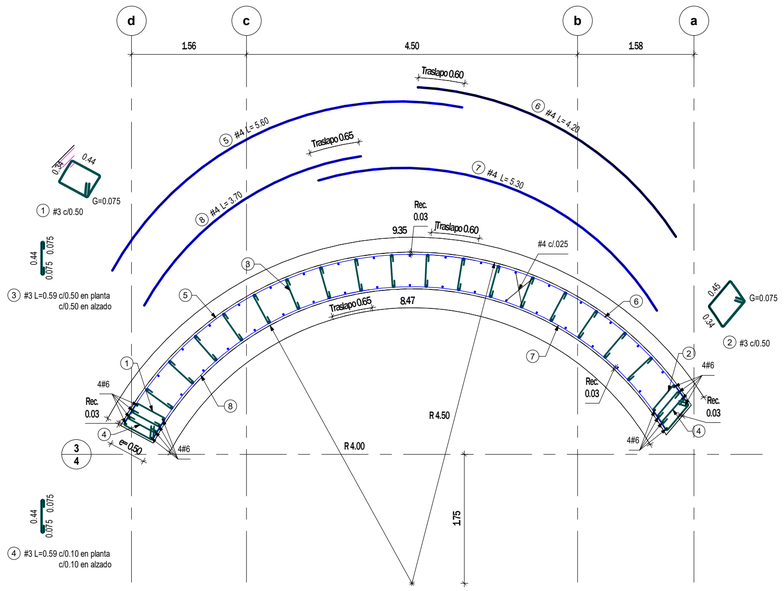

SECCIÓN MURO TIPO 4
Escala 1 : 50

CONVENCIONES

- Indica disco de anclaje
- Indica empalme mecánico

NOTAS

1. Ver detalles generales en plano PL N° 01.02 y 01.03
2. Ver planta localización e identificación de muros y columnas en PL. N° 04.00
3. Ver detalle 1 en el PL N° 04.00

VERSIÓN : 0

PLANO N° 04.07

Aycardi Estructural

GERENTE DE PROYECTO
LUIS ENRIQUE AYCARDI F.
MAT. 2520212794 CND

INGENIERO
DANIEL E. QUICANO C.

MODELADOR
PAULA ANDREA MONTOYA RENDÓN

MODIFICACIONES	FECHA
Emisión Inicial	21-11-2025

HUMANISE STUDIO

EAN-0519- AES-01-EST

Calle 71 #9-84

DESPIECE MUROS TIPO 3 Y 4

EAN-0519 -AES-01-EST-PL-514 04.07

REVISOR ESTRUCTURAL
JULIO CESAR SANMIGUEL CAMACHO
MAT. 25202-57738 CND

PLANO N° 04.07 VERSIÓN : 0