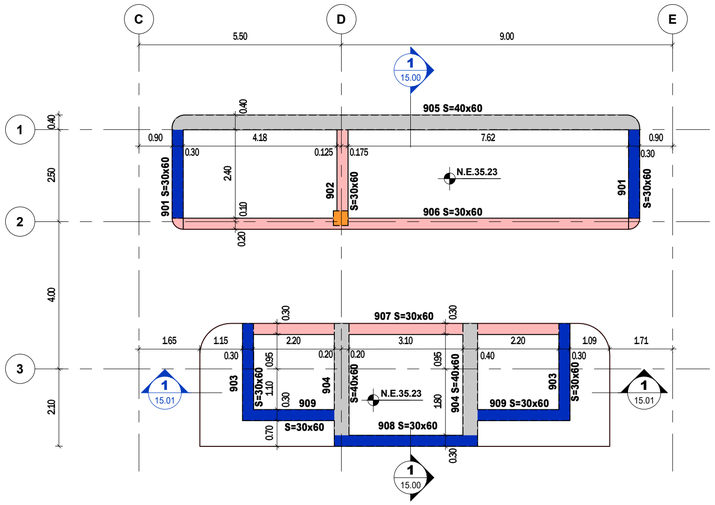

PLANTA DE CUBIERTA MÁQUINAS
Escala 1 : 100

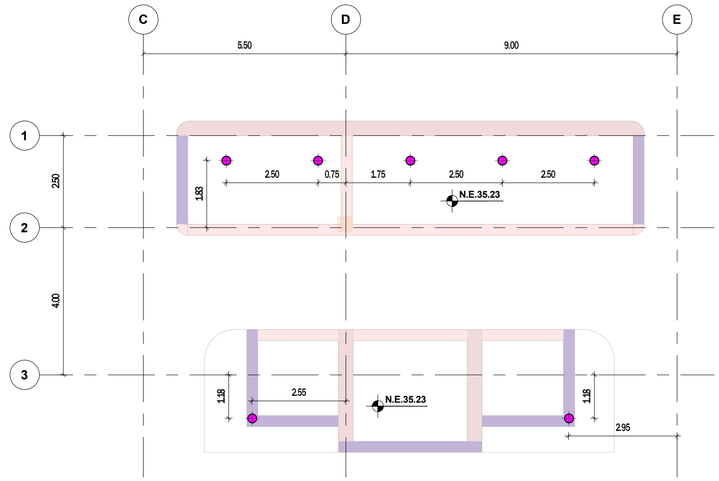

PLANTA DE LOCALIZACIÓN DE PUNTOS DE ANCLAJE Y DUCTOS DE CUBIERTA DE MÁQUINAS
Escala 1 : 100

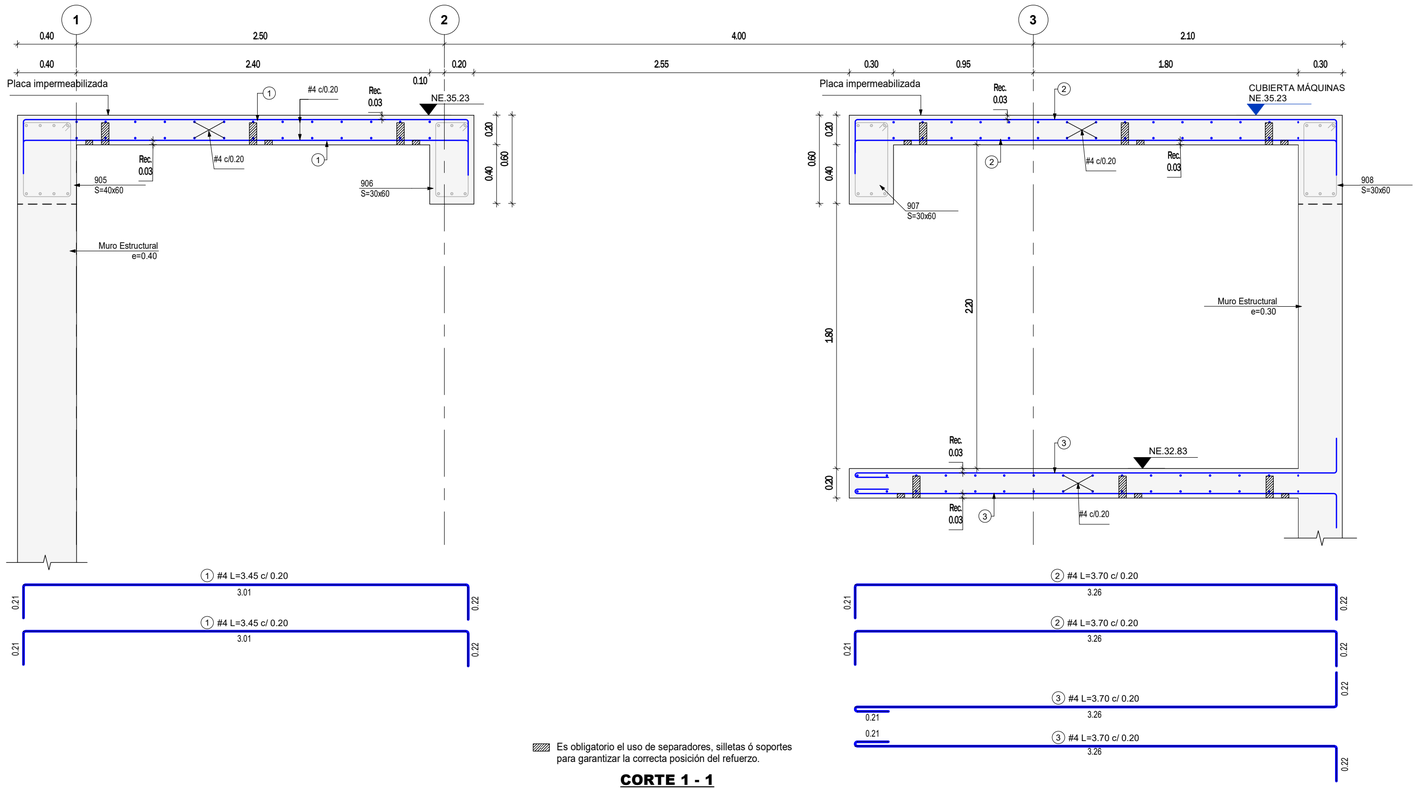

Es obligatorio el uso de separadores, silletas ó soportes para garantizar la correcta posición del refuerzo.

CORTE 1 - 1
Escala 1 : 25

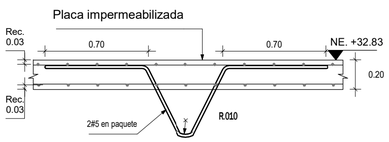

DETALLE GANCHO DE IZAJE CUBIERTA DE ASCENSOR
Escala 1 : 25

CONCRETO

f'c=35 MPa
f'c=350 kg/cm²
f'c=5000 psi

CONVENCIONES

- Indica columna que muere
- Indica muro e=30 que muere
- Indica muro e=40 que muere
- Indica viga h=60

NOTAS

1. Ver detalles generales en el PL N° 01.02 y 01.03
2. Ver corte 2 - 2 en el PL N°15.01
3. Ver despieces de vigas en los PL N° 15.02
4. Se debe garantizar un tiempo mínimo de curado intensivo de por lo menos 15 días
5. Debe estudiarse e implementar algún sistema de aislamiento térmico de la losa de concreto

VERSIÓN : 0

PLANO N° 15.00

Aycardi Estructural

GERENTE DE PROYECTO
LUIS ENRIQUE AYCARDI F.
MAT. 2520212794 CND

INGENIERO
DANIEL E. QUICANO C.

MODELADOR
PAULA ANDREA MONTOYA RENDÓN

MODIFICACIONES	FECHA
Emisión Inicial	21-11-2025

HUMANISE STUDIO

EAN-0519- AES-01-EST

Calle 71 #9-84

PLANTA DE CUBIERTA DE MÁQUINAS

EAN-0519 -AES-01-EST-SCU-PL-116 15.00

REVISOR ESTRUCTURAL
JULIO CESAR SANMIGUEL CAMACHO
MAT. 25202-57738 CND

PLANO N° 15.00 VERSIÓN : 0