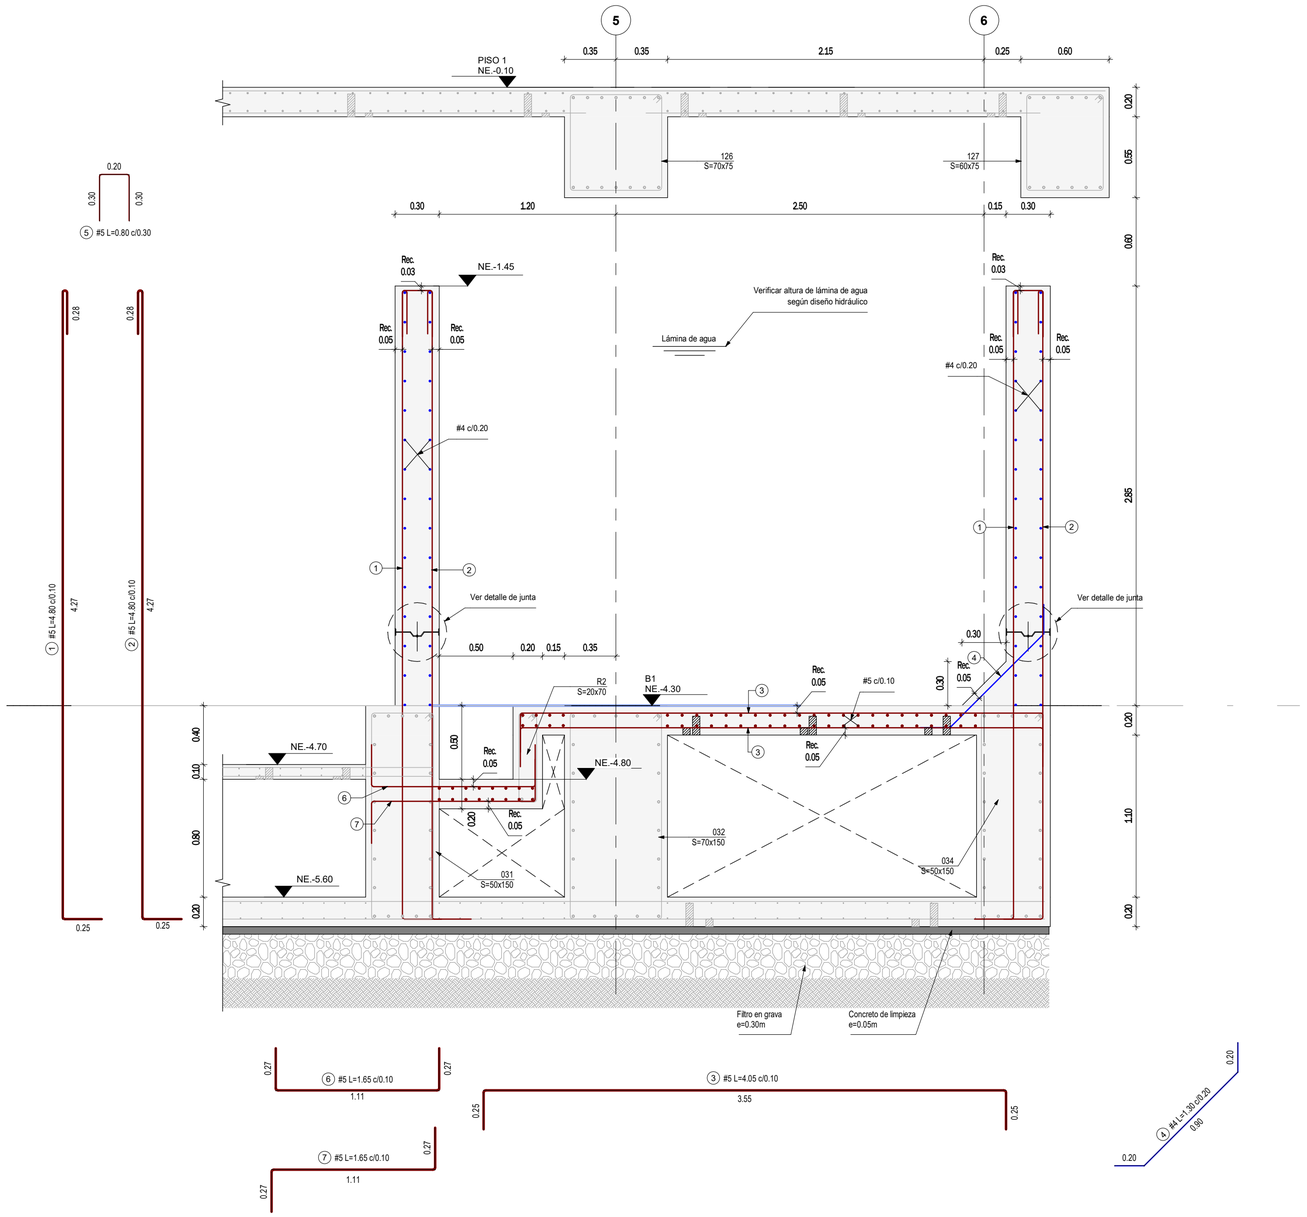

Es obligatorio el uso de separadores, silletas o soportes para garantizar la correcta posición del refuerzo.

CORTE TQ8
Escala 1 : 25

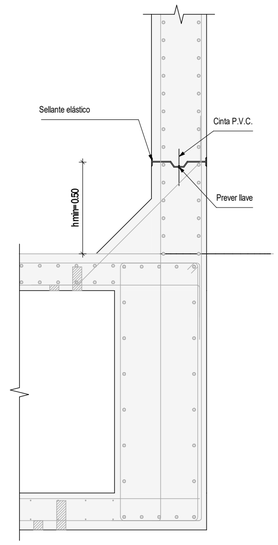

DETALLE JUNTA DE MUROS
Escala 1 : 20

NOTAS:

1. Ver detalles generales en PL. N° 01.02 y 01.03
2. Ver planta de cimentación y detalles de riostras en PL. N° 06.00.
3. Ver planta de tanque y detalle de refuerzo en esquinas de muro en PL. N° 16.05

NOTA:
El diseño del tanque deberá ser revisado por el ingeniero hidrosanitario.

V°B° DISEÑADOR HIDROSANITARIO

NOTA:
Este plano debe ser revisado y aprobado por el Ingeniero de suelos.

V°B° INGENIERO DE SUELOS

VERSIÓN : 1

PLANO N° 16.06

Aycardi Estructural

GERENTE DE PROYECTO
LUIS ENRIQUE AYCARDI F.
MAT. 2520212794 CND

INGENIERO
DANIEL E. QUICANO C.

MODELADOR
PAULA ANDREA MONTOYA RENDÓN

MODIFICACIONES	FECHA
Emisión Inicial	13-03-2026

HUMANISE

Circular Lab

HUMANISE STUDIO

EAN-0519- AES-01-EST

Calle 71 #9-84

CORTE TANQUE DE AGUA ENTRE EJES 5 Y 6

EAN-0519 -AES-01-EST-B1-PL-588 16.06

REVISOR ESTRUCTURAL
JULIO CESAR SANMIGUEL CAMACHO
MAT. 25202-57738 CND

PLANO N° 16.06 VERSIÓN : 1