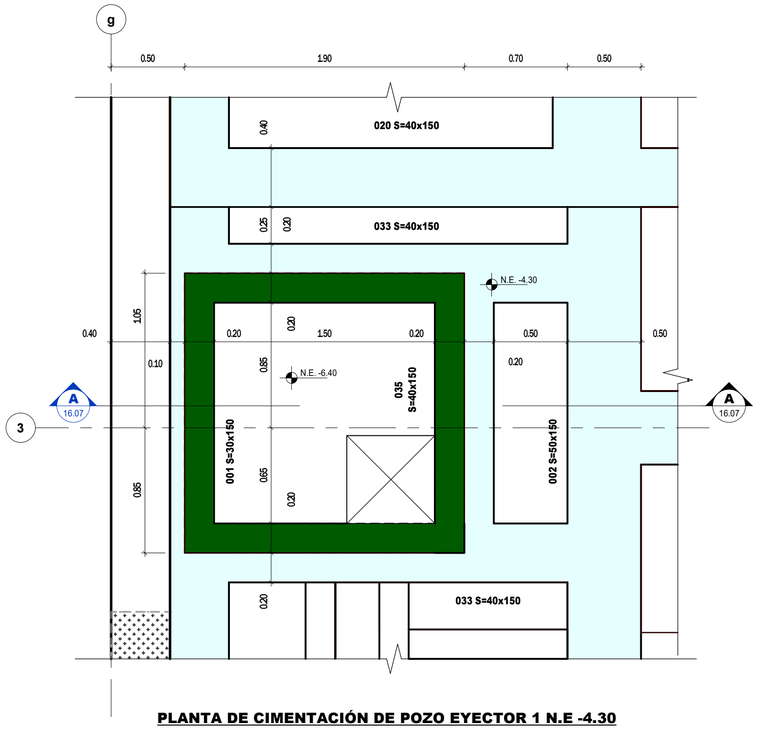

PLANTA DE CIMENTACIÓN DE POZO EYECTOR 1 N.E -4.30
Escala 1 : 25

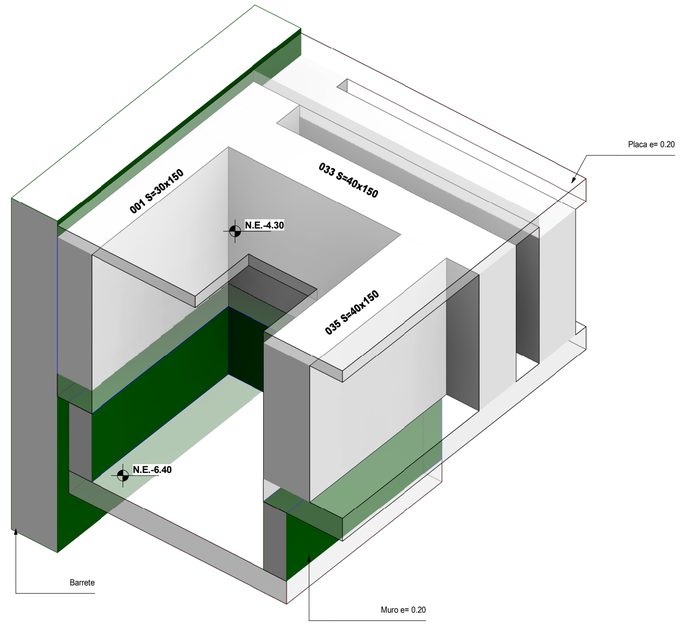

ESQUEMA 3D POZO EYECTOR 1
Sin escala

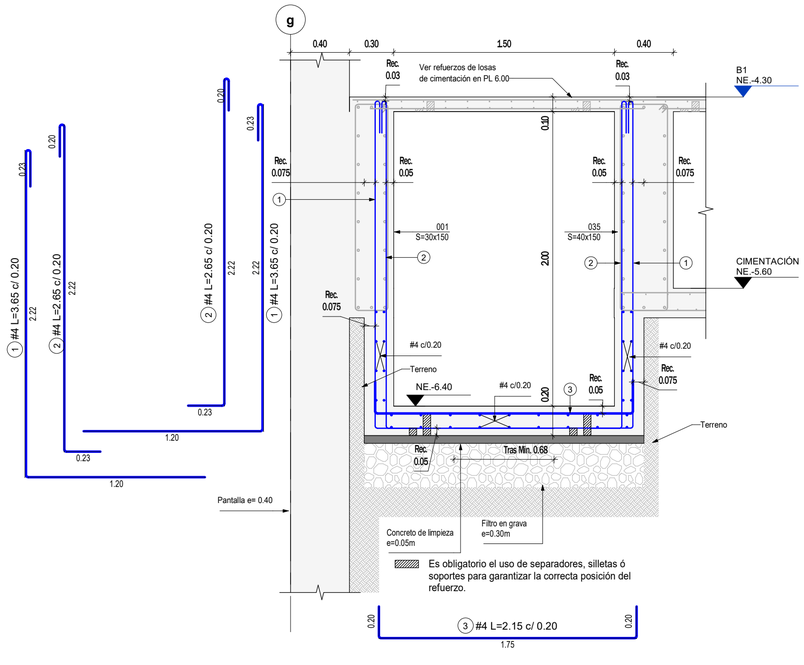

CORTE A-A
Escala 1 : 25

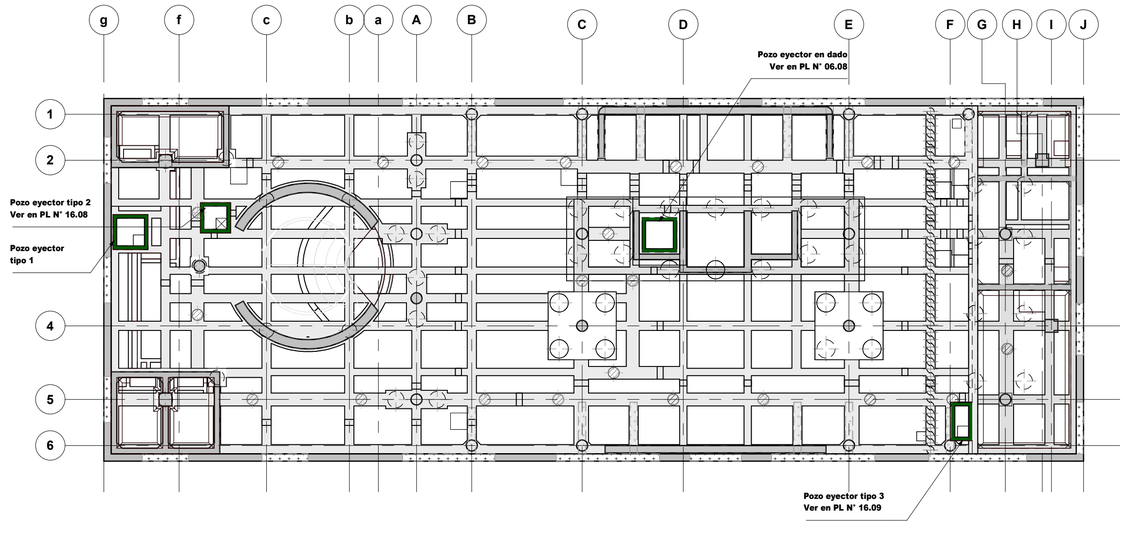

PLANTA DE LOCALIZACIÓN DE POZOS EYECTORES
Escala 1 : 200

CONCRETO

f'c=28 MPa
f'c=280 kg/cm²
f'c=4000 psi

CONVENCIONES

Indica muro e=20

Indica viga H=150

NOTAS

1. Ver detalles generales en el PL. 01.02 PL. 01.03
2. Ver planos de cimentación en PL. N° 06.00,PL. N° 06.01,PL. N° 06.02.

VERSIÓN : 1

PLANO N° 16.07

Aycardi Estructural

GERENTE DE PROYECTO
LUIS ENRIQUE AYCARDI F.
MAT. 2520212794 CND

INGENIERO
DANIEL E. QUICANO C.

MODELADOR
JUAN MANUEL SANTOS

MODIFICACIONES	FECHA
Emisión Inicial	13-03-2026

HUMANISE STUDIO

EAN-0519- AES-01-TQ

Calle 71 #9-84

POZO EYECTOR TIPO 1

EAN-0519 -AES-01-TQ-B1-PL-589 16.07

REVISOR ESTRUCTURAL
JULIO CESAR SANMIGUEL CAMACHO
MAT. 25202-57738 CND

PLANO N° 16.07 VERSIÓN : 1