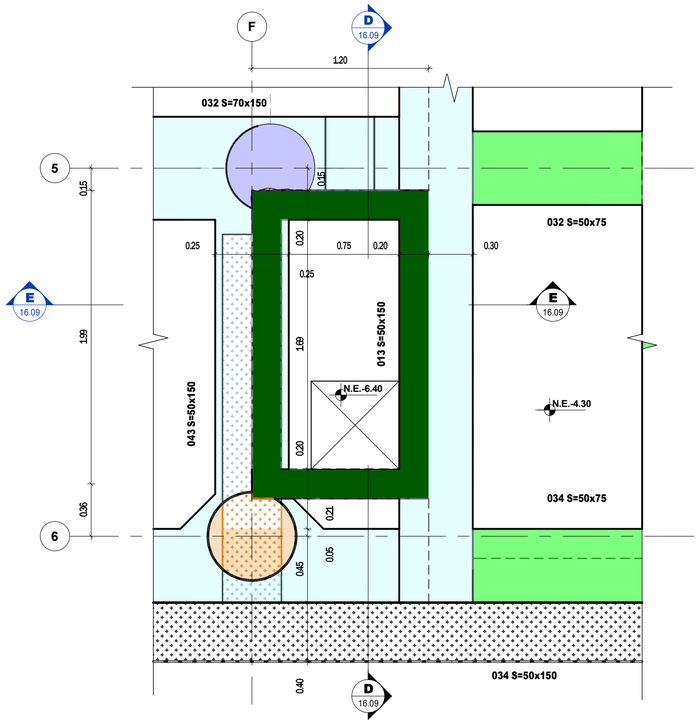

PLANTA DE CIMENTACIÓN DE POZO EYECTOR 3 N.E -4.30
Escala 1 : 25

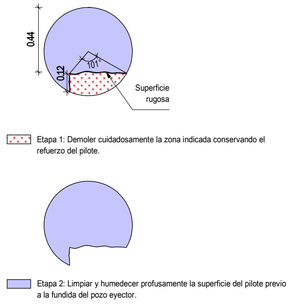

DETALLE DE DEMOLICIÓN DE PILOTE CONSTRUCTIVO
Escala 1 : 25

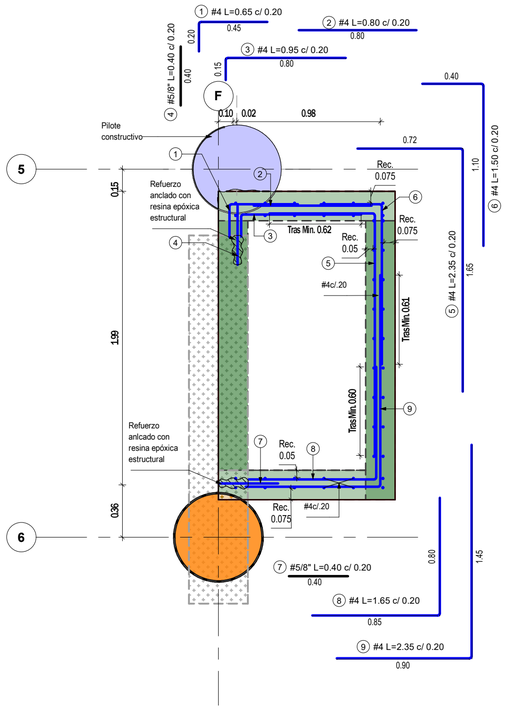

PLANTA DE REFUERZO DE POZO EYECTOR 3 N.E -4.30
Escala 1 : 25

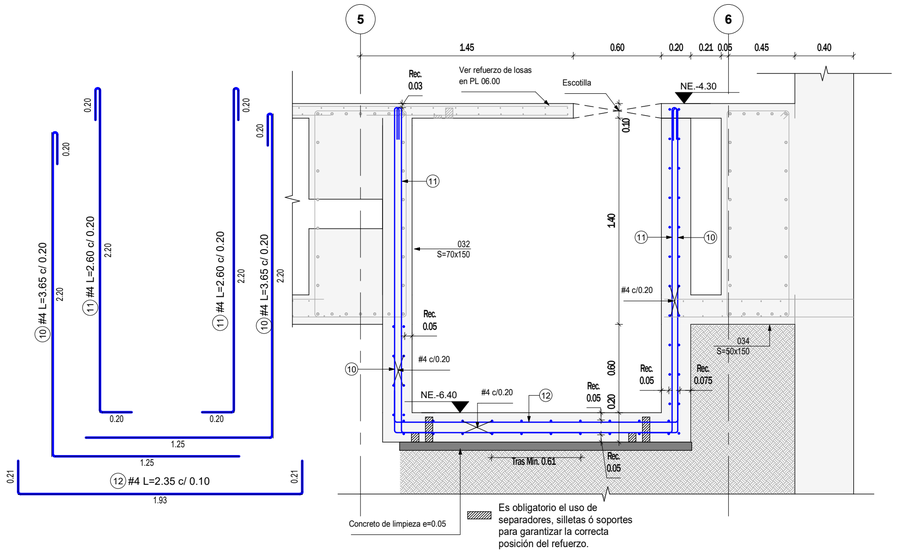

CORTE D-D
Escala 1 : 25

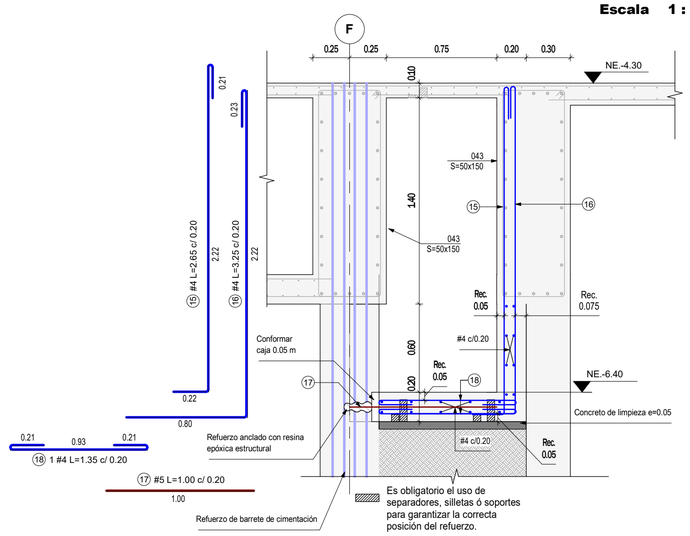

CORTE E-E
Escala 1 : 25

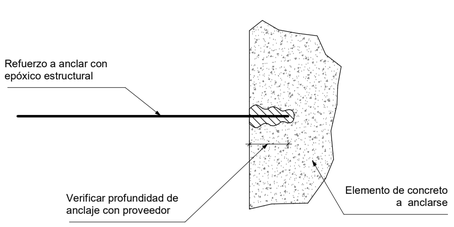

CONVENCIÓN REFUERZO ANCLADO CON EPÓXICO
Sin escala

- **Realizar anclajes con epóxico estructural instalado según ESR 2322**
- **Perforación con taladro a percusión, empleando un pistón de inyección**

CONCRETO

f'c=28 MPa
f'c=280 kg/cm²
f'c=4000 psi

CONVENCIONES

- Indica Columna
- Indica pilote constructivo
- Indica muro e=20
- Indica muro e=50
- Indica viga H=150
- Indica barrete

NOTAS

1. Ver detalles generales en el PL. 01.02 y PL. 01.03
2. Ver planos de cimentación en PL. N° 06.00,PL. N° 06.01,PL. N° 06.02.
3. Ver planta de localización de pozos eyectores en PL N° 16.07.

VERSIÓN : 1

PLANO N° 16.09

Aycardi Estructural

GERENTE DE PROYECTO
LUIS ENRIQUE AYCARDI F.
MAT. 2520212794 CND

INGENIERO
DANIEL E. QUICANO C.

MODELADOR
JUAN MANUEL SANTOS

MODIFICACIONES	FECHA
Emisión Inicial	13-03-2026

HUMANISE

Circular Lab

HUMANISE STUDIO

EAN-0519- AES-01-TQ

Calle 71 #9-84

POZO EYECTOR TIPO 3

EAN-0519 -AES-01-TQ-B1-PL-591 16.09

REVISOR ESTRUCTURAL
JULIO CESAR SANMIGUEL CAMACHO
MAT. 25202-57738 CND

PLANO N° 16.09 VERSIÓN : 1