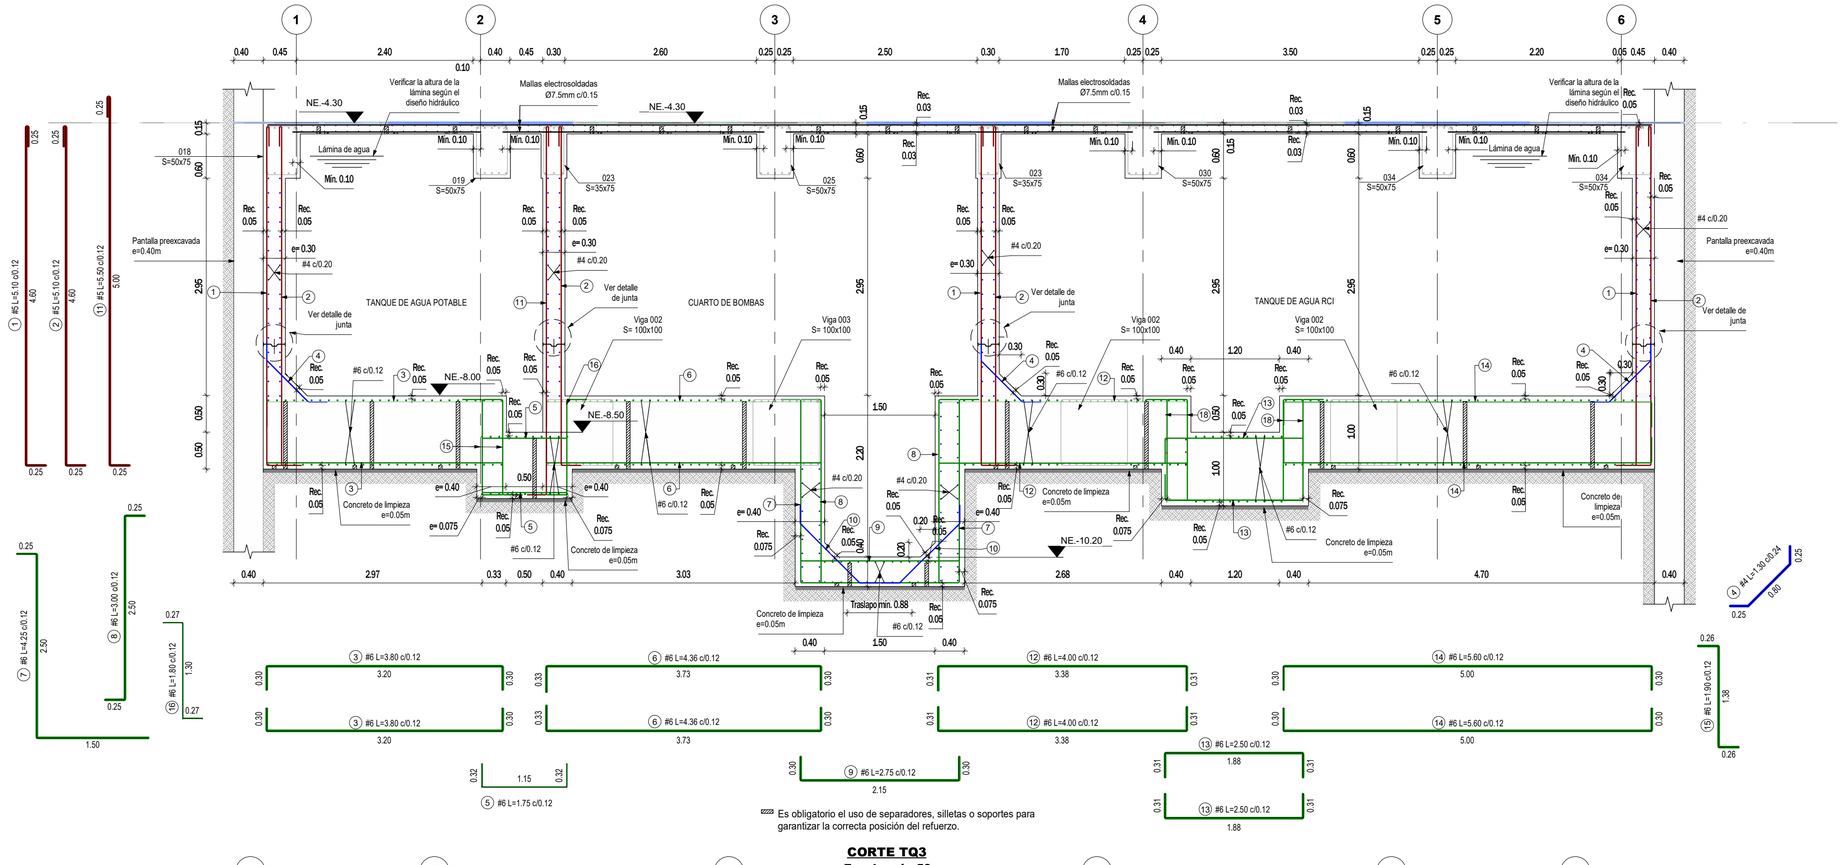

Es obligatorio el uso de separadores, silletas o soportes para garantizar la correcta posición del refuerzo.

CORTE TQ3
Escala 1 : 50

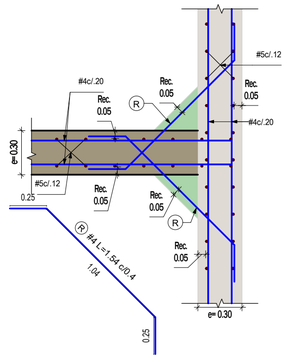

DETALLE UNIÓN MURO TANQUE EN PLANTA
Escala 1 : 25

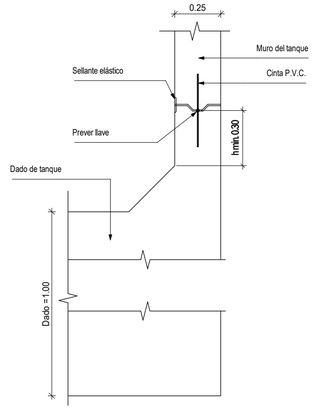

DETALLE DE JUNTA
Escala 1 : 20

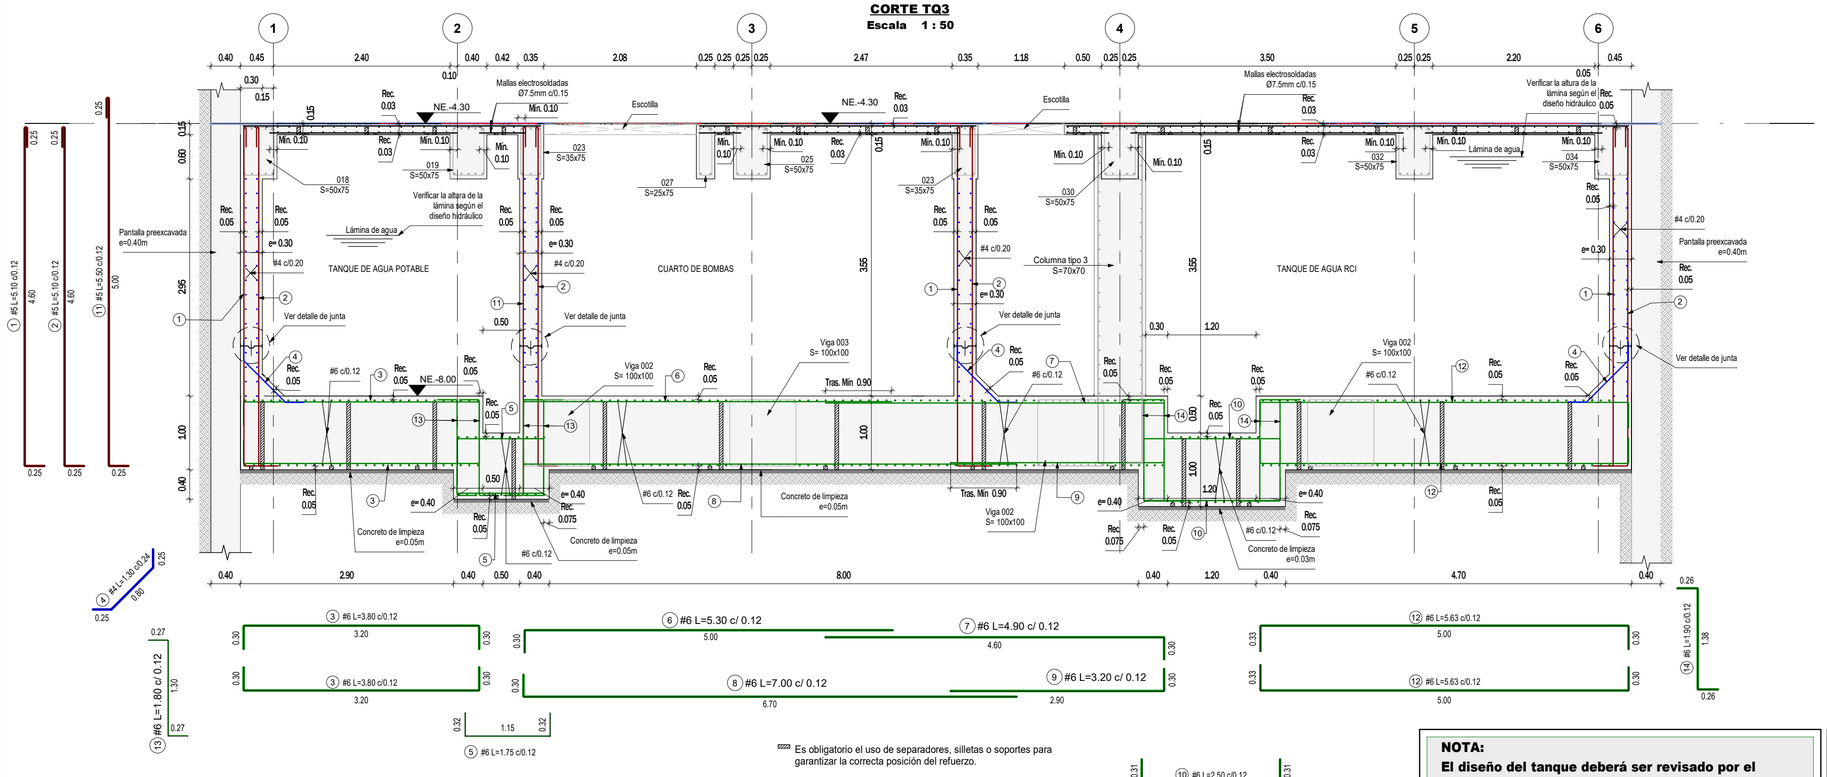

Es obligatorio el uso de separadores, silletas o soportes para garantizar la correcta posición del refuerzo.

CORTE TQ4
Escala 1 : 50

NOTAS
1. Ver detalles generales en el PL. N° 01.02 y PL. N° 01.03
2. Ver planta de localización de pilotes plano PL. N°02.00
3. Ver secuencia constructiva en PL° 03.00 a PL° 03.11
4. Ver planta de tanque en PL N°16.00
5. Ver despieces de vigas de tanque en PL N°16.02

NOTA:
El diseño del tanque deberá ser revisado por el ingeniero hidrosanitario.

V°B° DISEÑADOR HIDROSANITARIO

NOTA:
Este plano debe ser revisado y aprobado por el Ingeniero de suelos.

V°B° INGENIERO DE SUELOS

VERSIÓN : 1

PLANO N° 16.01

Aycardi Estructural

GERENTE DE PROYECTO
LUIS ENRIQUE AYCARDI F.
MAT. 2520212794 CND

INGENIERO
DANIEL E. QUICANO C.

MODELADOR
JUAN MANUEL SANTOS

MODIFICACIONES	FECHA
Emisión Inicial	13-03-2026

HUMANISE

Circular Lab

HUMANISE STUDIO

EAN-0519- AES-01-EST

Calle 71 #9-84

CORTES TANQUE DE AGUA

EAN-0519 -AES-01-EST-B2-PL-583 16.01

REVISOR ESTRUCTURAL
JULIO CESAR SANMIGUEL CAMACHO
MAT. 25202-57738 CND

PLANO N° 16.01 VERSIÓN : 1