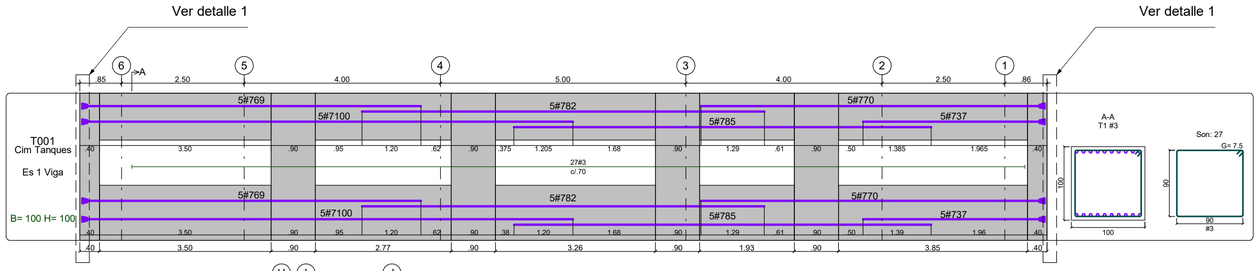

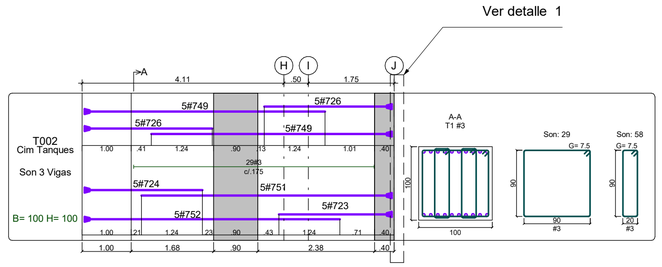

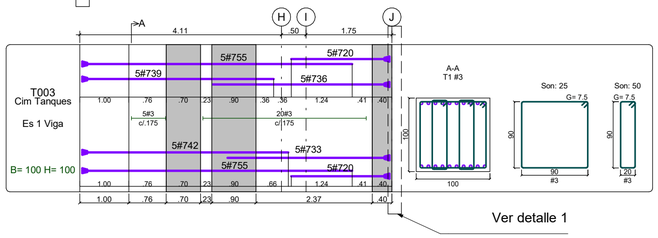

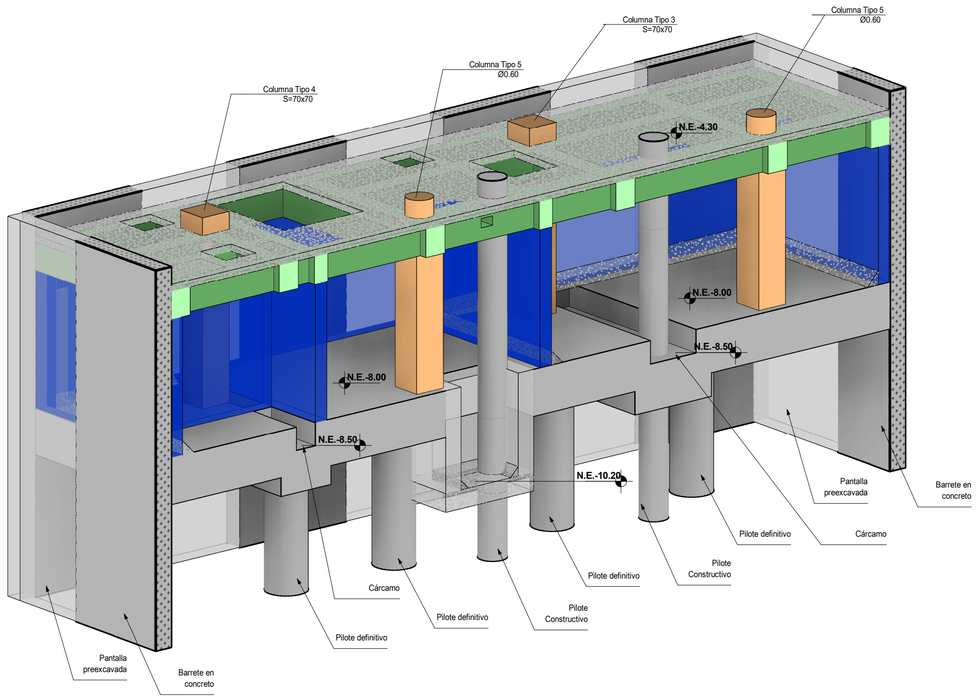

ESQUEMA 3D TANQUE
Sin escala

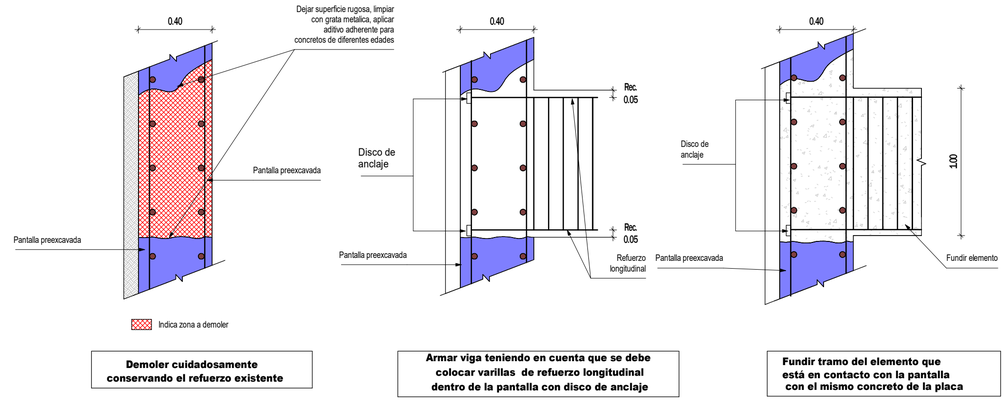

DETALLE 1 - VINCULACIÓN VIGAS DE CIMENTACIÓN PERPENDICULARES A LA PANTALLA PRE-EXCAVADA CON DISCO DE ANCLAJE
Escala 1 : 25

CONCRETO	
CONCRETO DE DADO	CONCRETO DE MUROS
f'c=35 MPa	**f'c=28 MPa**
f'c=350 kg/cm²	**f'c=280 kg/cm²**
f'c=5000 psi	**f'c=4000 psi**

NOTAS

1. Ver detalles generales en el PL. N° 01.02 y PL. N° 01.03
2. Ver refuerzo lateral para vigas altas en PL. N° 01.02
3. Ver planta de ciemntación de agua en el PL. N° 06.00

VERSIÓN : 1

PLANO N° 16.02

Aycardi Estructural

GERENTE DE PROYECTO
LUIS ENRIQUE AYCARDI F.
MAT. 2520212794 CND

INGENIERO
DANIEL E. QUICANO C.

MODELADOR
PAULA ANDREA MONTOYA RENDÓN

MODIFICACIONES	FECHA
Emisión Inicial	13-03-2026

HUMANISE

Circular Lab

HUMANISE STUDIO

EAN-0519- AES-01-EST

Calle 71 #9-84

DESPIECES VIGAS DE CIMENTACIÓN TANQUE DE AGUA

EAN-0519 -AES-01-EST-B2-PL-584 16.02

REVISOR ESTRUCTURAL
JULIO CESAR SANMIGUEL CAMACHO
MAT. 25202-57738 CND

PLANO N° 16.02 VERSIÓN : 1