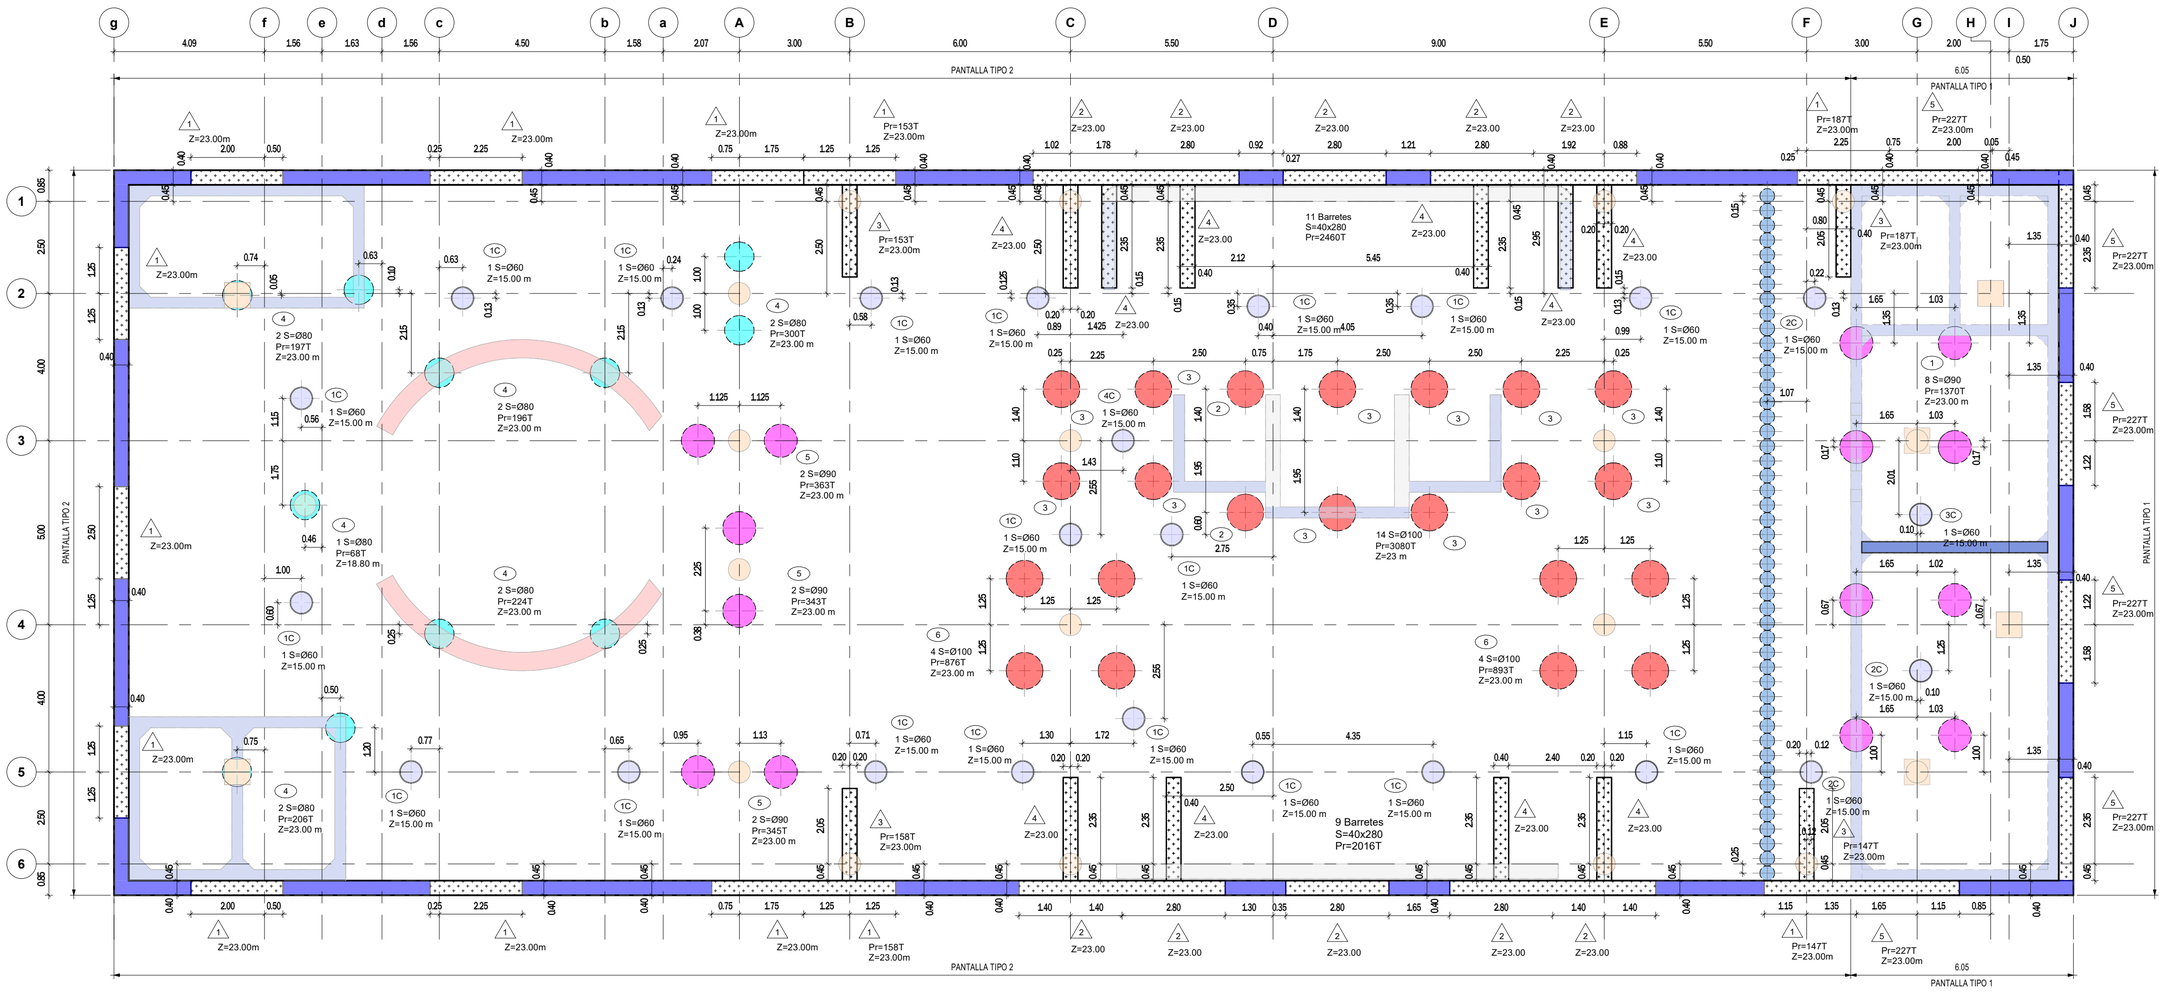

PLANTA DE LOCALIZACIÓN DE PILOTES, PANTALLAS Y BARRETES

Escala 1 : 100

CONCRETO

f'c=28 MPa
f'c=280 kg/cm²
f'c=4000 psi

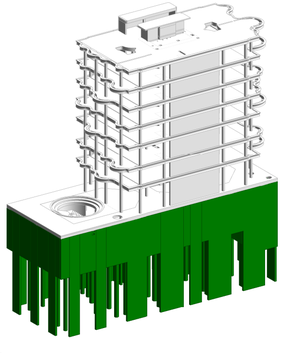

LOCALIZACIÓN DE PILOTES, PANTALLAS Y BARRETES EN 3D

Escala

NOTA:
La longitud ó profundidad del pilote deberá ser revisada y aprobada en obra por el Ingeniero de Suelos para garantizar que la capacidad del elemento sea la establecida en el estudio de suelos.

V°B° INGENIERO DE SUELOS

CONVENCIONES

- # Indica tipo de pilotes
- Pr= Indica carga real en toneladas
- Z= Indica profundidad del pilote medida desde el nivel actualdel terreno
- Indica pilotes S=Ø80
- Indica pilotes S=Ø90
- Indica pilotes S=Ø100
- Indica pilotes tangentes
- Indica pilotes constructivos
- Indica barretes
- Indica pantalla preexcavada
- Indica columna
- Indica muro e=30
- Indica muro e=40
- Indica muro e=50

NOTAS

1. Ver detalles generales en PL N° 01.02 y 01.03
2. Ver detalles de pantallas en PL N° 02.01
3. Ver detalles de barretes en PL N° 02.04 y 02.05
4. Ver detalles de pilotes en PL N° 02.02
5. Ver detalles de pilotes constructivos en PL N° 02.03

VERSIÓN : 1

PLANO N° 02.00

Aycardi Estructural

GERENTE DE PROYECTO
LUIS ENRIQUE AYCARDI F.
MAT. 2520212794 CND

INGENIERO
DANIEL E. QUICANO C.

MODELADOR
PAULA ANDREA MONTOYA RENDÓN

MODIFICACIONES	FECHA
Emisión Inicial	13-03-2026

HUMANISE

Circular Lab

HUMANISE STUDIO

EAN-0519- AES-01-EST

Calle 71 #9-84

PLANTA LOCALIZACIÓN DE PILOTES, PANTALLAS Y BARRETES

EAN-0519 -AES-01-EST-CIM-PL-101 02.00

REVISOR ESTRUCTURAL
JULIO CESAR SANMIGUEL CAMACHO
MAT. 25202-57738 CND

PLANO N° 02.00 VERSIÓN : 1