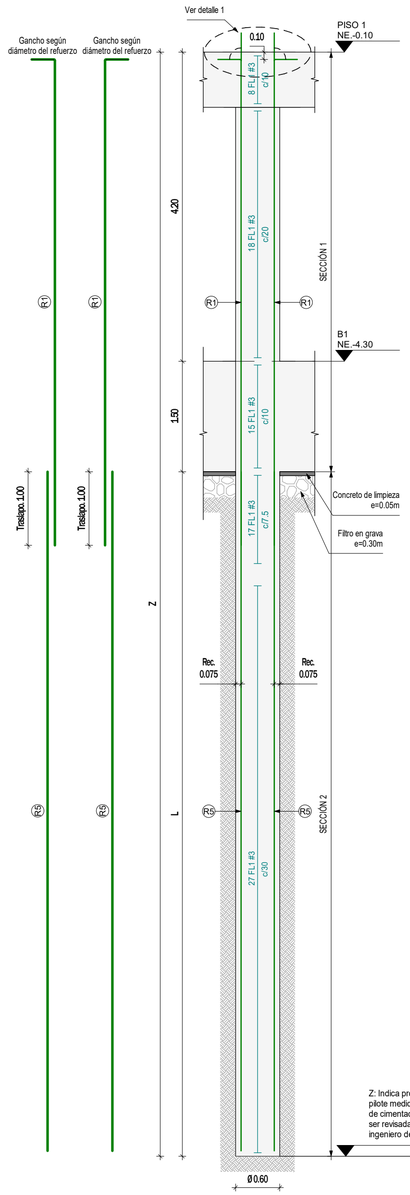

DESPIECE PILOTE CONSTRUCTIVO TIPO 1C

Escala 1 : 50

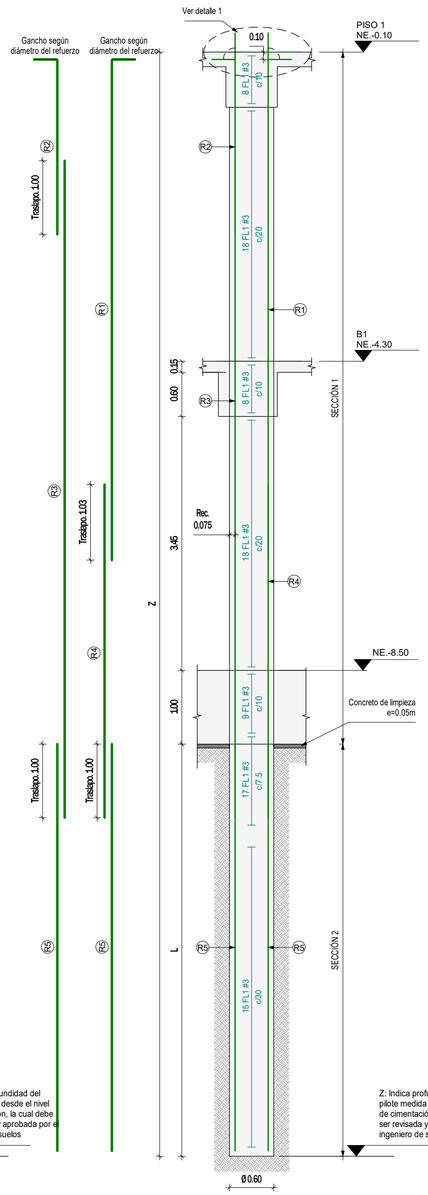

DESPIECE PILOTE CONSTRUCTIVO TIPO 2C

Escala 1 : 50

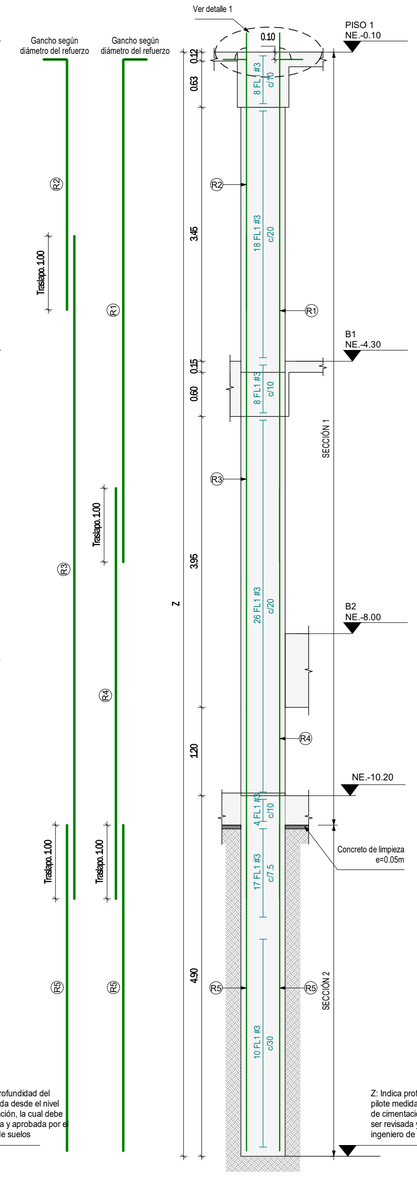

DESPIECE PILOTE CONSTRUCTIVO TIPO 3C

Escala 1 : 50

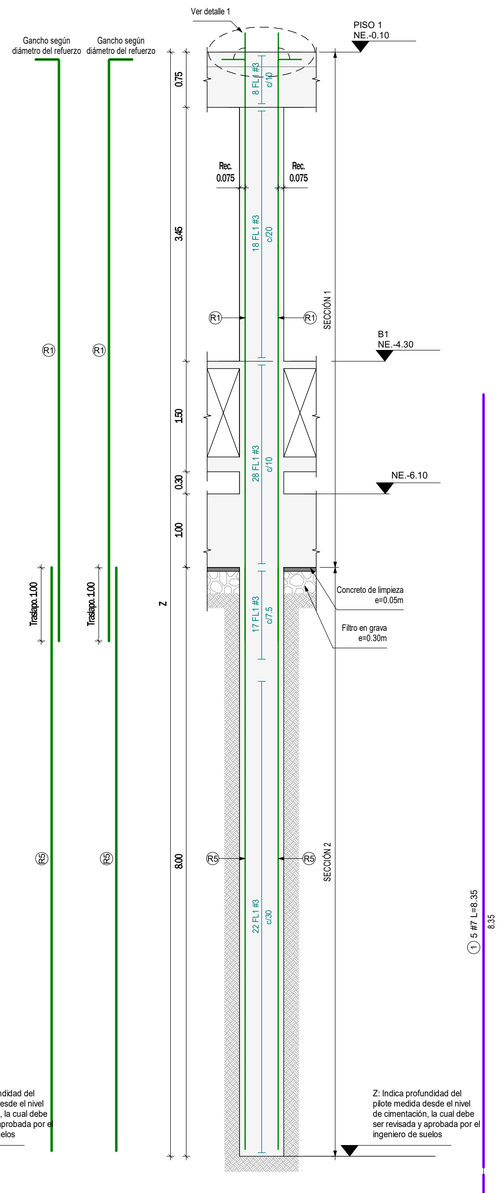

DESPIECE PILOTE CONSTRUCTIVO TIPO 4C

Escala 1 : 50

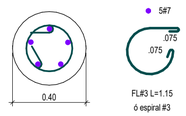

SECCIÓN PILOTE TANGENTE Ø0.40

Escala 1 : 20

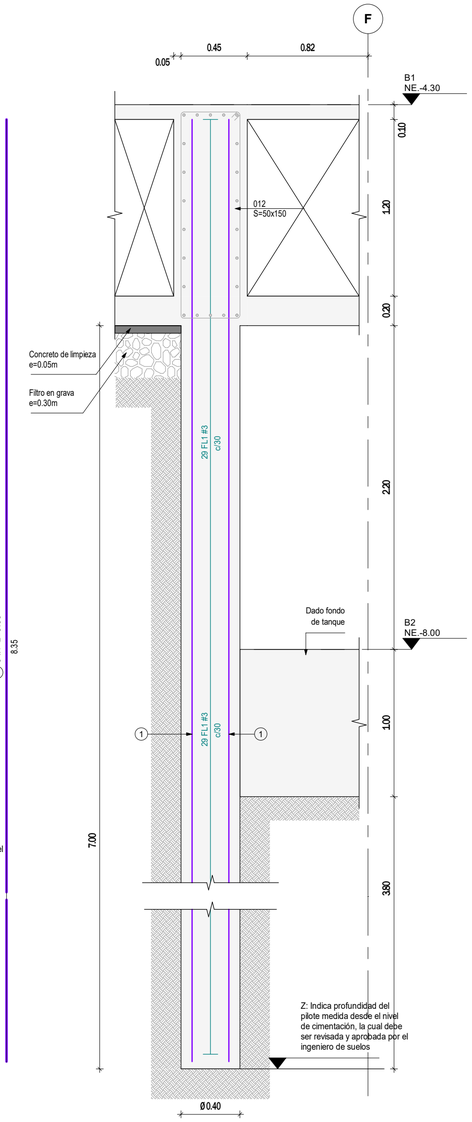

DESPIECE PILOTE TANGENTE

Escala 1 : 25

CUADRO RESUMEN DE REFUERZO DE PILOTES CONSTRUCTIVOS

Tipo Pilote		UNID	Refuerzo Longitudinal columna Sección 1														Refuerzo Longitudinal pilote Sección 2						Refuerzo Transversal									RESUMEN		
			Z [m]	L [m]	Cant	Barra	R1	Cant	Barra	R2	Cant	Barra	R3	Cant	Barra	R4	Cant	Barra	R5	Cant	Barra	R6	Zona Pilote sección 1			Zona Pilote sección 2				Zona Pilote sección 2			V_C (m^3)	W_{RL} (kg)	W_{RT} (kg)
1C	Ø0.6m	19	15.0	9.3	10	# 6	6.9										5	# 6	9.2				41	# 3		L= 1.90 m	17	# 3	c/ 0.075	L= 1.90 m	27	# 3	c/ 0.300	L= 1.90 m	80.6	4916	1718
2C	Ø0.6m	3	15.0	5.6	5	# 6	7.1	5	# 6	2.7	5	# 6	9	5	# 6	4.6	5	# 6	5.6				61	# 3		L= 1.90 m	17	# 3	c/ 0.075	L= 1.90 m	15	# 3	c/ 0.300	L= 1.90 m	12.7	979	297
3C	Ø0.6m	1	15.0	4.5	5	# 6	7.1	5	# 6	3.7	5	# 6	9	5	# 6	5.6	5	# 6	4.5				64	# 3		L= 1.90 m	17	# 3	c/ 0.075	L= 1.90 m	10	# 3	c/ 0.300	L= 1.90 m	4.2	336	97
4C	Ø0.6m	1	15.0	8.0	10	# 6	8.2										5	# 6	7.9				54	# 3		L= 1.90 m	17	# 3	c/ 0.075	L= 1.90 m	22	# 3	c/ 0.300	L= 1.90 m	4.2	273	99
Total		*24*																															***101.8***	***6505***	***2211***

V_C: Volúmen de concreto pilotes Se calcula con la longitud "Z" que se indica en el corte típico.

W_{RL}: Peso Refuerzo Longitudinal

W_{RT}: Peso Refuerzo Transversal

NOTA: Éstas cantidades no incluyen desperdicios

CUADRO RESUMEN DE REFUERZO DE PILOTES TANGENTES

Tipo Pilote		UNID	Refuerzo Longitudinal							Refuerzo Transversal							RESUMEN		
			Z [m]	L (m)	Cant	Barra	R1 (m)	R2 (m)	R3 (m)	Tramo F1				Tramo F2			V_C (m^3)	W_{RL} (kg)	W_{RT} (kg)
1	Ø 0.4 m	47	8.5	7.00	5	# 7	8.4			29	# 3	c/ 0.300	L= 1.15 m				41.3	6009	882
Total		*47*															***41.3***	***6009***	***882***

V_C: Volúmen de concreto pilotes Se calcula con la longitud "L" que se indica en el corte típico.

W_{RL}: Peso Refuerzo Longitudinal

W_{RT}: Peso Refuerzo Transversal

NOTA: Éstas cantidades no incluyen desperdicios

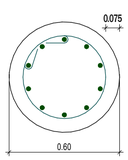

SECCIÓN 1 PILOTE CONSTRUCTIVO Ø0.60

Escala 1 : 20

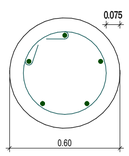

SECCIÓN 2 PILOTE CONSTRUCTIVO Ø0.60

Escala 1 : 20

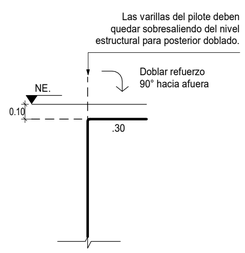

DETALLE 1

Escala 1 : 25

CONCRETO

f'c=28 MPa
f'c=280 kg/cm²
f'c=4000 psi

NOTAS

1. Ver detalles generales en PL N° 01.02 y 01.03
2. Ver planta de localización de pilotes, pantallas y barretes en PL N° 02.00

NOTA:
La longitud ó profundidad del pilote deberá ser revisada y aprobada en obra por el Ingeniero de Suelos para garantizar que la capacidad del elemento sea la establecida en el estudio de suelos.

VºBº INGENIERO DE SUELOS

VERSIÓN : 1

PLANO Nº 02.03

Aycardi Estructural

GERENTE DE PROYECTO
LUIS ENRIQUE AYCARDI F.
MAT. 2520212794 CND

INGENIERO
DANIEL E. QUICANO C.

MODELADOR
PAULA ANDREA MONTOYA RENDÓN

MODIFICACIONES	FECHA
Emisión Inicial	13-03-2026

HUMANISE

Circular Lab

HUMANISE STUDIO

EAN-0519- AES-01-EST

Calle 71 #9-84

DESPIECE DE PILOTES CONSTRUCTIVOS

EAN-0519 -AES-01-EST-CIM-PL-505 02.03

REVISOR ESTRUCTURAL
JULIO CESAR SANMIGUEL CAMACHO
MAT. 25202-57738 CND

PLANO Nº 02.03 VERSIÓN : 1