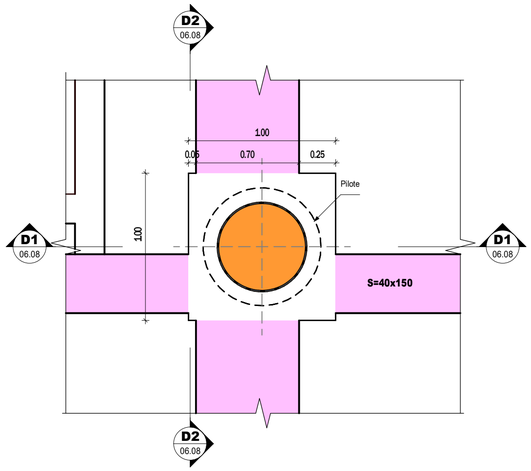

PLANTA DADO TIPO 1 Son 8 und.
Escala 1 : 25

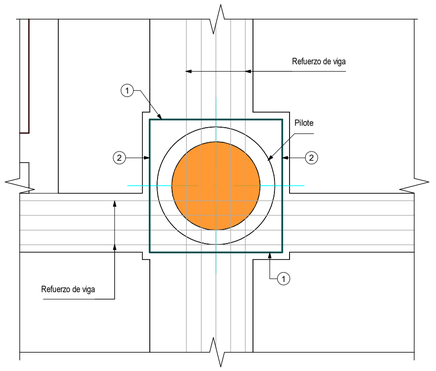

PLANTA DE REFUERZO SUPERIOR E INFERIOR DADO TIPO 1
Escala 1 : 25

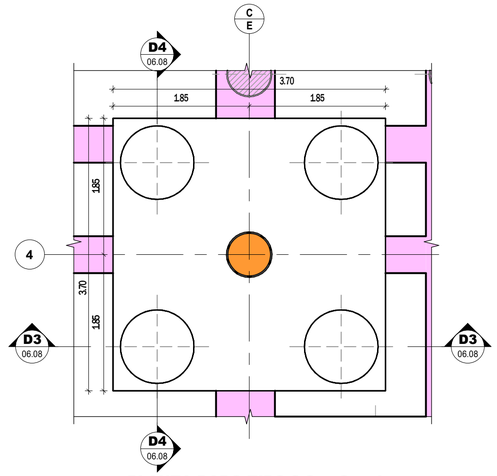

PLANTA DADO TIPO 2 Son 2 und.
Escala 1 : 50

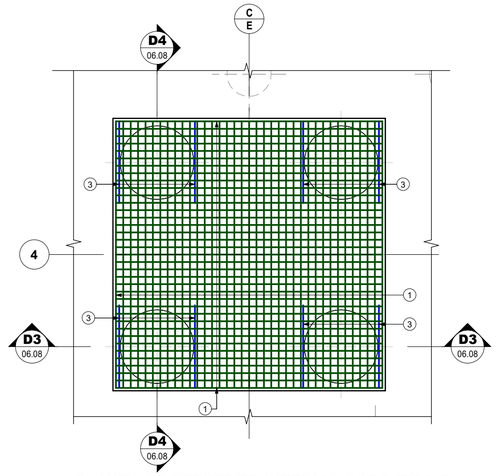

PLANTA DE REFUERZO INFERIOR DADO TIPO 2
Escala 1 : 50

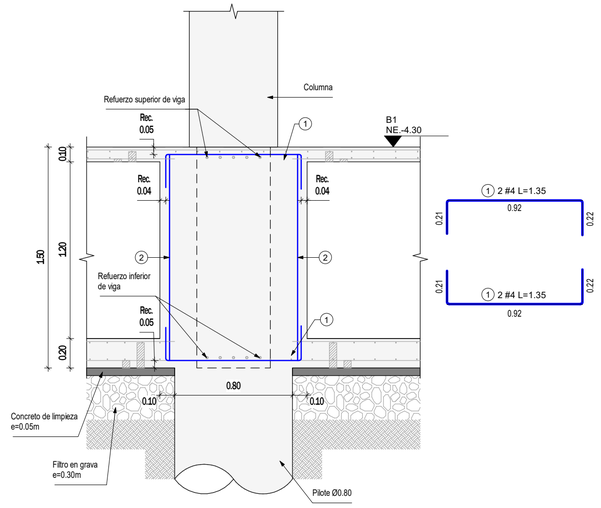

CORTE D1 - D1
Escala 1 : 25

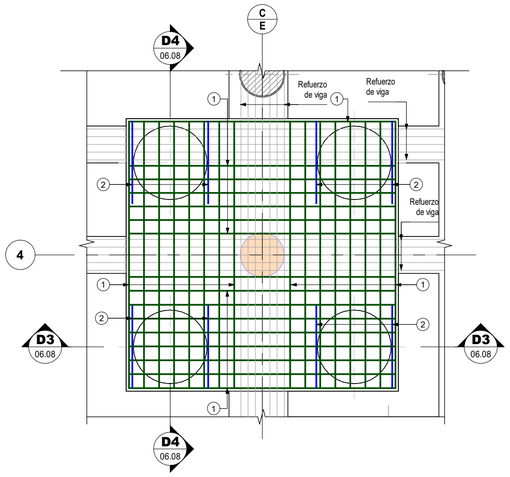

PLANTA DE REFUERZO SUPERIOR DADO TIPO 2
Escala 1 : 50

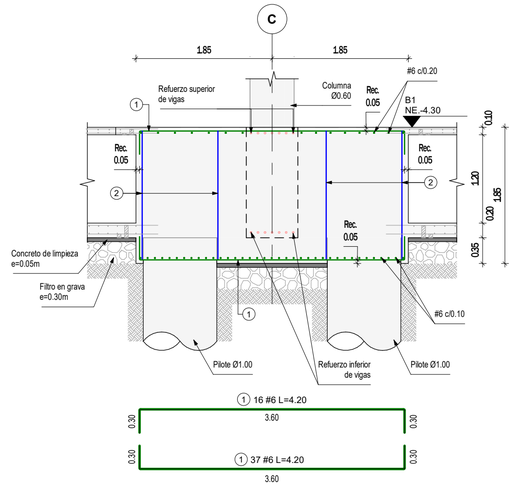

CORTE D3 - D3
Escala 1 : 50

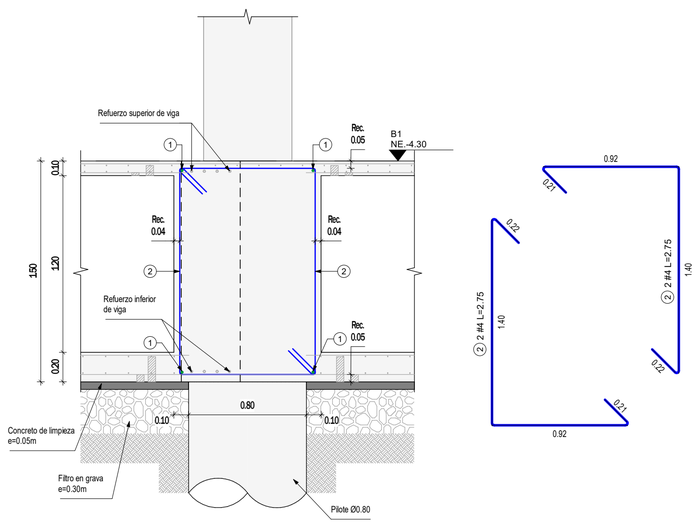

CORTE D2 - D2
Escala 1 : 25

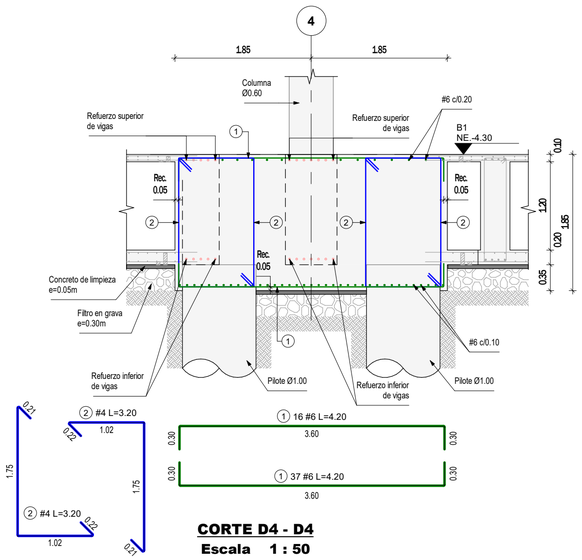

CORTE D4 - D4
Escala 1 : 50

CONCRETO
f'c=35 MPa
f'c=350 kg/cm²
f'c=5000 psi

NOTAS

1. Ver detalles generales en PL N° 01.02 y 01.03
2. Ver planta de localización de pilotes en PL N° 02.00
3. Ver planta de cimentación en PL N° 06.00

VERSIÓN : 1

PLANO N° 06.08

Aycardi Estructural

GERENTE DE PROYECTO
LUIS ENRIQUE AYCARDI F.
MAT. 2520212794 CND

INGENIERO
DANIEL E. QUICANO C.

MODELADOR
PAULA ANDREA MONTOYA RENDÓN

MODIFICACIONES	FECHA
Emisión Inicial	13-03-2026

HUMANISE

Circular Lab

HUMANISE STUDIO

EAN-0519- AES-01-EST

Calle 71 #9-84

DESPIECE DE DADOS

EAN-0519 -AES-01-EST-CIM-PL-526 06.08

REVISOR ESTRUCTURAL
JULIO CESAR SANMIGUEL CAMACHO
MAT. 25202-57738 CND

PLANO N° 06.08 VERSIÓN : 1