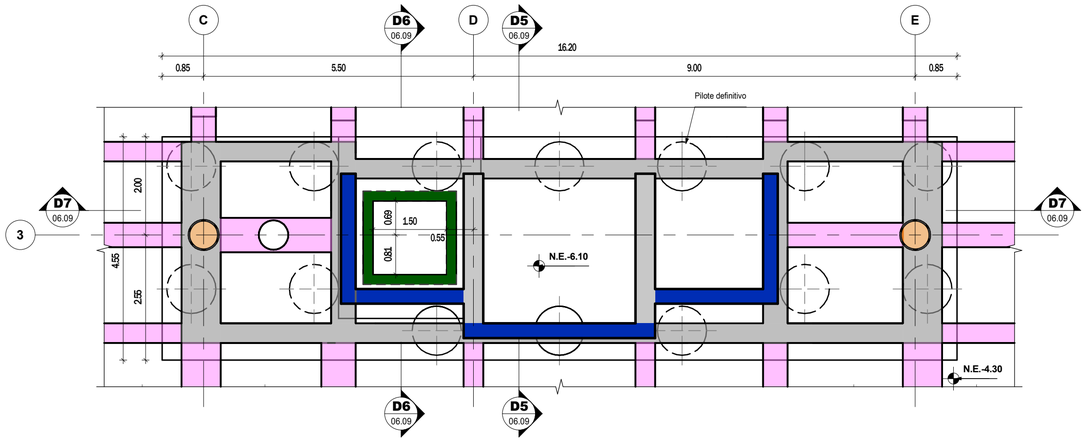

PLANTA DADO TIPO 3
Escala 1 : 75

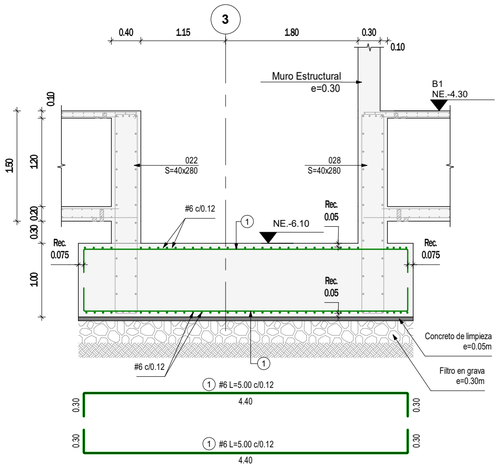

CORTE D5- D5
Escala 1 : 50

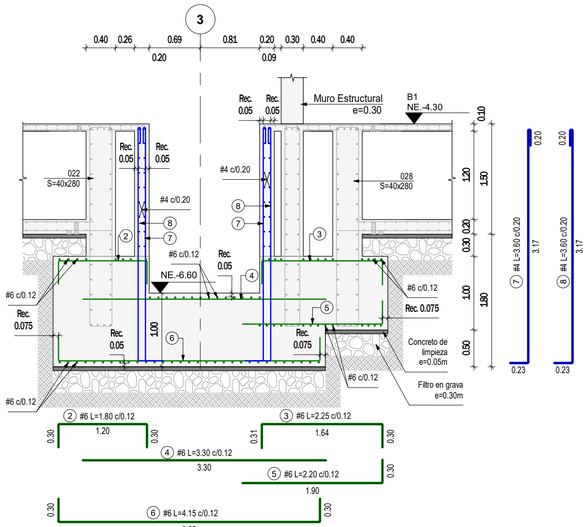

CORTE D6 - D6
Escala 1 : 50

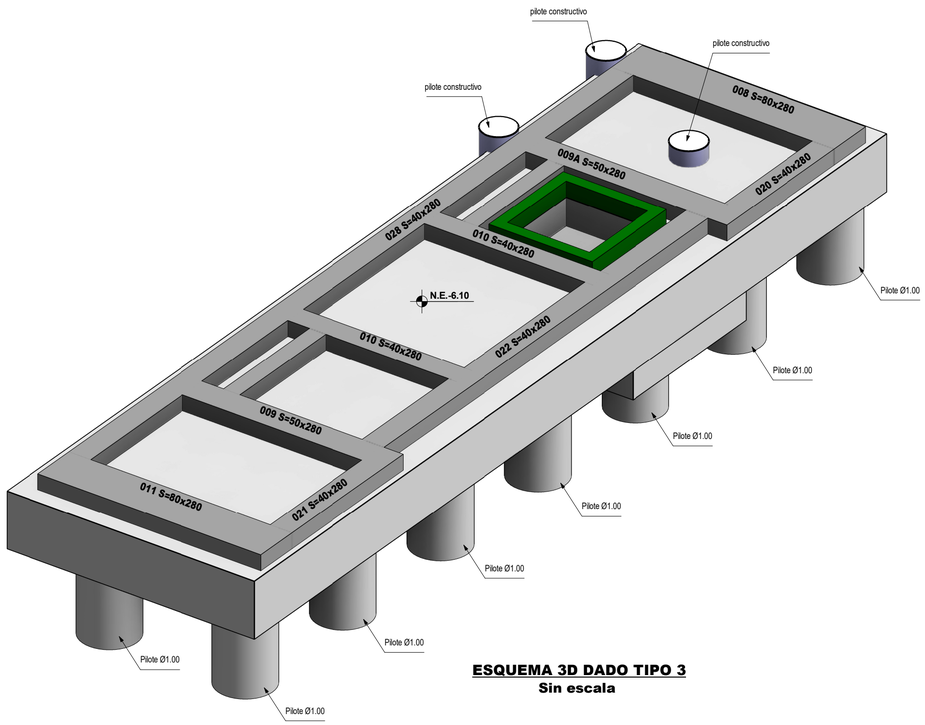

ESQUEMA 3D DADO TIPO 3
Sin escala

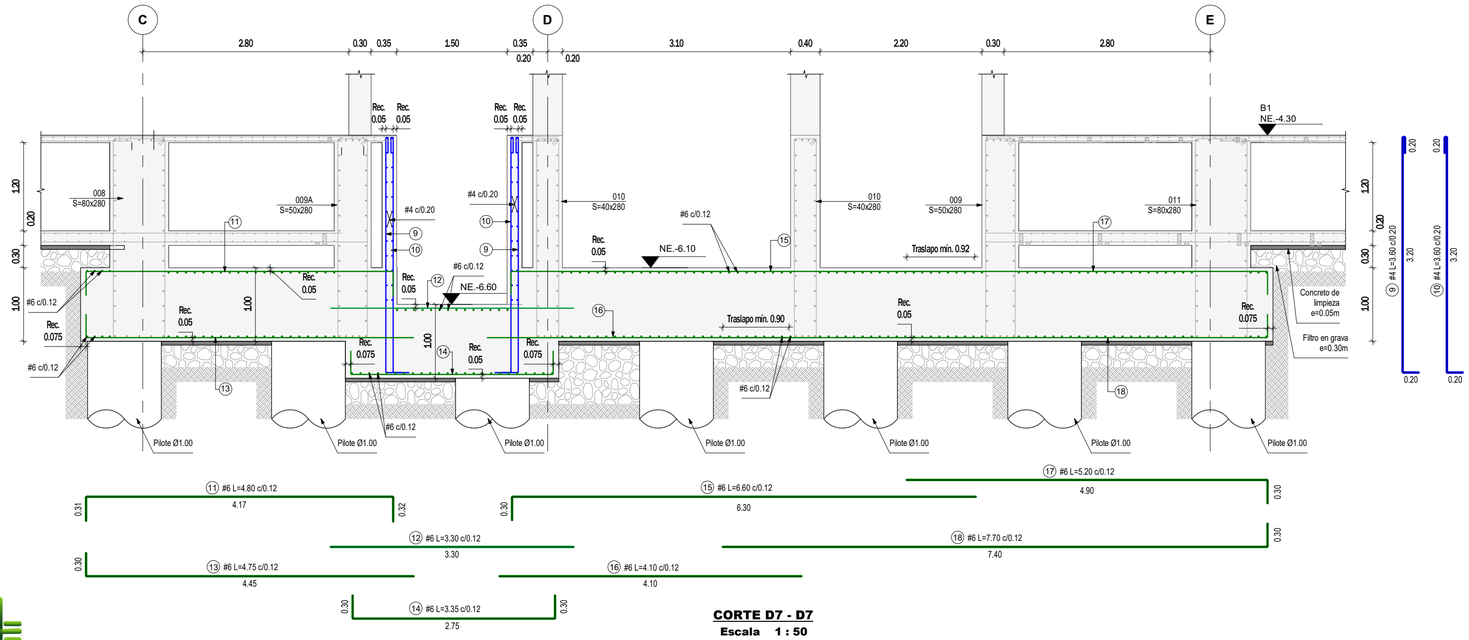

CORTE D7 - D7
Escala 1 : 50

CONCRETO
f'c=35 MPa
f'c=350 kg/cm²
f'c=5000 psi

NOTAS

1. Ver detalles generales en PL N° 01.02 y 01.03
2. Ver planta de localización de pilotes en PL N° 02.00
3. Ver planta de cimentación en PL N° 06.00

VERSIÓN : 1

PLANO N° 06.09

Aycardi Estructural

GERENTE DE PROYECTO
LUIS ENRIQUE AYCARDI F.
MAT. 2520212794 CND

INGENIERO
DANIEL E. QUICANO C.

MODELADOR
PAULA ANDREA MONTOYA RENDÓN

MODIFICACIONES	FECHA
Emisión Inicial	13-03-2026

HUMANISE

Circular Lab

HUMANISE STUDIO

EAN-0519- AES-01-EST

Calle 71 #9-84

DESPIECE DE DADOS

EAN-0519 -AES-01-EST-CIM-PL-527 06.09

REVISOR ESTRUCTURAL
JULIO CESAR SANMIGUEL CAMACHO
MAT. 25202-57738 CND

PLANO N° 06.09 VERSIÓN : 1