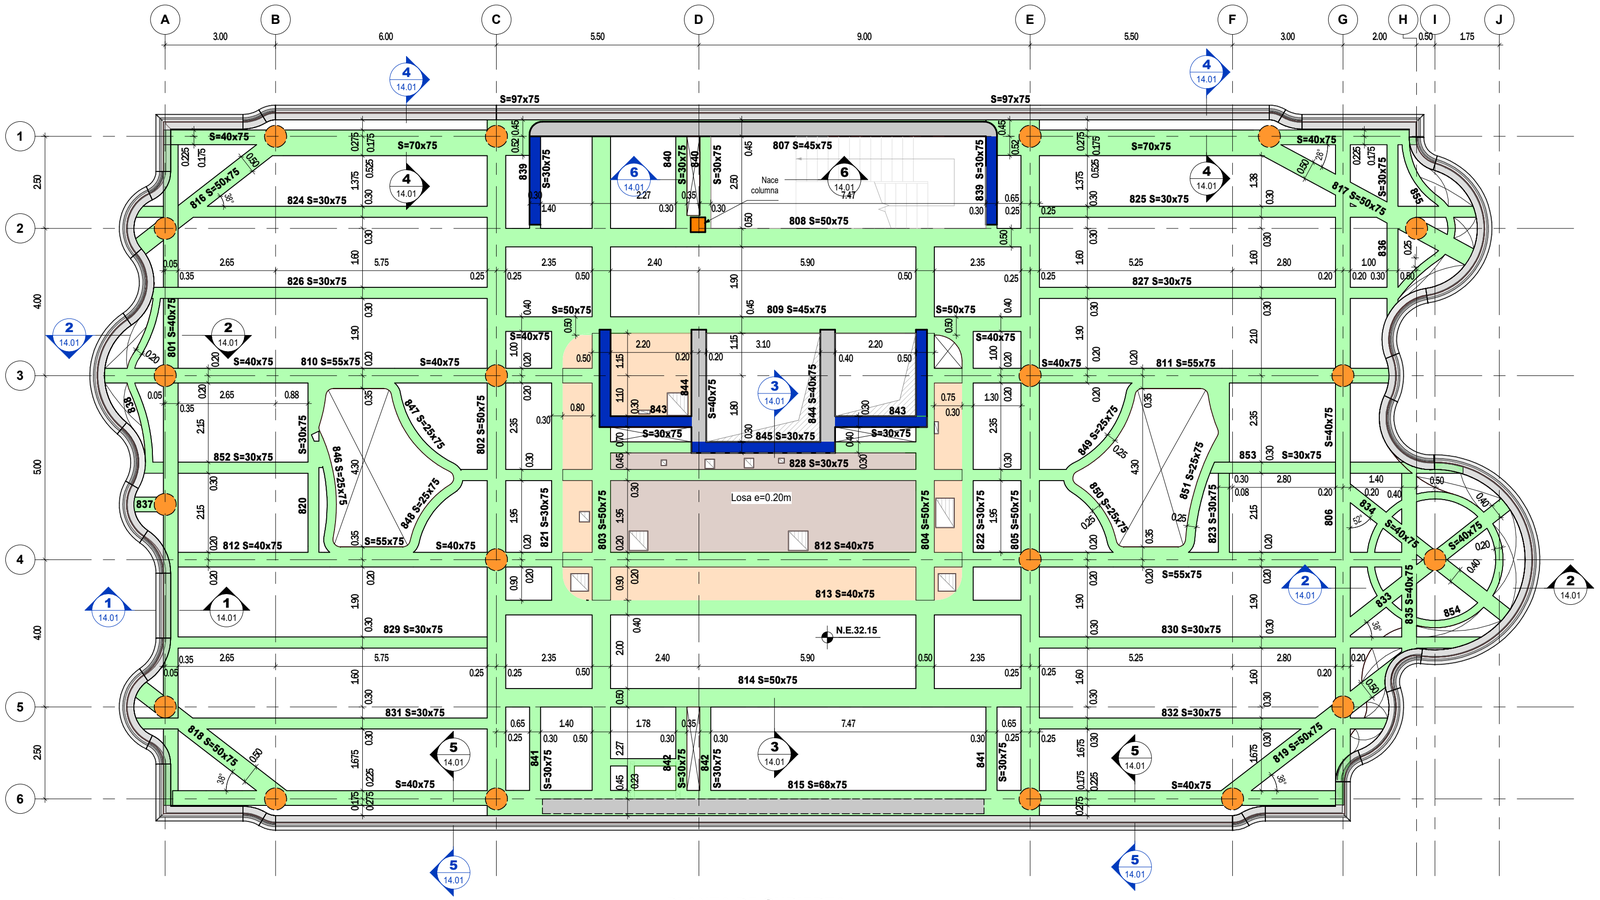

PLANTA DE CUBIERTA
Escala 1 : 100

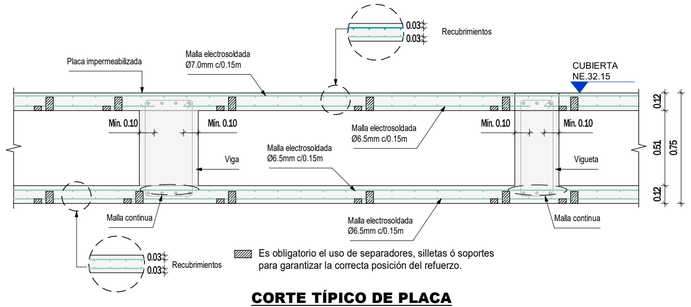

CORTE TÍPICO DE PLACA
Escala 1 : 25

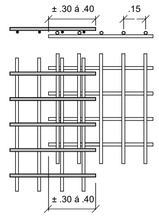

DETALLE TRASLAPO MALLAS
Escala 1 : 25

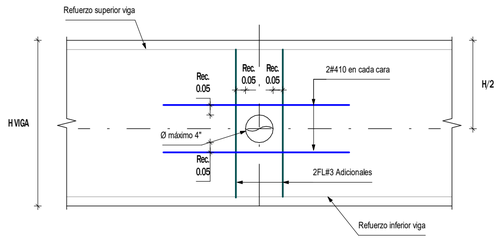

DETALLE PASE EN VIGAS AEREAS
Escala 1 : 20

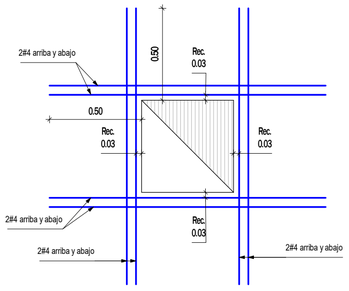

DETALLE TÍPICO REFUERZO ADICIONAL PARA DUCTOS
Escala 1 : 20

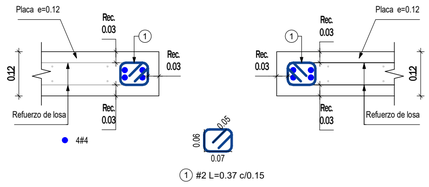

ALZADO REFUERZO ADICIONAL EN DUCTOS
Escala 1 : 10

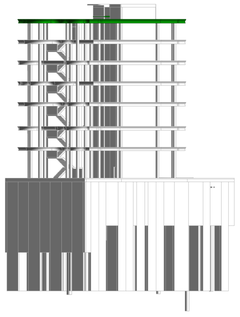

LOCALIZACIÓN DE CUBIERTA EN 3D
Escala

CONCRETO

f'c=35 MPa
f'c=350 kg/cm²
f'c=5000 psi

CONVENCIONES

- Indica columna
- Indica columna que muere
- Indica muro e=30
- Indica muro e=40
- Indica muro e=40 que muere
- Indica viga h=75
- Indica losa e=0.20 (Ver corte 3 - 3)
- Indica zona sin losa inferior

NOTAS

1. Ver detalles generales en el PL N° 01.02 y 01.03
2. Ver despieces de vigas en los PL N° 14.03 a 14.05
3. Ver cortes y esquemas 3D en el PL N° 14.01
4. Se debe garantizar un tiempo mínimo de curado intensivo de por lo menos 15 días
5. Debe estudiarse e implementar algún sistema de aislamiento térmico de la losa de concreto
6. Ver planta de puntos de anclaje y localización de ductos en el PL N°14.02

VERSIÓN : 1

PLANO N° 14.00

Aycardi Estructural

GERENTE DE PROYECTO
LUIS ENRIQUE AYCARDI F.
MAT. 2520212794 CND

INGENIERO
DANIEL E. QUICANO C.

MODELADOR
PAULA ANDREA MONTOYA RENDÓN

MODIFICACIONES	FECHA
Emisión Inicial	13-03-2026

HUMANISE

Circular Lab

HUMANISE STUDIO

EAN-0519- AES-01-EST

Calle 71 #9-84

PLANTA DE CUBIERTA

EAN-0519 -AES-01-EST-CUB-PL-115 14.00

REVISOR ESTRUCTURAL
JULIO CESAR SANMIGUEL CAMACHO
MAT. 25202-57738 CND

PLANO N° 14.00 VERSIÓN : 1