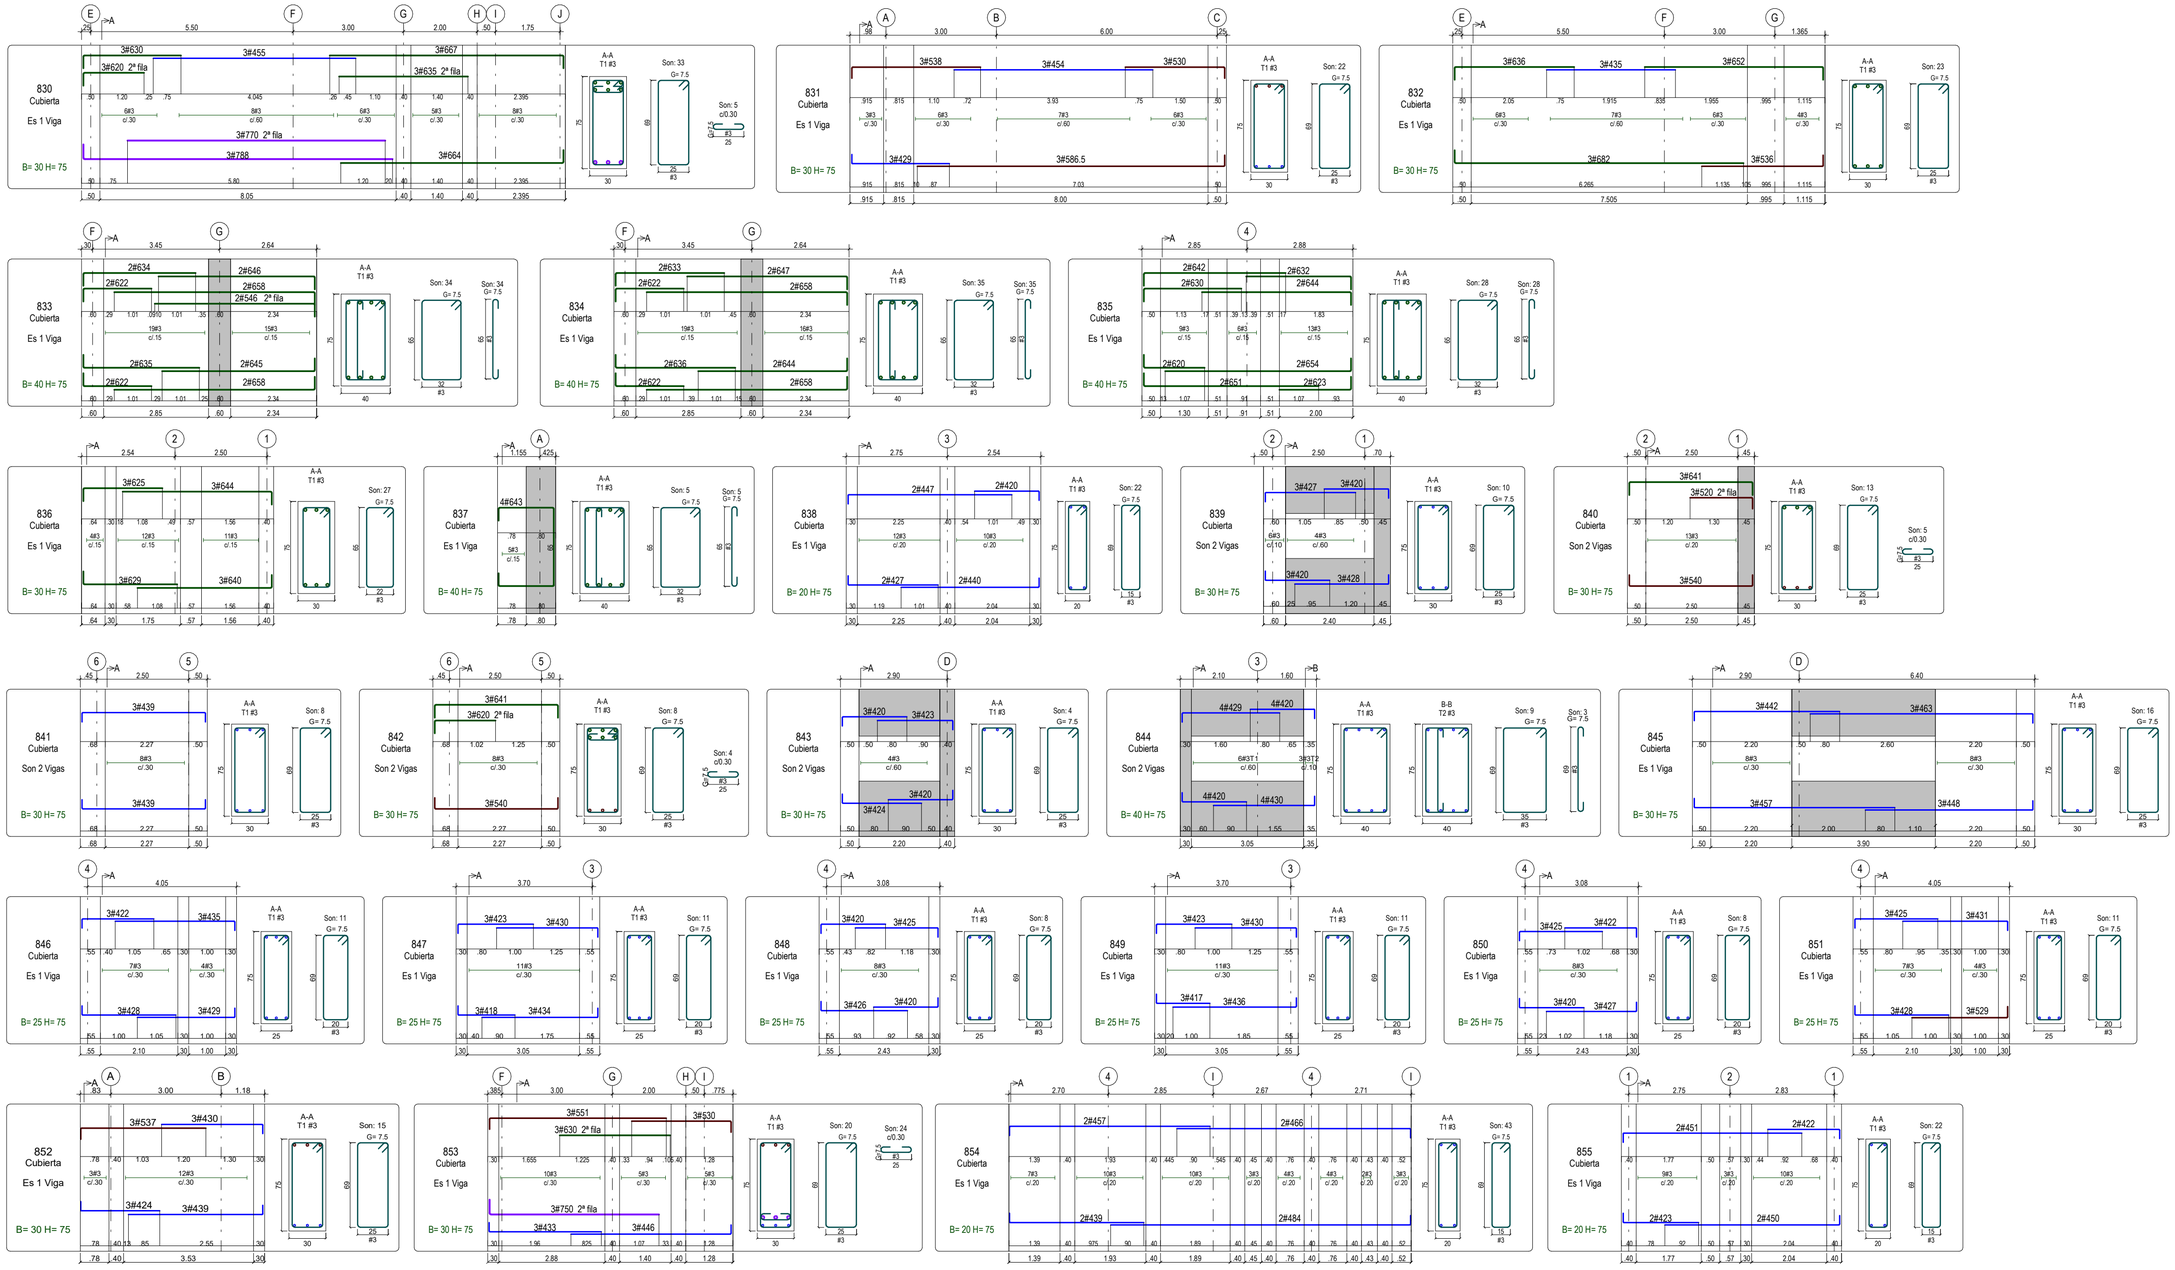

NOTAS

1. Ver detalles generales en PL N° 01.02 y 01.03
2. Ver planta de cubierta en PL N° 14.00

VERSIÓN : 1

PLANO N° 14.05

Aycardi Estructural

GERENTE DE PROYECTO
LUIS ENRIQUE AYCARDI F.
MAT. 2520212794 CND

INGENIERO
DANIEL E. QUICANO C.

MODELADOR
PAULA ANDREA MONTOYA RENDÓN

MODIFICACIONES	FECHA
Emisión Inicial	13-03-2026

HUMANISE

Circular Lab

HUMANISE STUDIO

EAN-0519- AES-01-EST

Calle 71 #9-84

DESPIECE DE VIGAS CUBIERTA

EAN-0519 -AES-01-EST-CUB-PL-579 14.05

REVISOR ESTRUCTURAL
JULIO CESAR SANMIGUEL CAMACHO
MAT. 25202-57738 CND

PLANO N° 14.05 VERSIÓN : 1