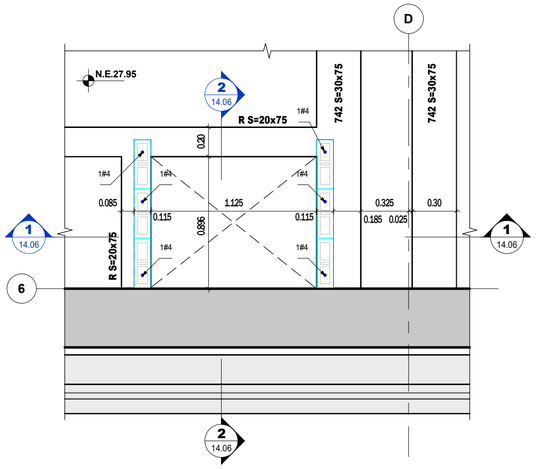

PLANTA DE MONTALIBROS PISO 7
Escala 1 : 25

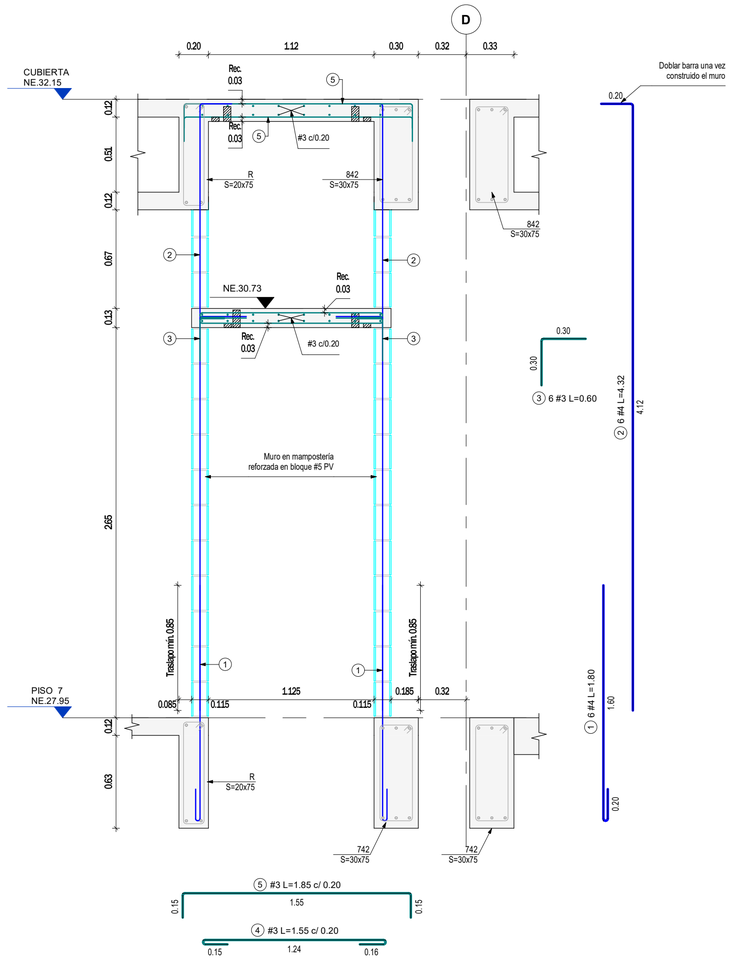

Es obligatorio el uso de separadores, silletas o soportes para garantizar la correcta posición del refuerzo.

CORTE 1 - 1
Escala 1 : 25

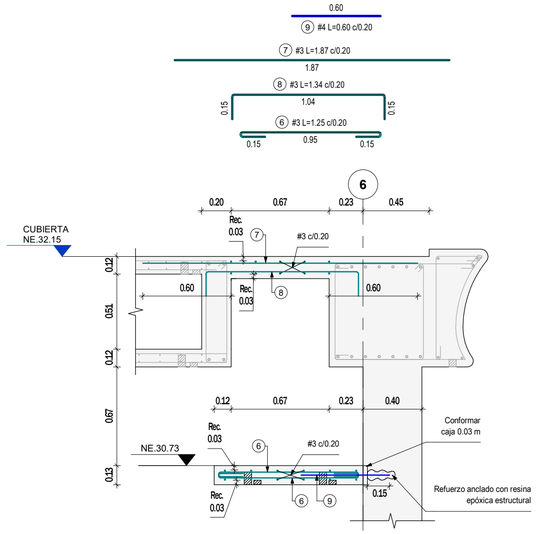

Es obligatorio el uso de separadores, silletas o soportes para garantizar la correcta posición del refuerzo.

CORTE 2 - 2
Escala 1 : 25

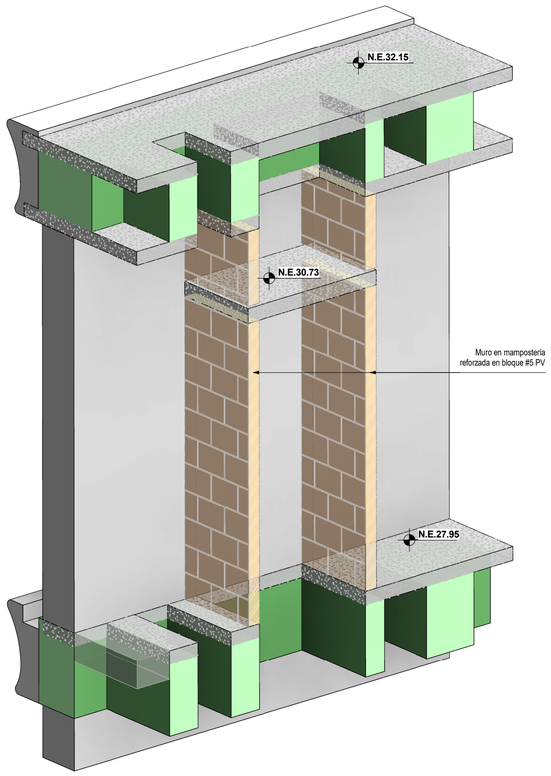

ESQUEMA 3D MONTALIBROS DE PISO 7 A CUBIERTA
Sin escala

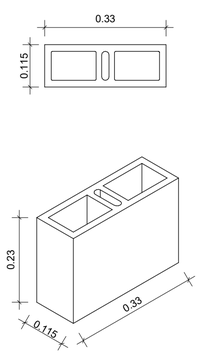

BLOQUE N° 5 PERFORACIÓN VERTICAL
Escala 1 : 10

DISPOSICIÓN DEL MORTERO

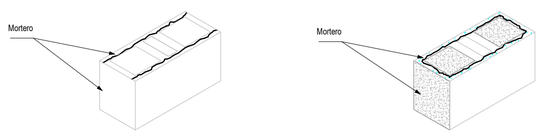

CASO TÍPICO **CASO DE CELDA RELLENAS**

1. El mortero de pega se hara según la siguiente disposición:
2. Las juntas verticales y horizontales son de 10 mm. con tolerancia de 3 mm.
3. Toda celda reforzada debe llevar ventana de limpieza
4. El mortero de relleno lleva agregado maximo de 3/8"

REQUISITOS DIMENSIONALES PARA UNIDADES DE MAMPOSTERÍA

tp = pared exterior portante > 2.5 cm.
tv = pared entre celdas > 2.5 cm.
v = dimension del vacio > .50 cm.

CONCRETO
f'c=35 MPa
f'c=350 kg/cm²
f'c=5000 psi

MUROS NO ESTRUCTURALES DE MAMPOSTERÍA

f'cr (Kg/cm²)	f'cp (Kg/cm²)	f'cm (Kg/cm²)	f'cu (Kg/cm²)
Resistencia última a la compresión del mortero de relleno	Resistencia última a la compresión del mortero de pega	Resistencia última a la compresión del murete en mampostería	Resistencia última a la compresión de la unidad de mampostería
100	100	60	130

CONVENCIONES

Indica muro e=40
Indica muro en mampostería

NOTAS

1. Ver detalles generales en el PL N° 01.02 y 01.03
2. Ver planta de piso 7 y detalles de riosttra en el PL N°13.00
3. Ver planta de cubierta en el PL N° 14.00

VERSIÓN : 1

PLANO N° 14.06

Aycardi Estructural

GERENTE DE PROYECTO
LUIS ENRIQUE AYCARDI F.
MAT. 2520212794 CND

INGENIERO
DANIEL E. QUICANO C.

MODELADOR
PAULA ANDREA MONTOYA RENDÓN

MODIFICACIONES	FECHA
Emisión Inicial	13-03-2026

HUMANISE

Circular Lab

HUMANISE STUDIO

EAN-0519- AES-01-EST

Calle 71 #9-84

PLANTA Y CORTES ASCENSOR MONTALIBROS

EAN-0519 -AES-01-EST-CUB-PL-580 14.06

REVISOR ESTRUCTURAL
JULIO CESAR SANMIGUEL CAMACHO
MAT. 25202-57738 CND

PLANO N° 14.06 VERSIÓN : 1