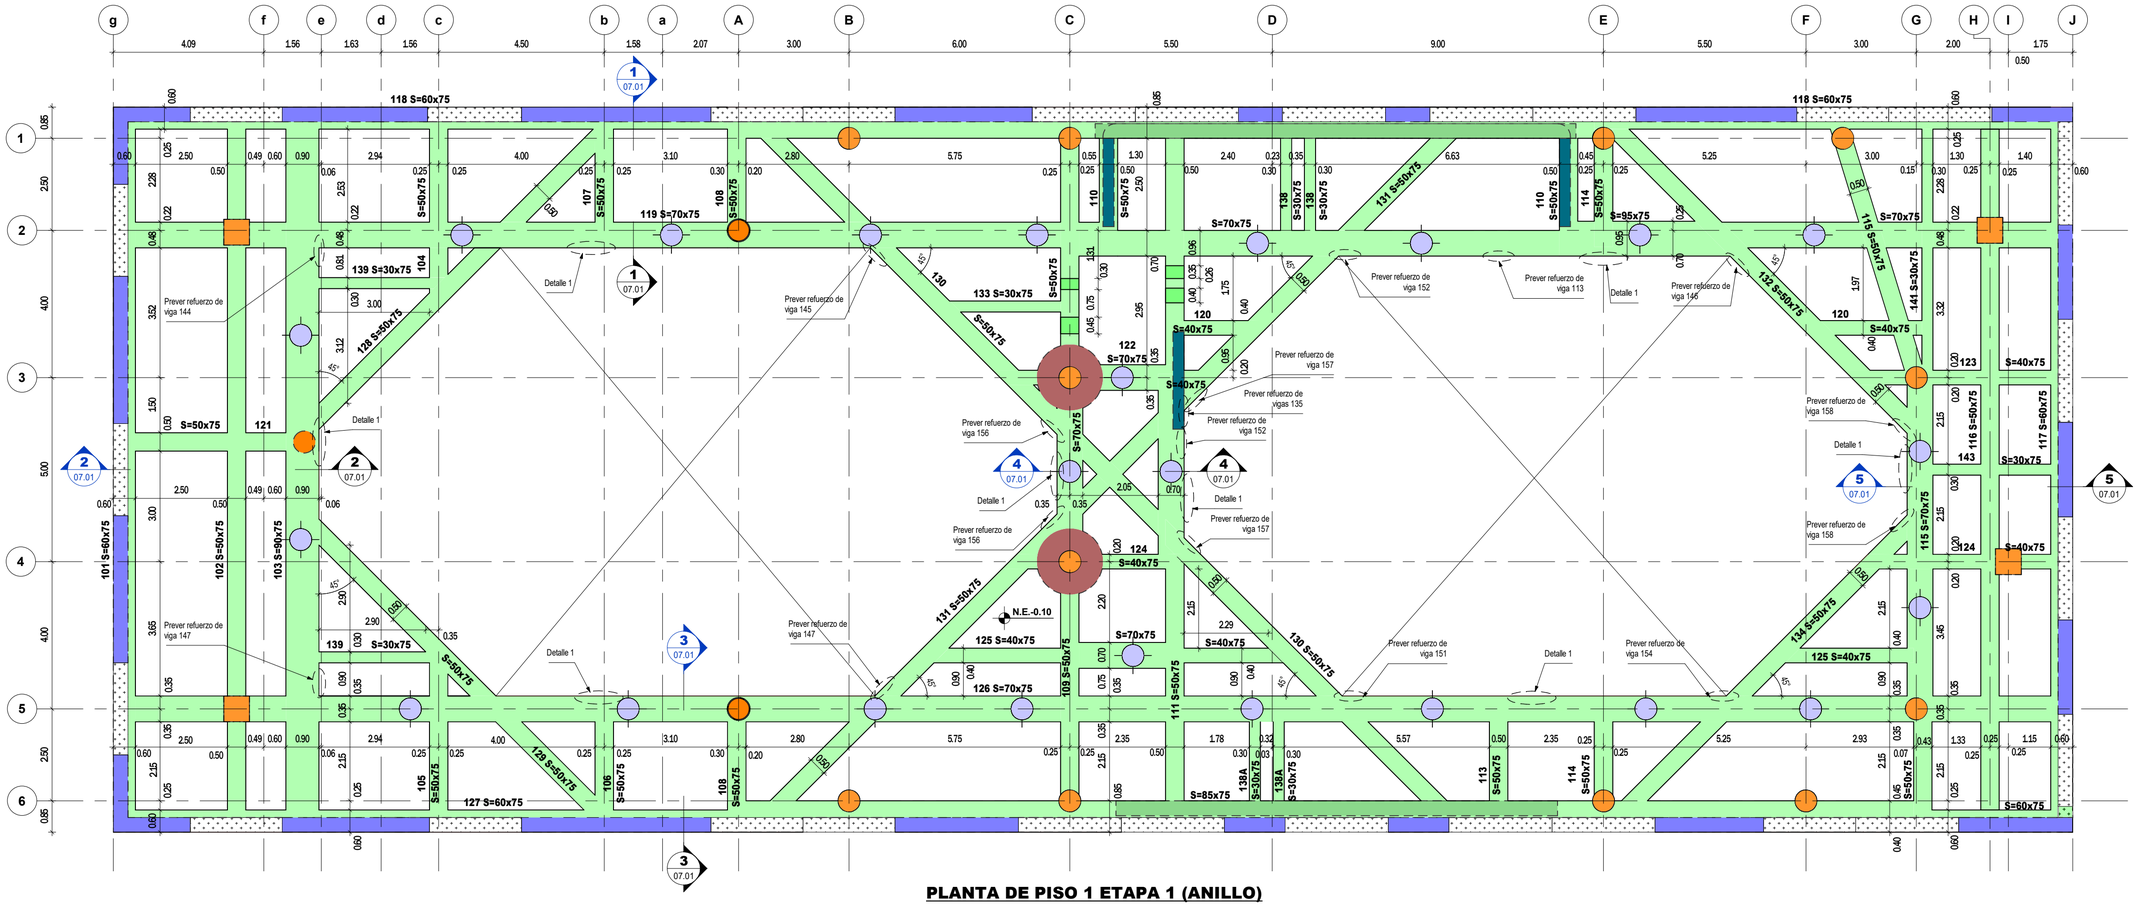

PLANTA DE PISO 1 ETAPA 1 (ANILLO)

Escala 1 : 100

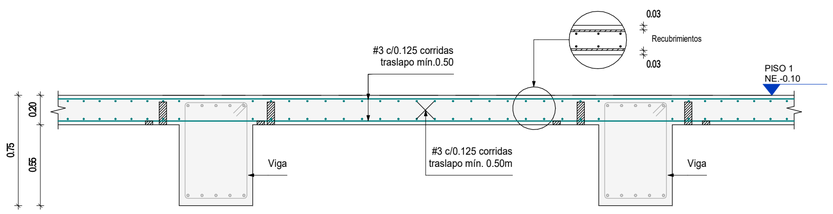

Es obligatorio el uso de separadores, silletas ó soportes para garantizar la correcta posición del refuerzo.

CORTE TÍPICO PLACA ANILLO

Escala 1 : 25

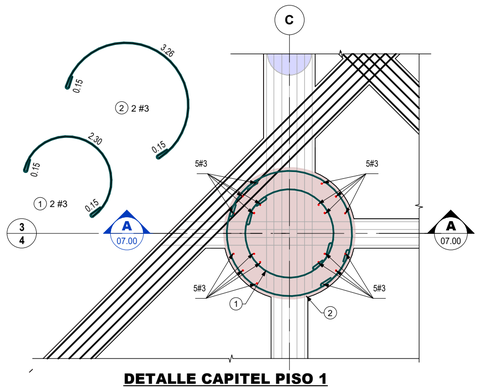

DETALLE CAPITEL PISO 1

Escala 1 : 50

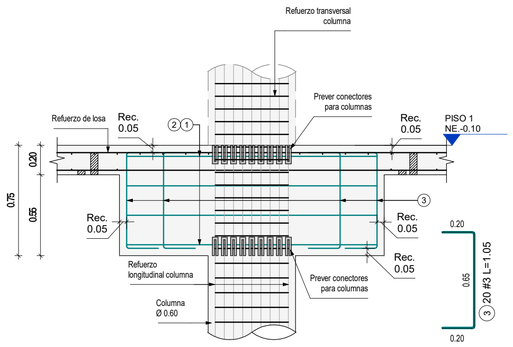

CORTE A - A

Escala 1 : 25

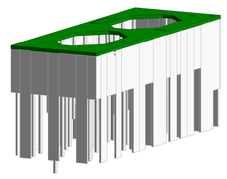

LOCALIZACIÓN DE PISO 1 EN 3D

Escala

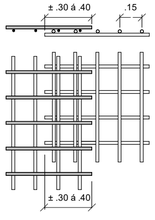

DETALLE TRASLAPO MALLAS

Escala 1 : 25

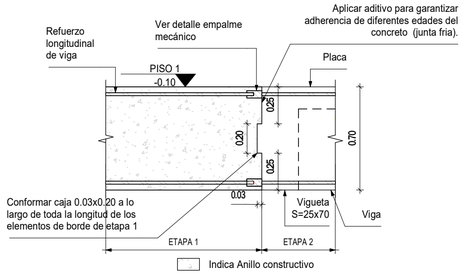

DETALLE 1 - CONEXIÓN DE VIGUETA DE BORDE ETAPA 2 A ANILLO CONSTRUCTIVO

Escala 1 : 25

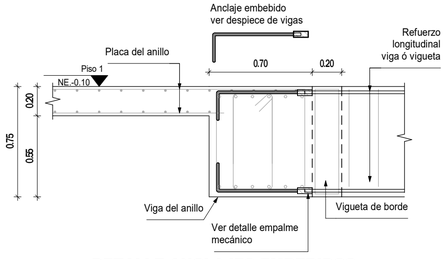

DETALLE ANCLAJES EMBEBIDOS

Escala 1 : 25

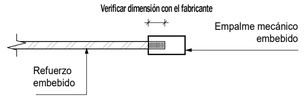

DETALLE EMPALME MECÁNICO

Escala 1 : 10

CONCRETO

f'c=35 MPa
f'c=350 kg/cm²
f'c=5000 psi

CONVENCIONES

- Indica pilotes constructivos
- Indica columna S=Ø60
- Indica capitel Ø180
- Indica muro e=30
- Indica muro e=40
- Indica viga h=75
- Indica viga h=75
- Indica pantalla preexcavada
- Indica barrete

NOTAS

1. Ver detalles generales en el PL. 01.02 y 01.03
2. Ver cortes y esquemas 3D en el PL N° 07.01
3. Ver despieces de vigas en los PL. N° 07.11 a 07.16

VERSIÓN : 1

PLANO N° 07.00

Aycardi Estructural

GERENTE DE PROYECTO
LUIS ENRIQUE AYCARDI F.
MAT. 2520212794 CND

INGENIERO
DANIEL E. QUICANO C.

MODELADOR
PAULA ANDREA MONTOYA RENDÓN

MODIFICACIONES	FECHA
Emisión Inicial	13-03-2026

HUMANISE STUDIO

EAN-0519- AES-01-EST

Calle 71 #9-84

PLANTA DE PISO 1 ETAPA 1 (ANILLO)

EAN-0519 -AES-01-EST-N01-PL-104 07.00

REVISOR ESTRUCTURAL
JULIO CESAR SANMIGUEL CAMACHO
MAT. 25202-57738 CND

PLANO N° 07.00 VERSIÓN : 1