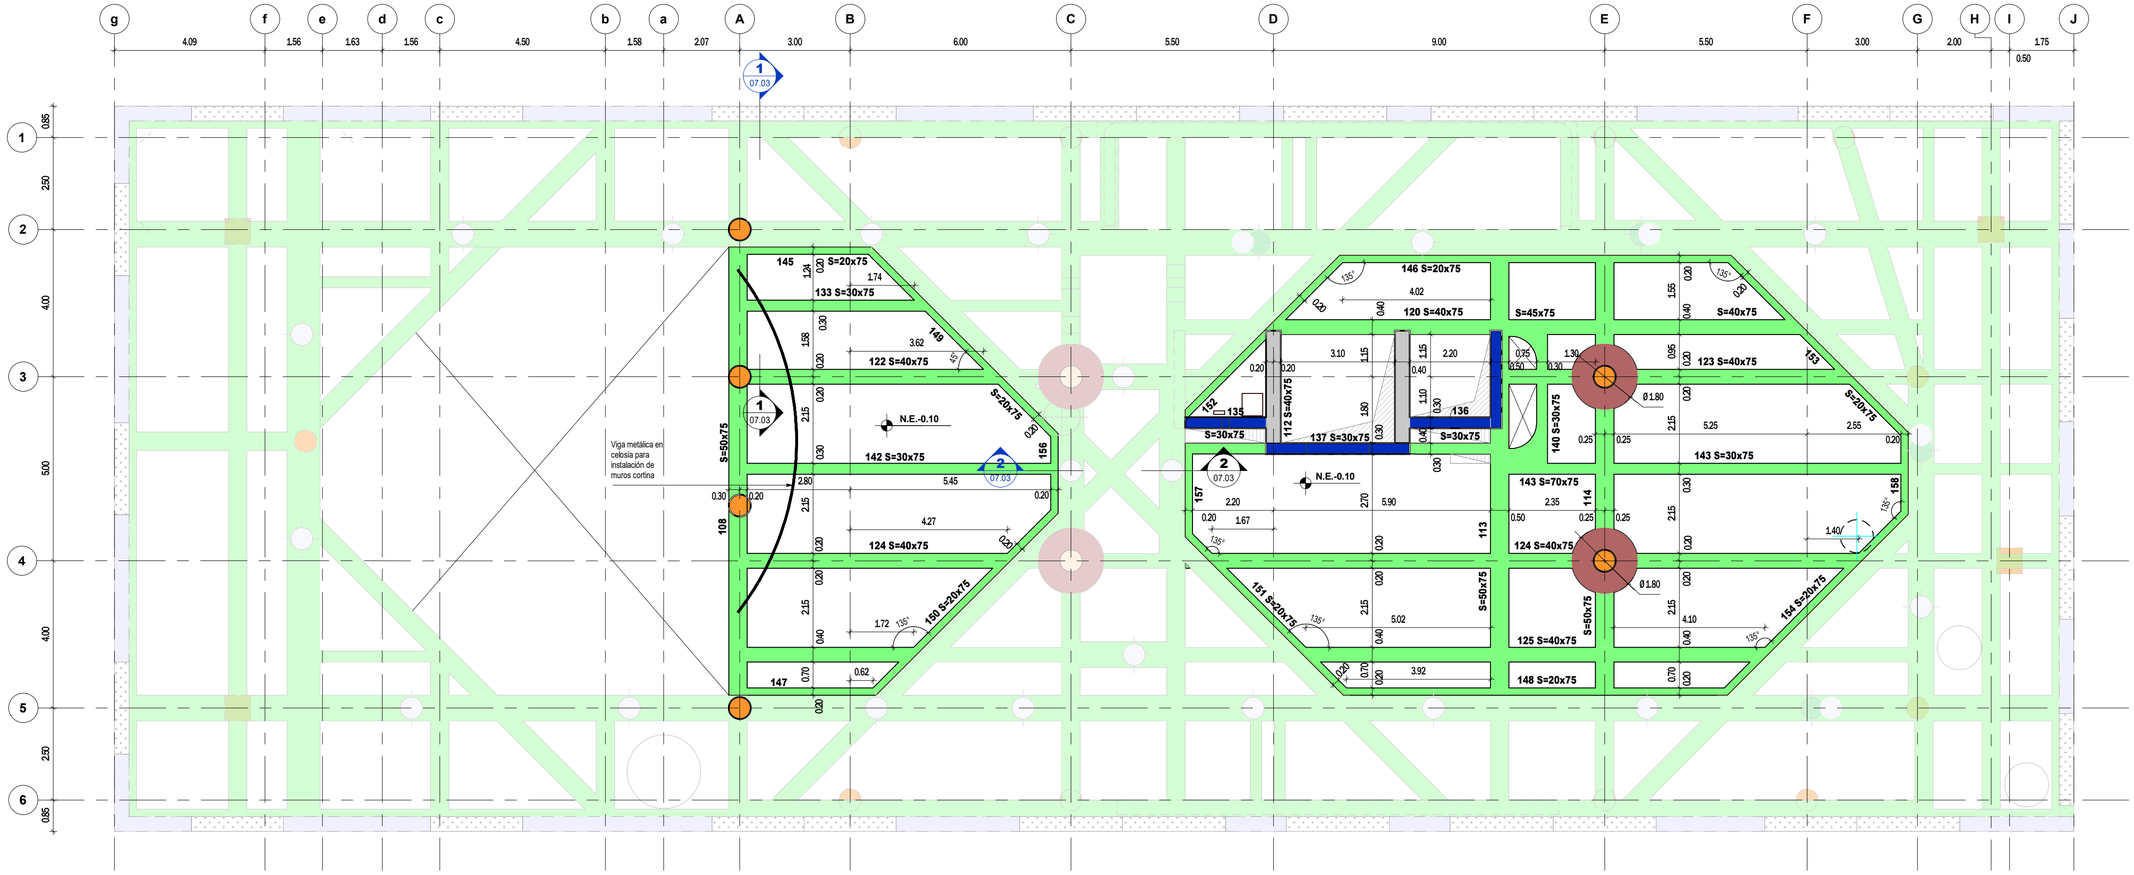

PLANTA DE PISO 1 ETAPA 2 (COMPLEMENTO)
Escala 1 : 100

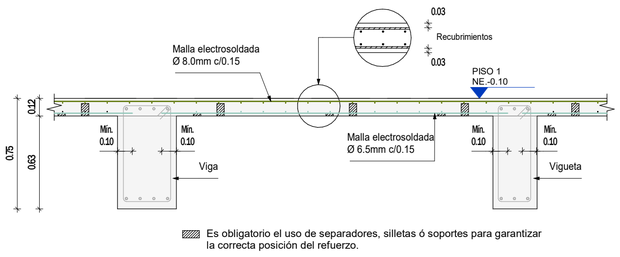

CORTE TÍPICO DE PLACA COMPLEMENTO
Escala 1 : 25

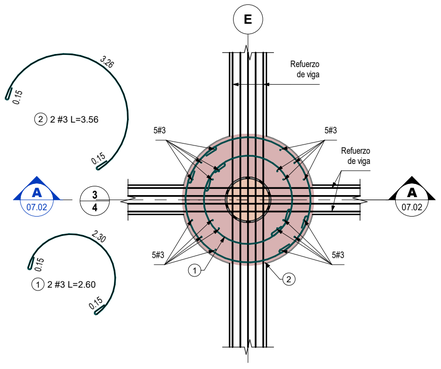

DETALLE CAPITEL
Escala 1 : 50

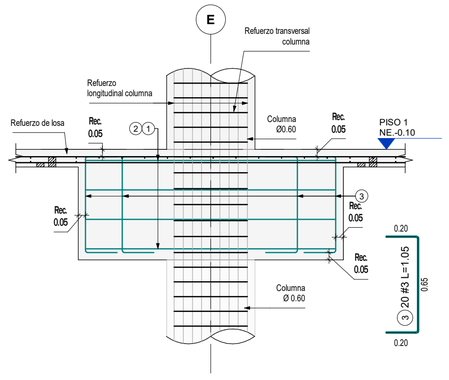

CORTE A - A PISO 1
Escala 1 : 25

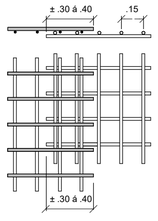

DETALLE TRASLAPO MALLAS
Escala 1 : 25

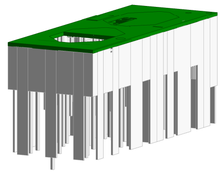

LOCALIZACIÓN DE PISO 1 EN 3D
Escala

CONCRETO
f'c=35 MPa
f'c=350 kg/cm²
f'c=5000 psi

CONVENCIONES

- Indica pilotes constructivos
- Indica columna S=Ø60
- Indica capitel Ø180
- Indica muro e=30
- Indica muro e=40
- Indica viga h=75
- Indica pantalla preexcavada
- Indica barrete

NOTAS

1. Ver detalles generales en el PL. 01.02 y 01.03
2. Ver cortes y esquemas 3D en el PL. N° 07.03
3. Ver despieces de vigas en los PL. N° 07.11 a 07.16

VERSIÓN : 1

PLANO N° 07.02

Aycardi Estructural

GERENTE DE PROYECTO
LUIS ENRIQUE AYCARDI F.
MAT. 2520212794 CND

INGENIERO
DANIEL E. QUICANO C.

MODELADOR
PAULA ANDREA MONTOYA RENDÓN

MODIFICACIONES	FECHA
Emisión Inicial	13-03-2026

HUMANISE STUDIO

EAN-0519- AES-01-EST

Calle 71 #9-84

PLANTA DE PISO 1 ETAPA 2 (COMPLEMENTO)

EAN-0519 -AES-01-EST-N01-PL-105 07.02

REVISOR ESTRUCTURAL
JULIO CESAR SANMIGUEL CAMACHO
MAT. 25202-57738 CND

PLANO N° 07.02 VERSIÓN : 1