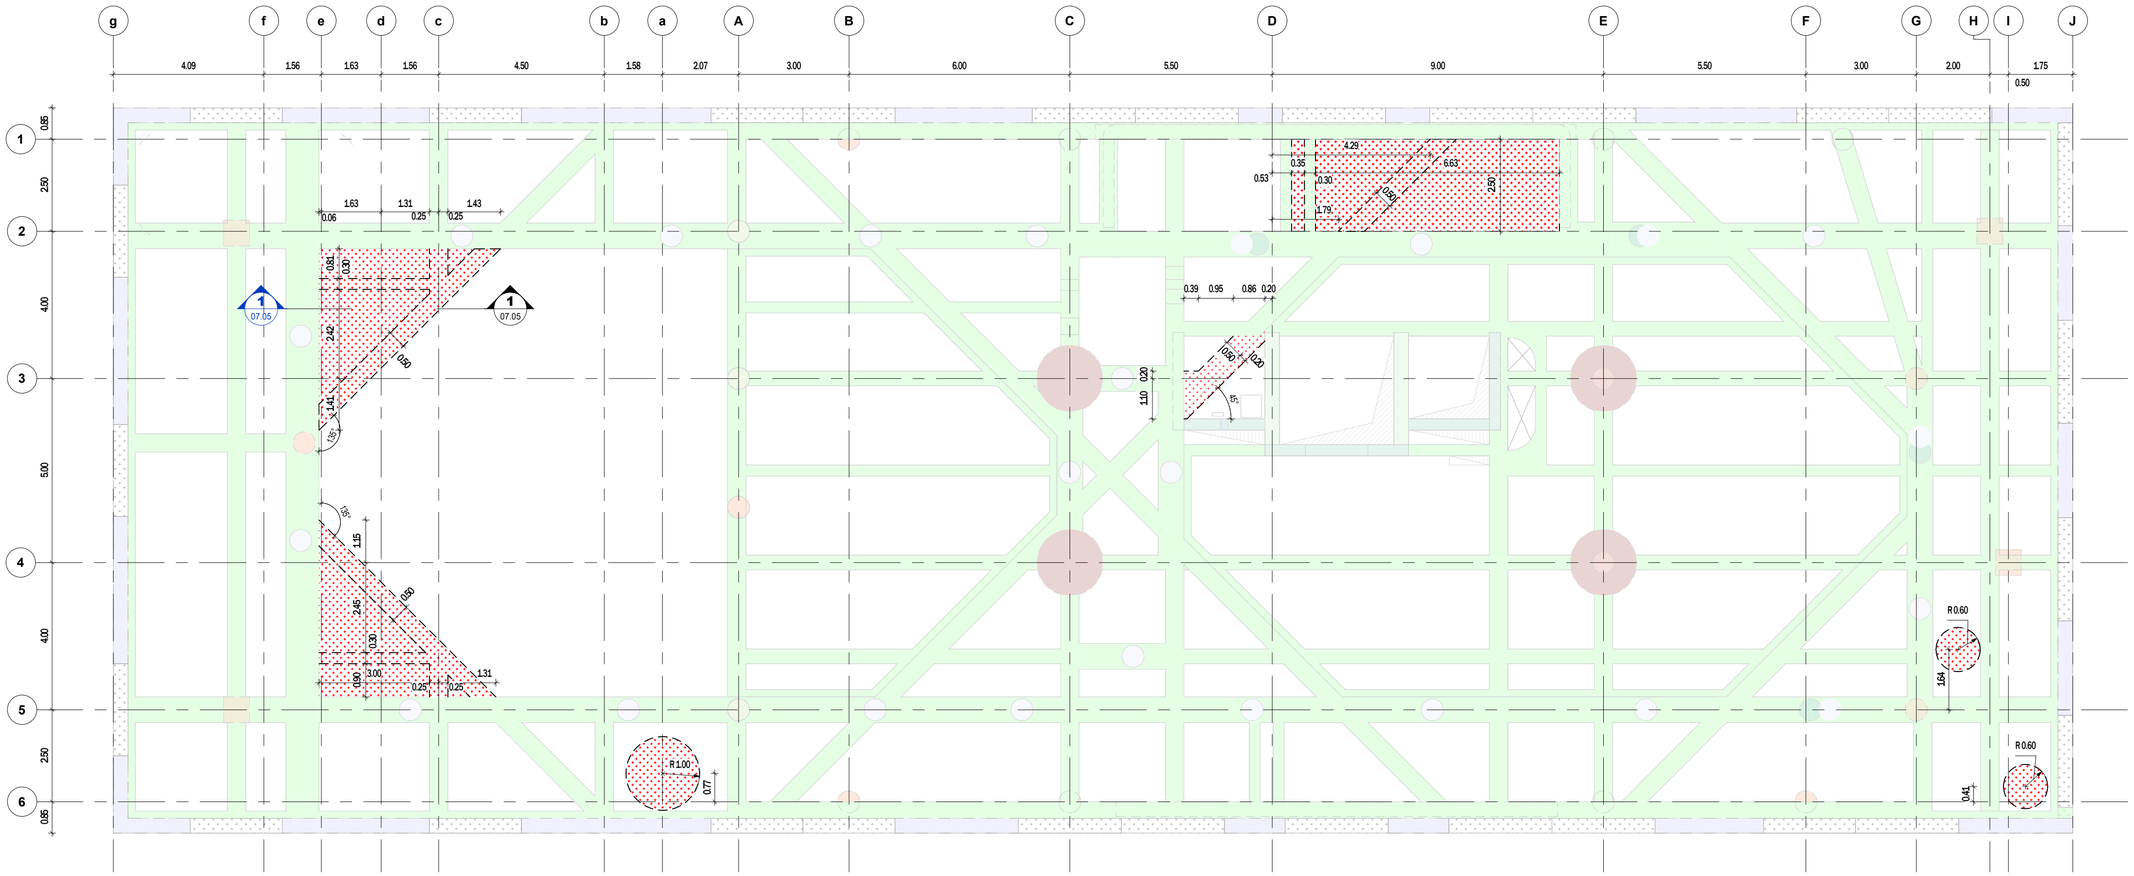

PLANTA DE PISO 1 ETAPA 3 (DEMOLICIÓN)
Escala 1 : 100

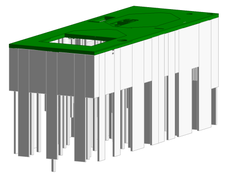

LOCALIZACIÓN DE PISO 1 EN 3D
Escala

CONVENCIONES

- Indica pilotes constructivos
- Indica columna S=Ø60
- Indica capitel Ø180
- Indica muro e=30
- Indica muro e=40
- Indica viga h=75
- Indica demolición cuidadosa sin conservar el refuerzo

NOTAS

1. Ver detalles generales en PL N° 01.02 y 01.03
2. Ver planta de piso 1 etapa 3 (demolición) en PL N° 07.04

VERSIÓN : 1

PLANO N° 07.04

Aycardi Estructural

GERENTE DE PROYECTO
LUIS ENRIQUE AYCARDI F.
MAT. 2520212794 CND

INGENIERO
DANIEL E. QUICANO C.

MODELADOR
PAULA ANDREA MONTOYA RENDÓN

MODIFICACIONES	FECHA
Emisión Inicial	13-03-2026

HUMANISE

Circular Lab

HUMANISE STUDIO

EAN-0519- AES-01-EST

Calle 71 #9-84

PLANTA DE PISO 1 ETAPA 3 (DEMOLICIÓN)

EAN-0519 -AES-01-EST-N01-PL-106 07.04

REVISOR ESTRUCTURAL
JULIO CESAR SANMIGUEL CAMACHO
MAT. 25202-57738 CND

PLANO N° 07.04 VERSIÓN : 1