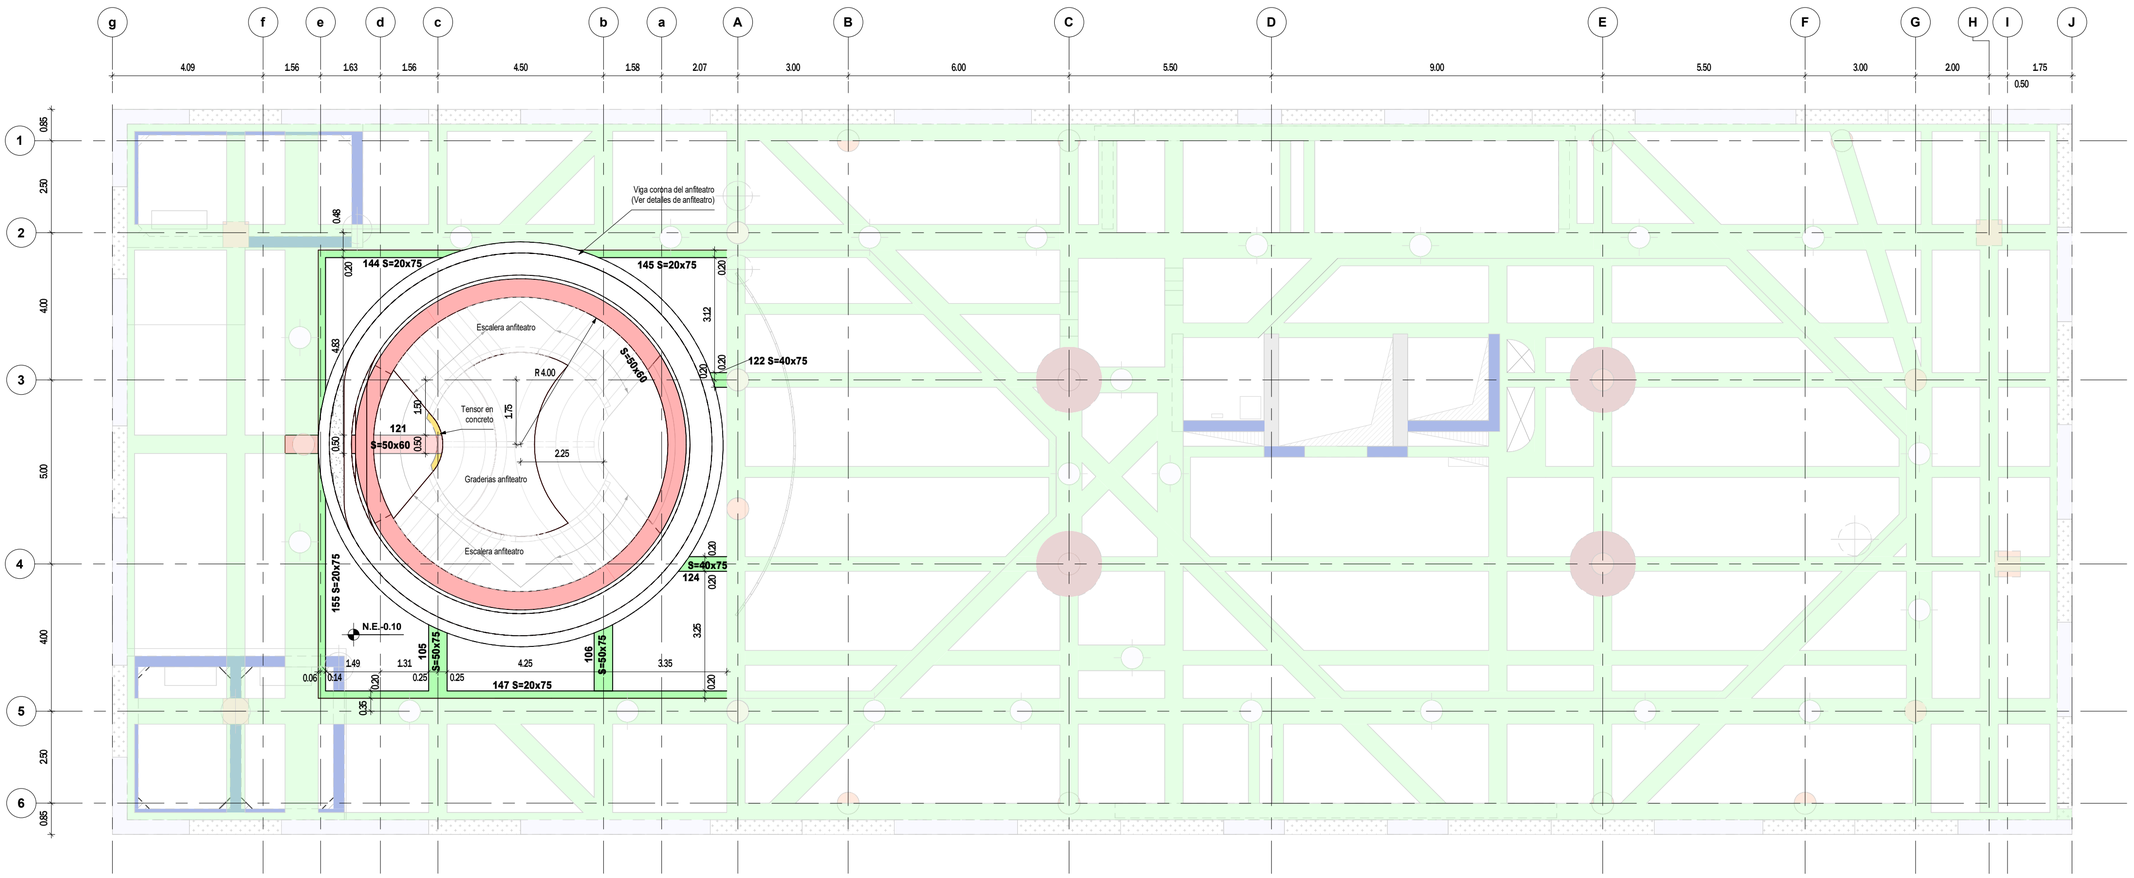


**PLANTA DE PISO 1 ETAPA 4 (COMPLEMENTO ANFITEATRO)**
**Escala 1 : 100**

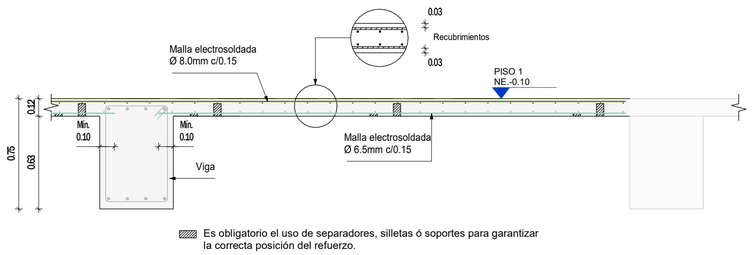


**CORTE TÍPICO DE PLACA**
**Escala 1 : 25**

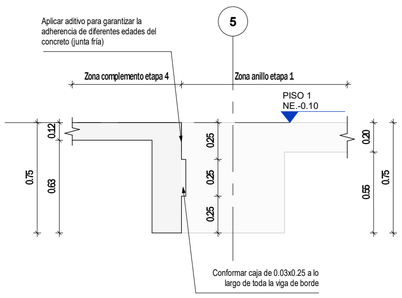


**DETALLE 1 VINCULACIÓN DE VIGAS ETAPA 1 Y ETAPA 4**
**Escala 1 : 25**

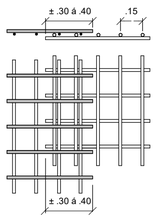


**DETALLE TRASLAPO MALLAS**
**Escala 1 : 25**

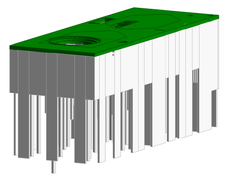

**LOCALIZACIÓN DE PISO 1 EN 3D**
**Escala**

**CONCRETO**
**f'c=35 MPa**
**f'c=350 kg/cm²**
**f'c=5000 psi**

**CONVENCIONES**

- Indica pilotes constructivos
- Indica columna S=Ø60
- Indica capitel Ø180
- Indica muro e=30
- Indica muro e=40
- Indica muro e=50
- Indica viga h=60
- Indica viga h=75
- Indica demolición cuidadosa sin conservar el refuerzo

**NOTAS**

1. Ver detalles generales en PL N° 01.02 y 01.03
2. Ver cortes y esquema 3D en el PL N° 07.07

VERSIÓN : 1

PLANO N° 07.06

Aycardi Estructural

GERENTE DE PROYECTO
LUIS ENRIQUE AYCARDI F.
**MAT. 2520212794 CND**

INGENIERO
DANIEL E. QUICANO C.

MODELADOR
PAULA ANDREA MONTOYA RENDÓN

| MODIFICACIONES | FECHA |
|---|---|
| Emisión Inicial | 13-03-2026 |

HUMANISE

Circular Lab

**HUMANISE STUDIO**

EAN-0519- AES-01-EST

Calle 71 #9-84

**PLANTA DE PISO 1 ETAPA 4 (COMPLEMENTO ANFITEATRO)**

EAN-0519 -AES-01-EST-N01-PL-107 07.06

REVISOR ESTRUCTURAL
JULIO CESAR SANMIGUEL CAMACHO
MAT. 25202-57738 CND

PLANO N° 07.06 VERSIÓN : 1