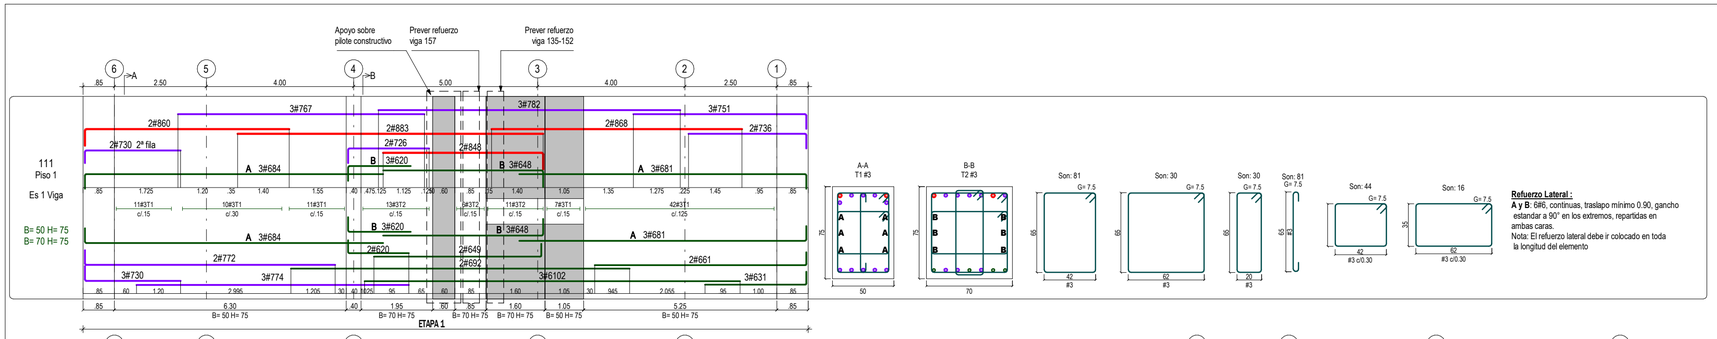


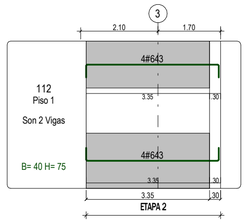


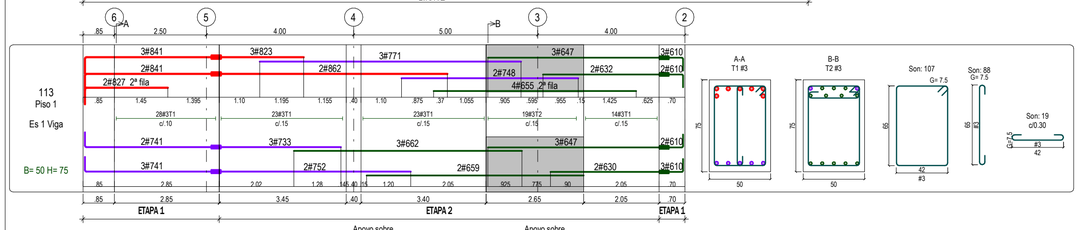


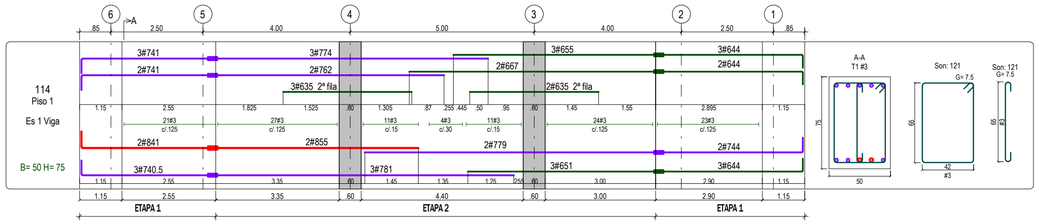


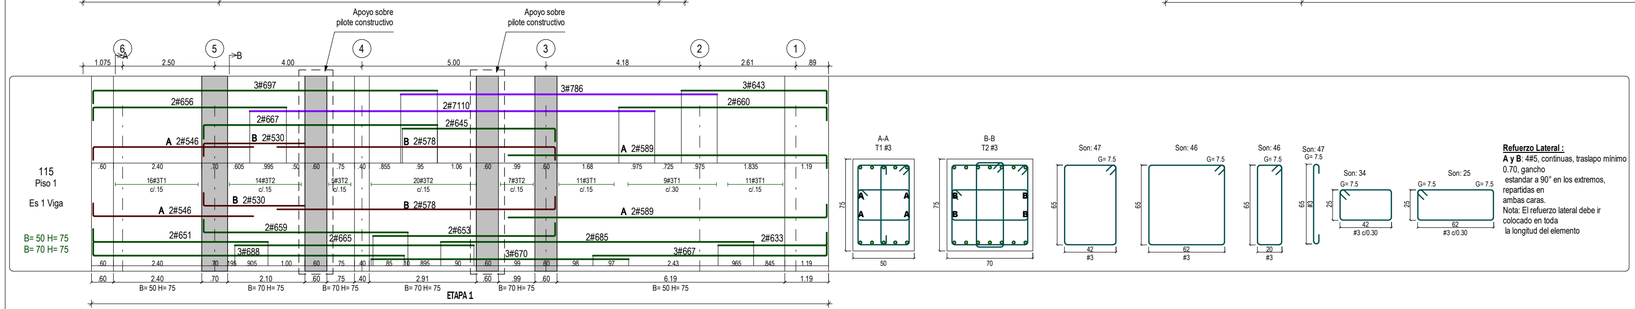


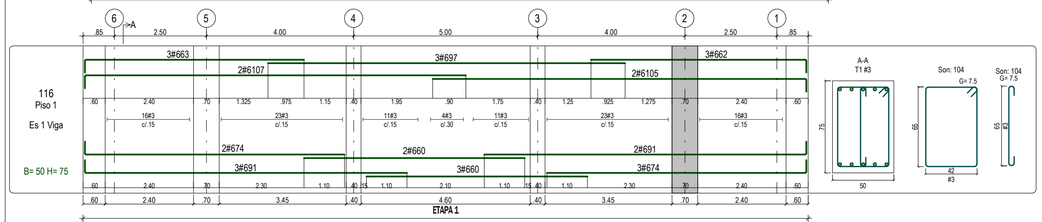


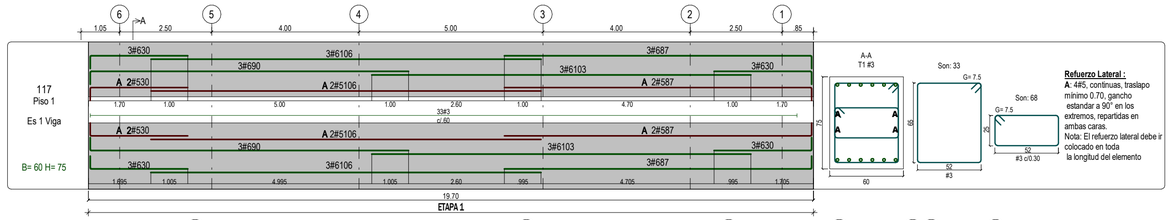


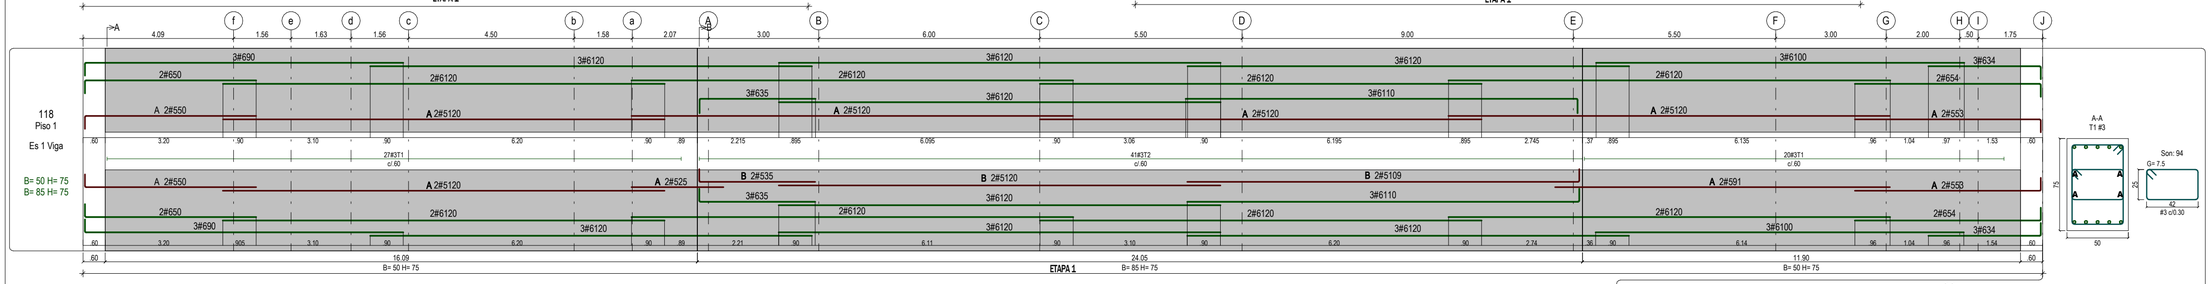


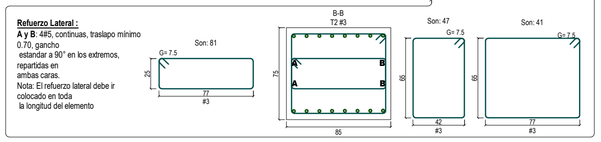


**CONVENCIONES**

- Indica empalme mecánico
- Indica disco de anclaje (El color depende del diámetro del refuerzo)

**NOTAS**

1. Ver detalles generales en PL N° 01.02 y 01.03
2. Ver planta de piso 1 en PL N° 07.00, 07.02, 07.04, 07.06 y 07.08

VERSIÓN : 1

PLANO N° 07.12

Aycardi Estructural

GERENTE DE PROYECTO
LUIS ENRIQUE AYCARDI F.
MAT. 2520212794 CND

INGENIERO
DANIEL E. QUICANO C.

MODELADOR
PAULA ANDREA MONTOYA RENDÓN

| MODIFICACIONES | FECHA |
|---|---|
| Emisión Inicial | 13-03-2026 |
| | |
| | |
| | |
| | |
| | |

HUMANISE

Circular Lab

HUMANISE STUDIO

EAN-0519- AES-01-EST

Calle 71 #9-84

**DESPIECES DE VIGAS PISO 1**

EAN-0519 -AES-01-EST-N01-PL-535 07.12

REVISOR ESTRUCTURAL
JULIO CESAR SANMIGUEL CAMACHO
MAT. 25202-57738 CND

PLANO N° 07.12 VERSIÓN : 1