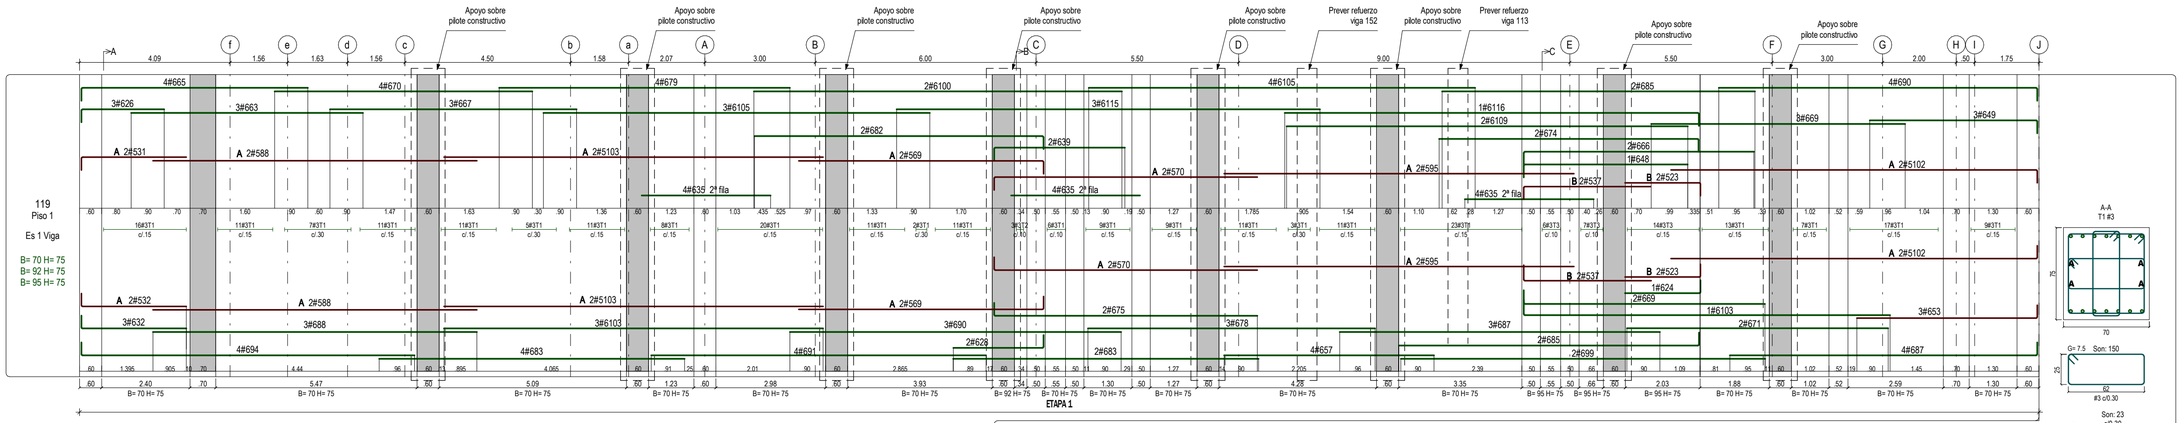

Refuerzo Lateral :
A y B : 4#5, continuas, traslapo mínimo 0.70, gancho estandar a 90° en los extremos, repartidas en ambas caras.
Nota: El refuerzo lateral debe ir colocado en toda la longitud del elemento

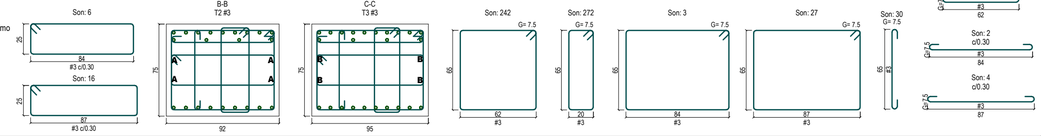

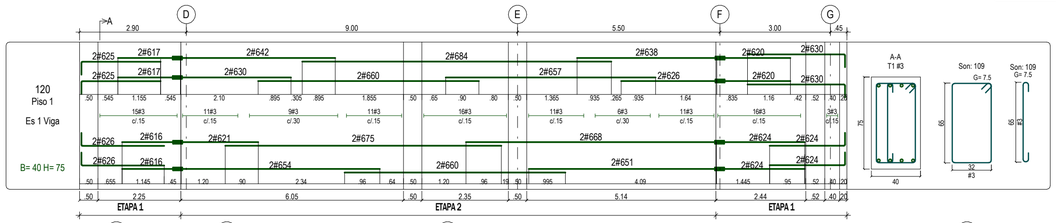

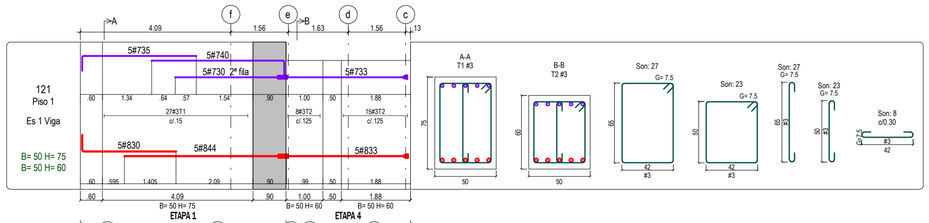

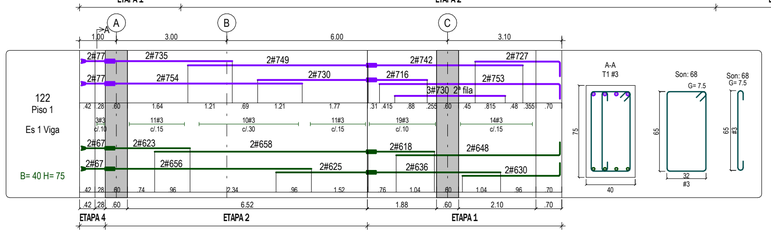

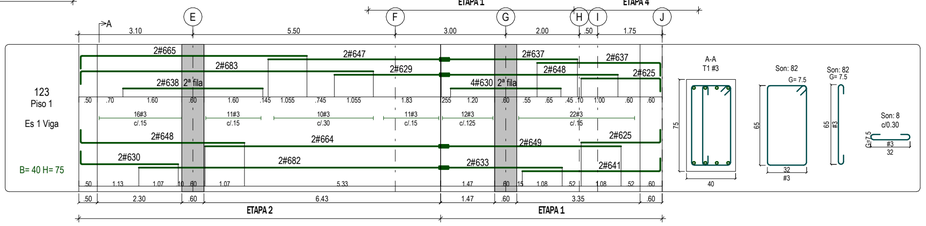

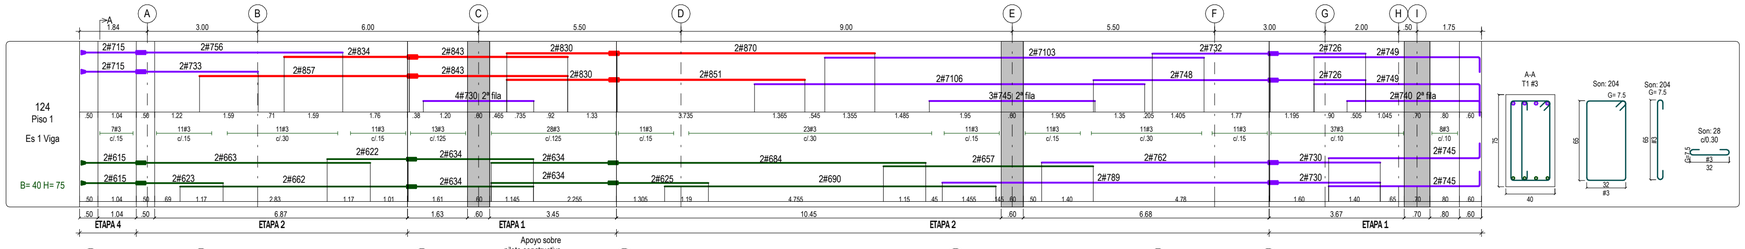

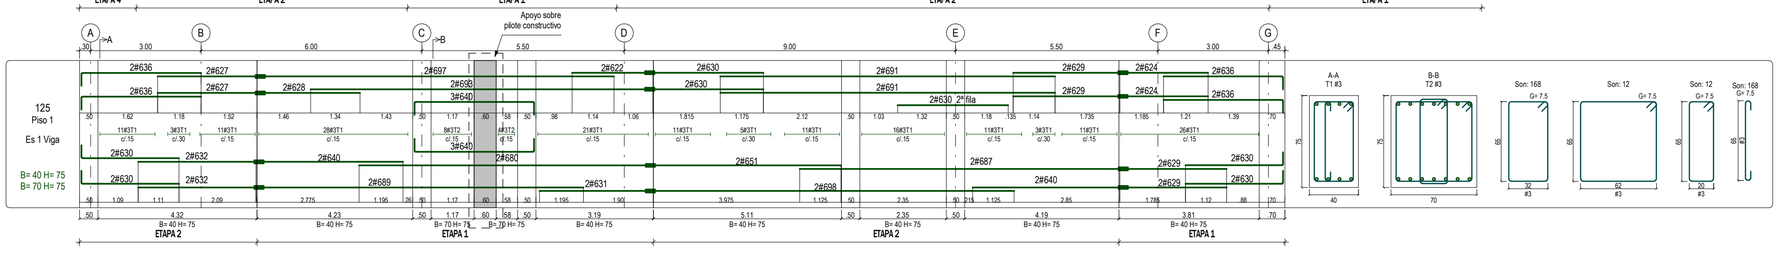

CONVENCIONES

- Indica empalme mecánico
- Indica disco de anclaje (El color depende del diámetro del refuerzo)
- Indica demolición cuidadosa sin conservar el refuerzo

NOTAS

1. Ver detalles generales en PL N° 01.02 y 01.03
2. Ver planta de piso 1 en PL N° 07.00, 07.02, 07.04, 07.06 y 07.08

VERSIÓN : 1

PLANO N° 07.13

Aycardi Estructural

GERENTE DE PROYECTO
LUIS ENRIQUE AYCARDI F.
MAT. 2520212794 CND

INGENIERO
DANIEL E. QUICANO C.

MODELADOR
PAULA ANDREA MONTOYA RENDÓN

MODIFICACIONES	FECHA
Emisión Inicial	13-03-2026

HUMANISE

Circular Lab

HUMANISE STUDIO

EAN-0519- AES-01-EST

Calle 71 #9-84

DESPIECES DE VIGAS PISO 1

EAN-0519 -AES-01-EST-N01-PL-536 07.13

REVISOR ESTRUCTURAL
JULIO CESAR SANMIGUEL CAMACHO
MAT. 25202-57738 CND

PLANO N° 07.13 VERSIÓN : 1