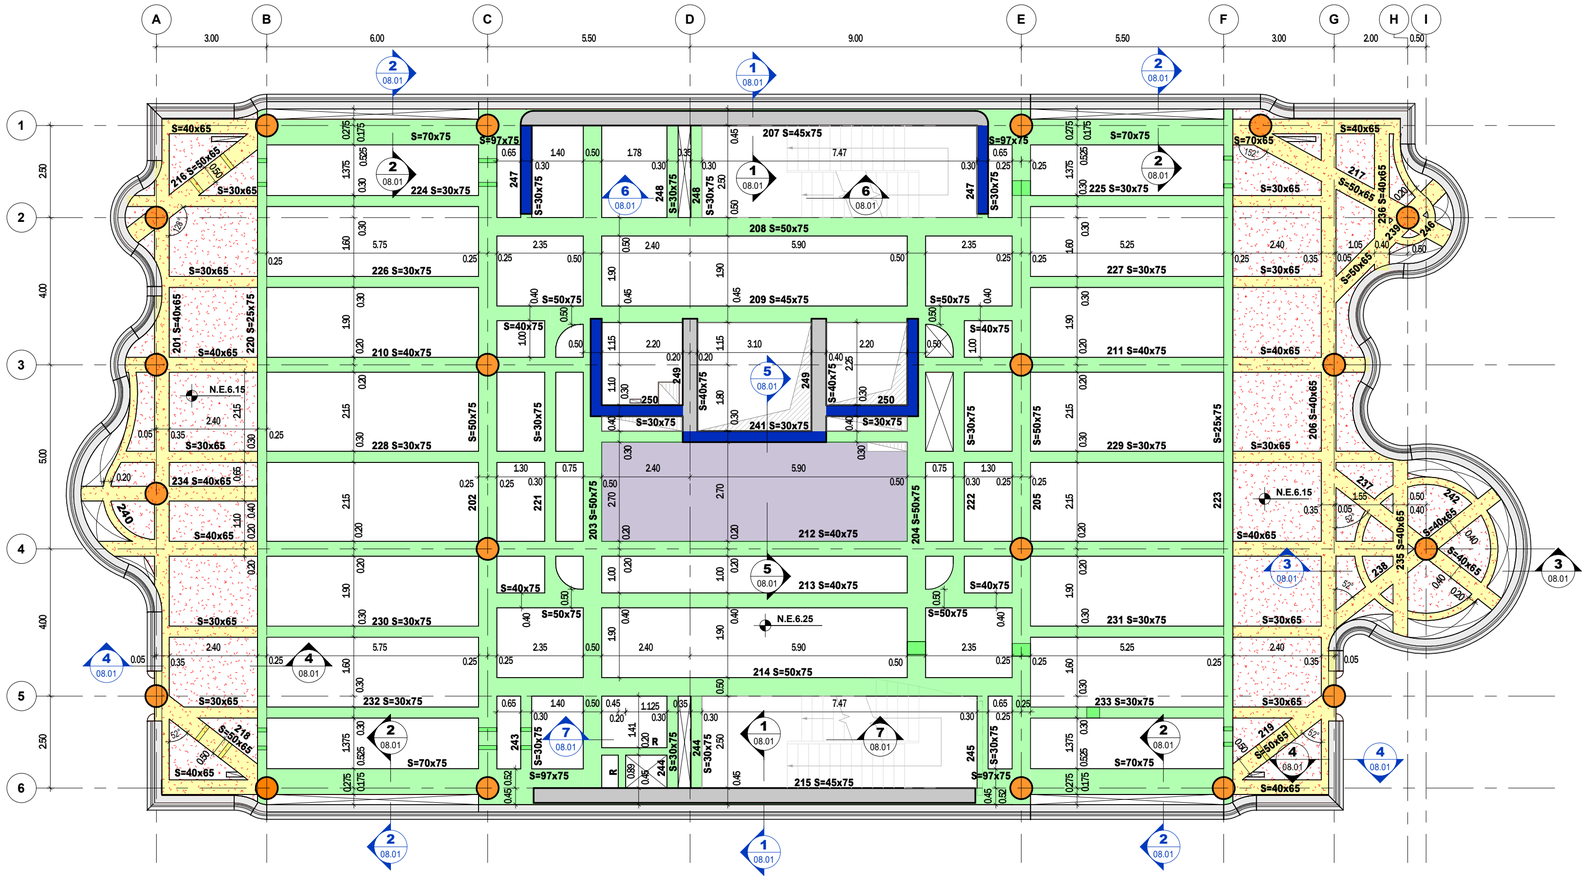

PLANTA DE PISO 2
Escala 1 : 100

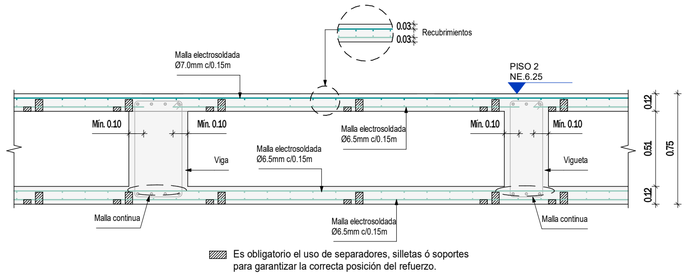

CORTE TÍPICO DE PLACA
Escala 1 : 25

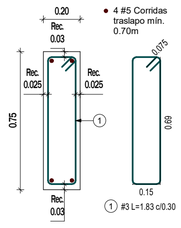

RIOSTRA (R) S=20x75
Escala 1 : 20

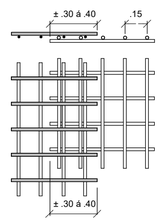

DETALLE TRASLAPO MALLAS
Escala 1 : 25

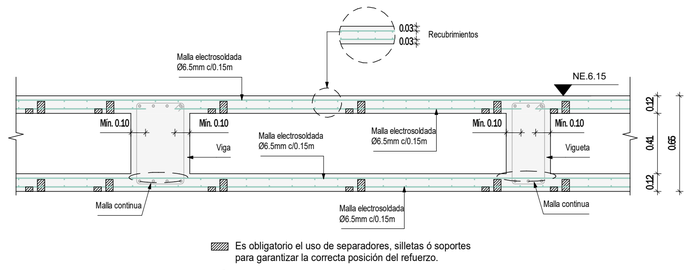

CORTE TÍPICO DE PLACA ZONA BALCONES
Escala 1 : 25

CONCRETO

f'c=35 MPa
f'c=350 kg/cm²
f'c=5000 psi

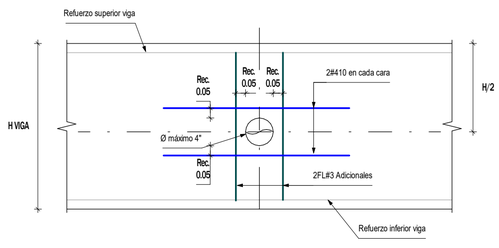

DETALLE PASE EN VIGAS AEREAS
Escala 1 : 20

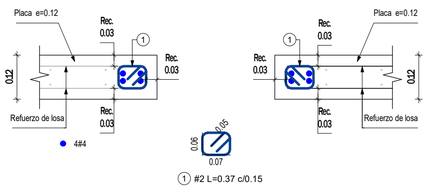

ALZADO REFUERZO ADICIONAL EN DUCTOS
Escala 1 : 10

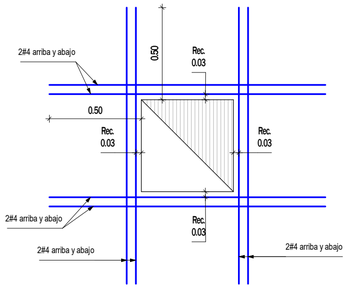

DETALLE TÍPICO REFUERZO ADICIONAL PARA DUCTOS
Escala 1 : 20

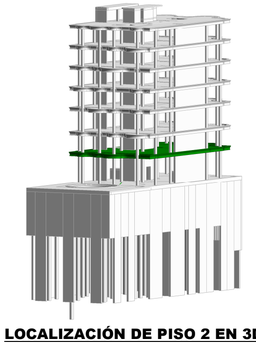

LOCALIZACIÓN DE PISO 2 EN 3D
Escala

CONVENCIONES

- Indica columna S=Ø60
- Indica muro e=30
- Indica muro e=40
- Indica viga h=75
- Indica viga h=65
- Indica pase en viga h=75
- Indica pase en viga h=65
- Indica zona de balcones NE. +6.15 (Ver corte típico zona de balcones)
- Indica zona con refuerzo especial (Ver corte 5 - 5)

NOTAS

1. Ver detalles generales en los PL N° 01.02 y 01.03
2. Ver cortes en el PL N° 08.01
3. Ver esquemas 3D en el PL N° 08.02
4. Ver despieces de vigas en los PL N° 08.03 a 08.06
5. Previo a la fundida del concreto se deben instalar los sistemas de anclaje embebidos para el soporte de los capiteles cerámicos. Ver diseños de ESTAHL.

VERSIÓN : 1

PLANO N° 08.00

Aycardi Estructural

GERENTE DE PROYECTO
LUIS ENRIQUE AYCARDI F.
MAT. 2520212794 CND

INGENIERO
DANIEL E. QUICANO C.

MODELADOR
PAULA ANDREA MONTOYA RENDÓN

MODIFICACIONES	FECHA
Emisión Inicial	13-03-2026

HUMANISE

Circular Lab

HUMANISE STUDIO

EAN-0519- AES-01-EST

Calle 71 #9-84

PLANTA PISO 2

EAN-0519 -AES-01-EST-N02-PL-109 08.00

REVISOR ESTRUCTURAL
JULIO CESAR SANMIGUEL CAMACHO
MAT. 25202-57738 CND

PLANO N° 08.00 VERSIÓN : 1