


**ELEMENTO DE BORDE EN ZONA DE MUROS PISO 5**
**Sin escala**




**CORTE 1 - 1**
**Escala 1 : 25**

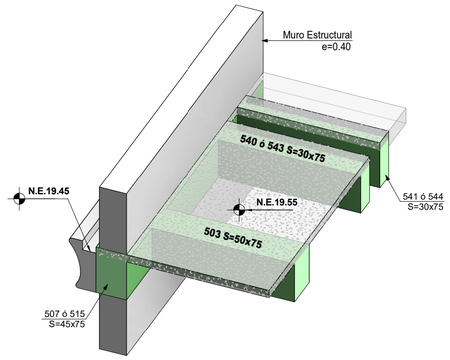


**ZONA DEPRIMIDO PISO 5**
**Sin escala**

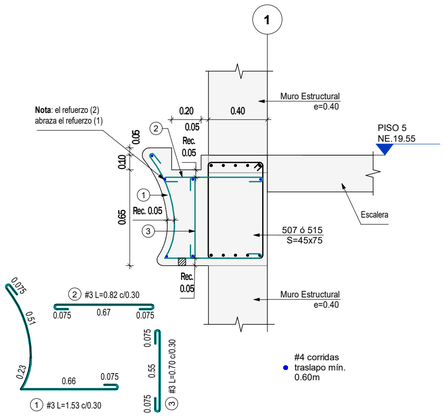


**CORTE 2 - 2**
**Escala 1 : 25**

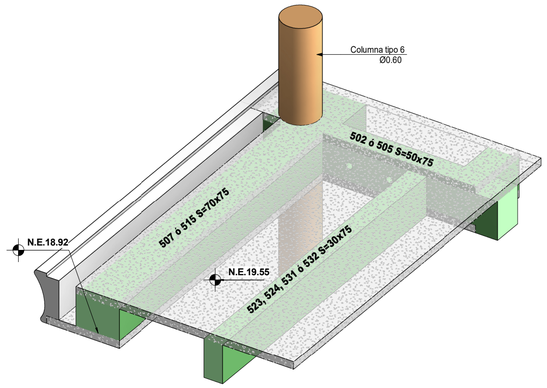


**CORTE 3 - 3**
**Escala 1 : 25**

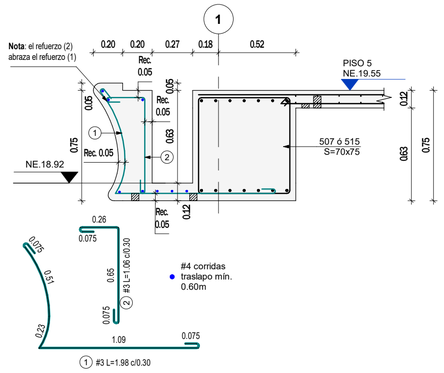


**CORTE 4 - 4**
**Escala 1 : 25**

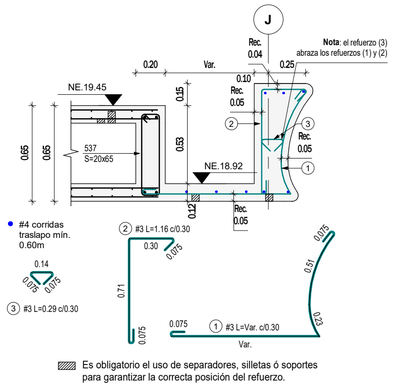


**CORTE 5 - 5**
**Escala 1 : 25**

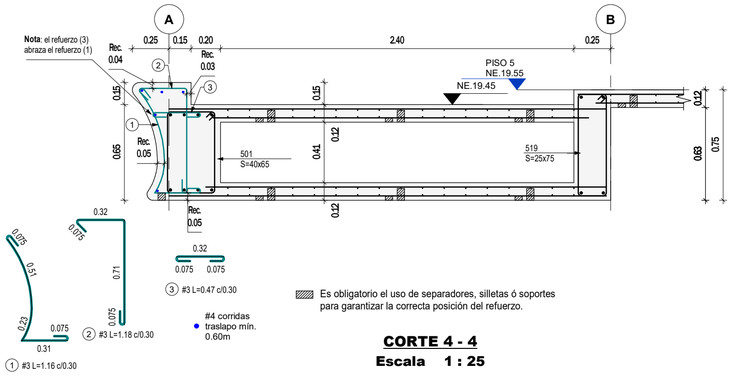


**CORTE 6 - 6**
**Escala 1 : 25**

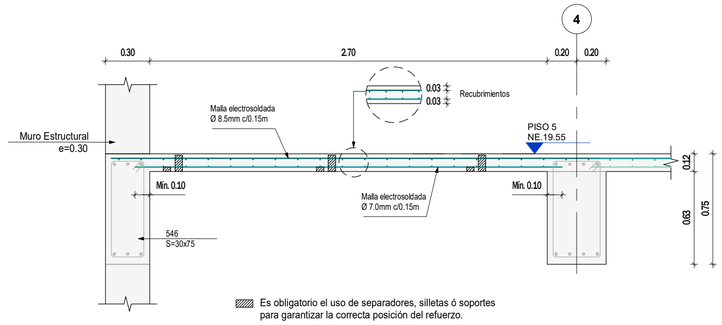


**CORTE 7 - 7**
**Escala 1 : 25**

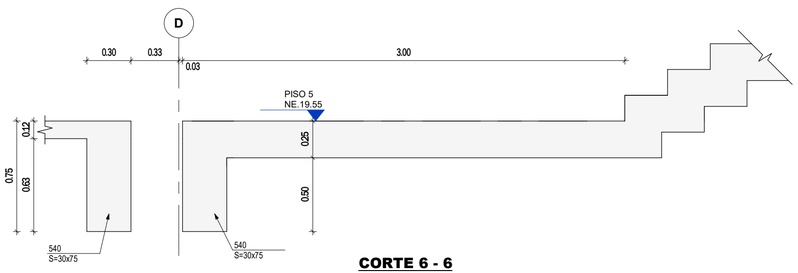


**CORTE 8 - 8**
**Escala 1 : 25**

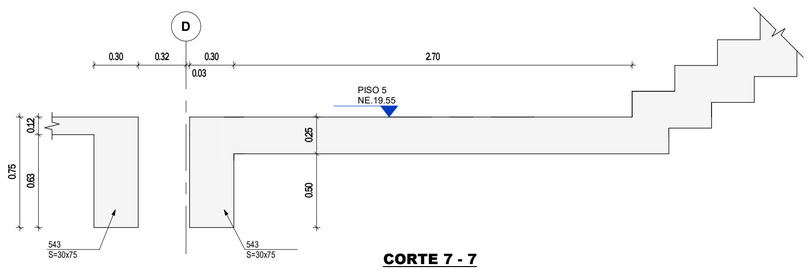


**DETALLE CAPITEL PISO 5**
**Escala 1 : 50**

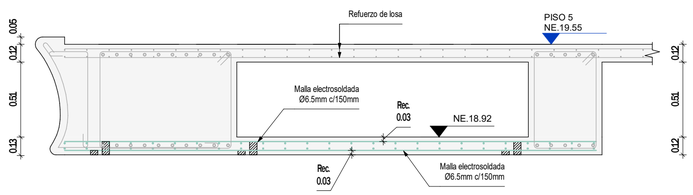


**CORTE A - A PISO 5**
**Escala 1 : 25**

**NOTAS**

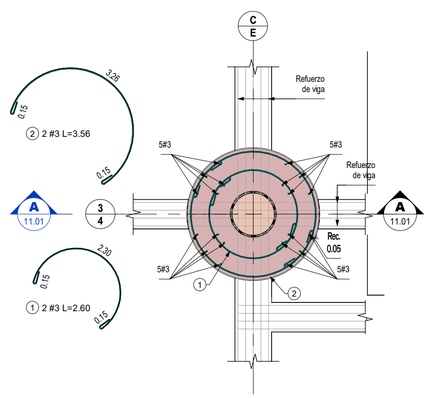1. Ver detalles generales en PL N° 01.02 y 01.03
2. Ver planta de piso 5 en PL N°11.00

VERSIÓN : 1

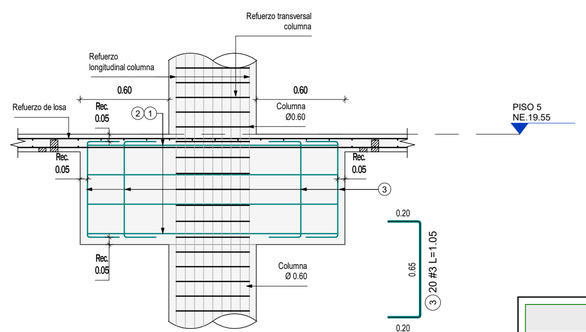PLANO N° 11.01

Aycardi Estructural

GERENTE DE PROYECTO
LUIS ENRIQUE AYCARDI F.
MAT. 2520212794 CND

INGENIERO
DANIEL E. QUICANO C.

MODELADOR
PAULA ANDREA MONTOYA RENDÓN

| MODIFICACIONES | FECHA |
|---|---|
| Emisión Inicial | 13-03-2026 |
| | |
| | |
| | |
| | |
| | |

HUMANISE

Circular Lab

HUMANISE STUDIO

EAN-0519- AES-01-EST

Calle 71 #9-84

CORTE PISO 5

EAN-0519 -AES-01-EST-N05-PL-558 11.01

REVISOR ESTRUCTURAL
JULIO CESAR SANMIGUEL CAMACHO
MAT. 25202-57738 CND

PLANO N° 11.01 VERSIÓN : 1