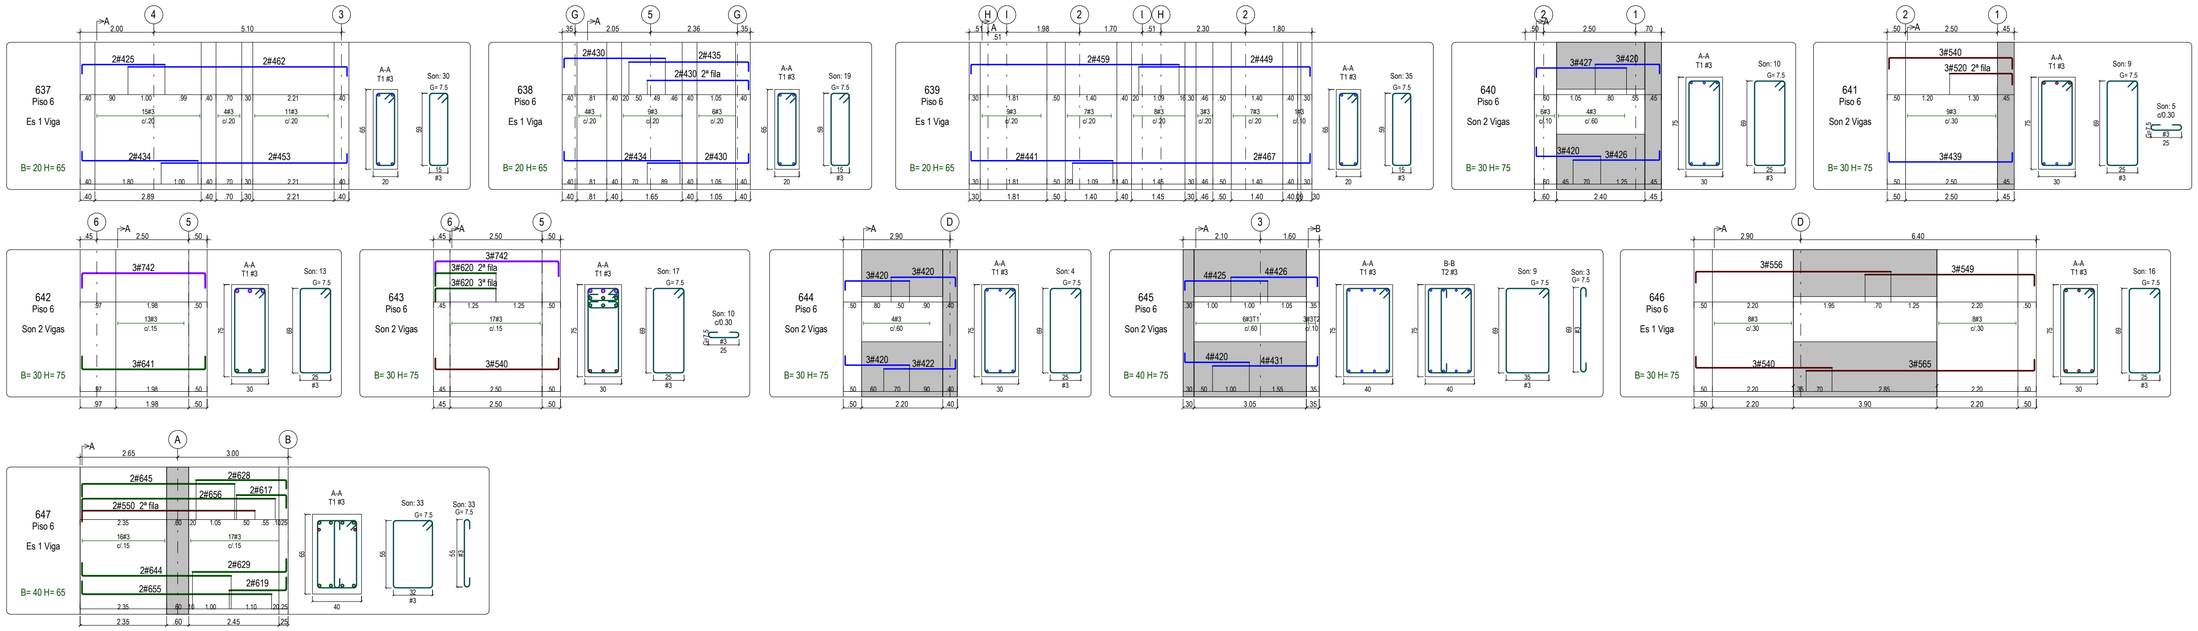


**NOTAS**

1. Ver detalles generales en PL N° 01.02 y 01.03
2. Ver planta de piso 6 en PL N° 12.06

VERSIÓN : 1

PLANO N° 12.06

Aycardi Estructural

GERENTE DE PROYECTO
LUIS ENRIQUE AYCARDI F.
**MAT. 2520212794 CND**

INGENIERO
DANIEL E. QUICANO C.

MODELADOR
PAULA ANDREA MONTOYA RENDÓN

| MODIFICACIONES | FECHA |
|---|---|
| Emisión Inicial | 13-03-2026 |
| | |
| | |
| | |
| | |
| | |

HUMANISE

Circular Lab

**HUMANISE STUDIO**

EAN-0519- AES-01-EST

Calle 71 #9-84

**DESPIECE DE VIGAS PISO 6**

EAN-0519 -AES-01-EST-N06-PL-569 12.06

REVISOR ESTRUCTURAL
JULIO CESAR SANMIGUEL CAMACHO
MAT. 25202-57738 CND

PLANO N° 12.06 VERSIÓN : 1