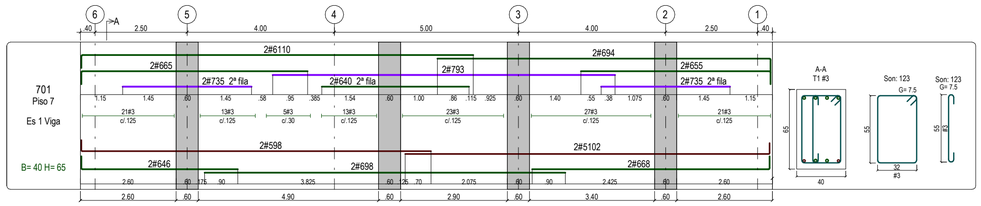

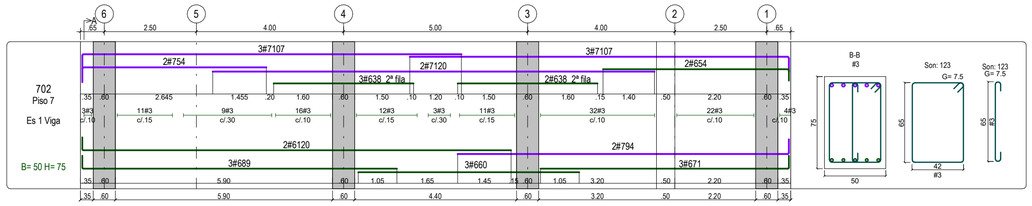

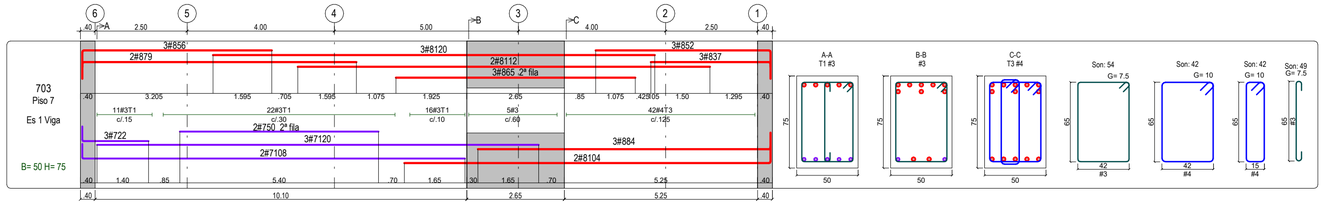

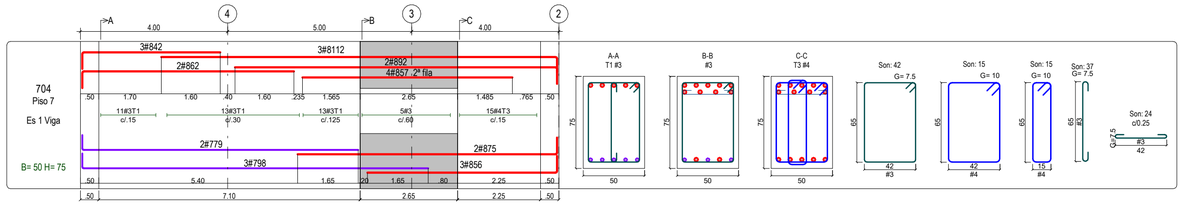

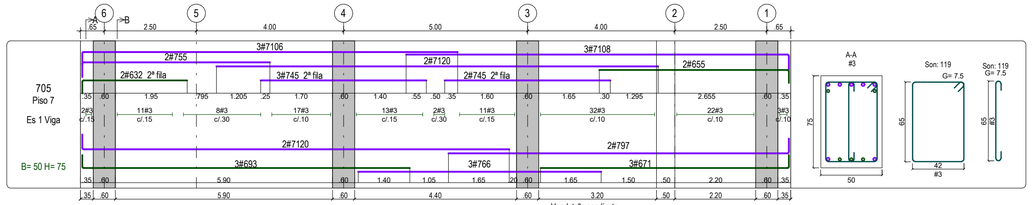

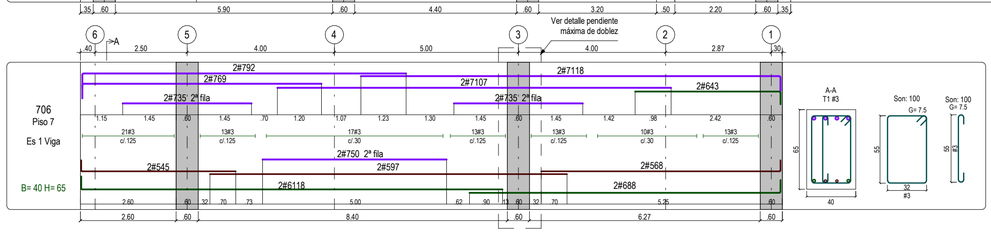

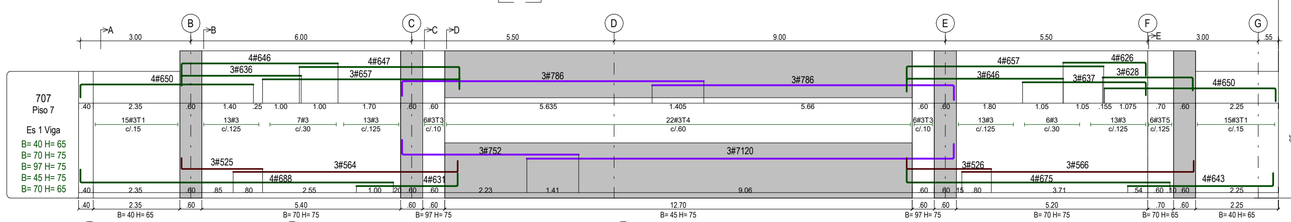

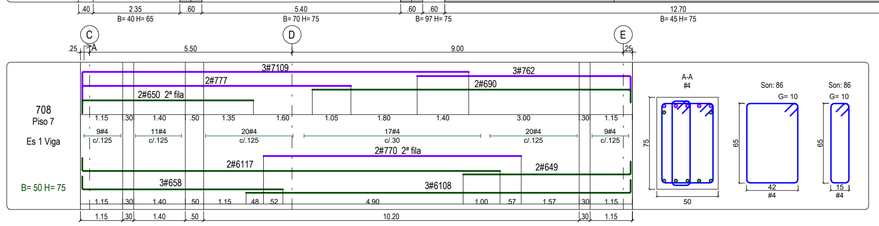

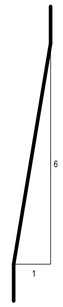

*No aplica para vigas circulares

DETALLE PENDIENTE MÁXIMA PARA DOBLEZ EN VARILLA EN CAMBIO DE SECCIÓN

Escala 1 : 10

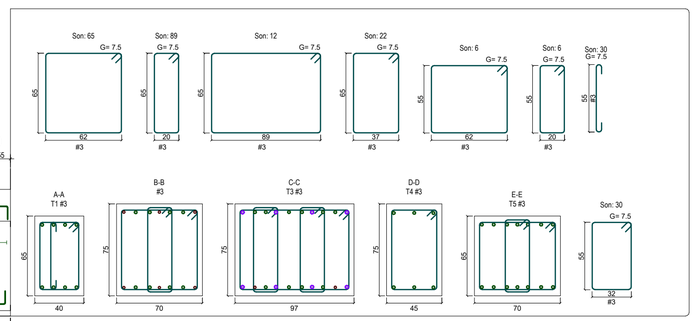

NOTAS

1. Ver detalles generales en PL N° 01.02 y 01.03
2. Ver planta de piso 7 en PL N° 13.00

VERSIÓN : 1

PLANO N° 13.03

Aycardi Estructural

GERENTE DE PROYECTO
LUIS ENRIQUE AYCARDI F.
MAT. 2520212794 CND

INGENIERO
DANIEL E. QUICANO C.

MODELADOR
PAULA ANDREA MONTOYA RENDÓN

MODIFICACIONES	FECHA
Emisión Inicial	13-03-2026

HUMANISE

Circular Lab

HUMANISE STUDIO

EAN-0519- AES-01-EST

Calle 71 #9-84

DESPIECE DE VIGAS PISO 7

EAN-0519 -AES-01-EST-N07-PL-572 13.03

REVISOR ESTRUCTURAL
JULIO CESAR SANMIGUEL CAMACHO
MAT. 25202-57738 CND

PLANO N° 13.03 VERSIÓN : 1