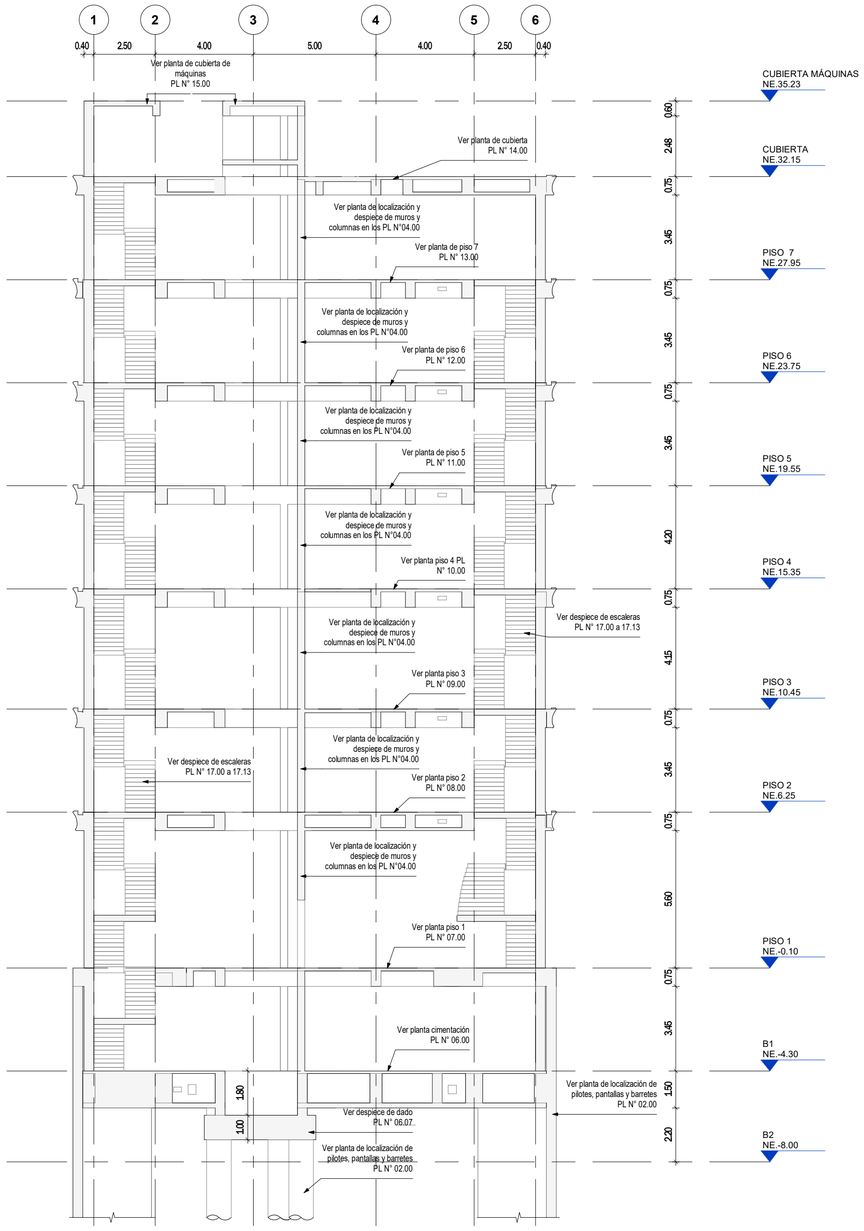

CORTE TRANSVERSAL
Escala 1 : 150

ÍNDICE DE PLANOS ESTRUCTURALES

PLANO N°	ARCHIVO DIGITAL	CONTENIDO	VERSIÓN
01.00	EAN-0519-AES-01-EST-PL-601-01.00	ESQUEMA 3D Y ESPECIFICACIONES	1
01.01	EAN-0519-AES-01-EST-PL-201-01.01	CORTE ESQUEMATICO E INDICE DE PLANOS	1
01.02	EAN-0519-AES-01-EST-PL-501-01.02	DETALLE GENERALES	1
01.03	EAN-0519-AES-01-EST-PL-502-01.03	DETALLE GENERALES	1
02.00	EAN-0519-AES-01-EST-CIM-PL-101-02.00	PLANTA LOCALIZACIÓN DE PILOTES, PANTALLAS Y BARRETES	1
02.01	EAN-0519-AES-01-EST-CIM-PL-503-02.01	DESPIECE DE PANTALLAS	1
02.02	EAN-0519-AES-01-EST-CIM-PL-504-02.02	DESPIECE DE PILOTES	1
02.03	EAN-0519-AES-01-EST-CIM-PL-505-02.03	DESPIECE DE PILOTES CONSTRUCTIVOS	1
02.04	EAN-0519-AES-01-EST-CIM-PL-506-02.04	DESPIECE DE BARRETES	1
02.05	EAN-0519-AES-01-EST-CIM-PL-507-02.05	DESPIECE DE BARRETES	1
03.00	EAN-0519-AES-01-EST-CIM-PL-202-03.00	SECUENCIA DE PROCESO CONSTRUCTIVO PASO 1	1
03.01	EAN-0519-AES-01-EST-CIM-PL-203-03.01	SECUENCIA PROCESO CONSTRUCTIVO PASO 2	1
03.02	EAN-0519-AES-01-EST-CIM-PL-204-03.02	SECUENCIA PROCESO CONSTRUCTIVO PASO 3	1
03.03	EAN-0519-AES-01-EST-CIM-PL-205-03.03	SECUENCIA PROCESO CONSTRUCTIVO PASO 4	1
03.04	EAN-0519-AES-01-EST-CIM-PL-206-03.04	SECUENCIA PROCESO CONSTRUCTIVO PASO 5	1
03.05	EAN-0519-AES-01-EST-CIM-PL-207-03.05	SECUENCIA PROCESO CONSTRUCTIVO PASO 6	1
03.06	EAN-0519-AES-01-EST-CIM-PL-208-03.06	SECUENCIA PROCESO CONSTRUCTIVO PASO 7	1
03.07	EAN-0519-AES-01-EST-CIM-PL-209-03.07	SECUENCIA PROCESO CONSTRUCTIVO PASO 8	1
03.08	EAN-0519-AES-01-EST-CIM-PL-210-03.08	SECUENCIA PROCESO CONSTRUCTIVO PASO 9	1
03.09	EAN-0519-AES-01-EST-CIM-PL-211-03.09	SECUENCIA PROCESO CONSTRUCTIVO PASO 10	1
03.10	EAN-0519-AES-01-EST-CIM-PL-212-03.10	SECUENCIA PROCESO CONSTRUCTIVO PASO 11	1
03.11	EAN-0519-AES-01-EST-CIM-PL-213-03.11	SECUENCIA PROCESO CONSTRUCTIVO PASO 12	1
04.00	EAN-0519-AES-01-EST-PL-102-04.00	PLANTA LOCALIZACIÓN DE MUROS Y COLUMNAS	1

ÍNDICE DE PLANOS ESTRUCTURALES

PLANO N°	ARCHIVO DIGITAL	CONTENIDO	VERSIÓN
04.01	EAN-0519-AES-01-EST-PL-508-04.01	DESPIECE DE COLUMNAS	1
04.02	EAN-0519-AES-01-EST-PL-509-04.02	DESPIECE DE COLUMNAS	1
04.03	EAN-0519-AES-01-EST-PL-510-04.03	DESPIECE DE COLUMNAS	1
04.04	EAN-0519-AES-01-EST-PL-511-04.04	DESPIECE DE COLUMNAS	1
04.05	EAN-0519-AES-01-EST-PL-512-04.05	DESPIECE MURO TIPO 1	1
04.06	EAN-0519-AES-01-EST-PL-513-04.06	DESPIECE MURO TIPO 2	1
04.07	EAN-0519-AES-01-EST-PL-514-04.07	DESPIECE MUROS TIPO 3 Y 4	1
05.00	EAN-0519-AES-01-EST-PL-515-05.00	DETALLES ANFITEATRO	1
05.01	EAN-0519-AES-01-EST-PL-516-05.01	DETALLES ANFITEATRO	1
05.02	EAN-0519-AES-01-EST-PL-516-05.02	DETALLES ANFITEATRO	1
05.03	EAN-0519-AES-01-EST-PL-516-05.03	DETALLES ANFITEATRO	1
06.00	EAN-0519-AES-01-EST-PL-103-06.00	PLANTA DE CIMENTACIÓN	1
06.01	EAN-0519-AES-01-EST-CIM-PL-519-06.01	ESQUEMAS 3D CIMENTACIÓN	1
06.02	EAN-0519-AES-01-EST-CIM-PL-520-06.02	CORTES Y ESQUEMAS 3D	1
06.03	EAN-0519-AES-01-EST-CIM-PL-521-06.03	DESPIECES DE VIGAS DE CIMENTACIÓN	1
06.04	EAN-0519-AES-01-EST-CIM-PL-522-06.04	DESPIECES DE VIGAS DE CIMENTACIÓN	1
06.05	EAN-0519-AES-01-EST-CIM-PL-523-06.05	DESPIECES DE VIGAS DE CIMENTACIÓN	1
06.06	EAN-0519-AES-01-EST-CIM-PL-524-06.06	DESPIECES DE VIGAS DE CIMENTACIÓN	1
06.07	EAN-0519-AES-01-EST-CIM-PL-525-06.07	DESPIECES DE VIGAS DE CIMENTACIÓN	1
06.08	EAN-0519-AES-01-EST-CIM-PL-526-06.08	DESPIECE DE DADOS	1
06.09	EAN-0519-AES-01-EST-CIM-PL-527-06.09	DESPIECE DE DADOS	1
07.00	EAN-0519-AES-01-EST-N01-PL-104-07.00	PLANTA DE PISO 1 ETAPA 1 (ANILLO)	1
07.01	EAN-0519-AES-01-EST-N01-PL-528-07.01	CORTES Y ESQUEMA 3D PISO 1 ETAPA 1 (ANILLO)	1
07.02	EAN-0519-AES-01-EST-N01-PL-105-07.02	PLANTA DE PISO 1 ETAPA 2 (COMPLEMENTO)	1
07.03	EAN-0519-AES-01-EST-N01-PL-529-07.03	CORTES Y ESQUEMA 3D PISO 1 ETAPA 2 (COMPLEMENTO)	1
07.04	EAN-0519-AES-01-EST-N01-PL-106-07.04	PLANTA DE PISO 1 ETAPA 3 (DEMOLICIÓN)	1
07.05	EAN-0519-AES-01-EST-N01-PL-530-07.05	CORTES Y ESQUEMA 3D PISO 1 ETAPA 3 (DEMOLICIÓN)	1
07.06	EAN-0519-AES-01-EST-N01-PL-107-07.06	PLANTA DE PISO 1 ETAPA 4 (COMPLEMENTO ANFITEATRO)	1
07.07	EAN-0519-AES-01-EST-N01-PL-531-07.07	ESQUEMA 3D PISO 1 ETAPA 4 (COMPLEMENTO ANFITEATRO)	1
07.08	EAN-0519-AES-01-EST-N01-PL-108-07.08	PLANTA DE PISO 1 ETAPA 5 (DEFINITIVA)	1
07.09	EAN-0519-AES-01-EST-N01-PL-532-07.09	CORTES Y ESQUEMA 3D PISO 1 (DEFINITIVA)	1
07.10	EAN-0519-AES-01-EST-N01-PL-533-07.10	DETALLES CERCHA PISO 1	1
07.11	EAN-0519-AES-01-EST-N01-PL-534-07.11	DESPIECES DE VIGAS PISO 1	1
07.12	EAN-0519-AES-01-EST-N01-PL-535-07.12	DESPIECES DE VIGAS PISO 1	1
07.13	EAN-0519-AES-01-EST-N01-PL-536-07.13	DESPIECES DE VIGAS PISO 1	1
07.14	EAN-0519-AES-01-EST-N01-PL-537-07.14	DESPIECES DE VIGAS PISO 1	1
07.15	EAN-0519-AES-01-EST-N01-PL-538-07.15	DESPIECES DE VIGAS PISO 1	1
07.16	EAN-0519-AES-01-EST-N01-PL-539-07.16	DESPIECES DE VIGAS PISO 1	1
08.00	EAN-0519-AES-01-EST-N02-PL-109-08.00	PLANTA PISO 2	1
08.01	EAN-0519-AES-01-EST-N02-PL-540-08.01	CORTES PISO 2	1
08.02	EAN-0519-AES-01-EST-N02-PL-541-08.02	ESQUEMAS 3D PISO 2	1
08.03	EAN-0519-AES-01-EST-N02-PL-542-08.03	DESPIECE DE VIGAS PISO 2	1
08.04	EAN-0519-AES-01-EST-N02-PL-543-08.04	DESPIECE DE VIGAS PISO 2	1
08.05	EAN-0519-AES-01-EST-N02-PL-544-08.05	DESPIECE DE VIGAS PISO 2	1
08.06	EAN-0519-AES-01-EST-N02-PL-545-08.06	DESPIECE DE VIGAS PISO 2	1
09.00	EAN-0519-AES-01-EST-N03-PL-110-09.00	PLANTA PISO 3	1
09.01	EAN-0519-AES-01-EST-N03-PL-546-09.01	CORTES PISO 3	1
09.02	EAN-0519-AES-01-EST-N03-PL-547-09.02	ESQUEMAS 3D PISO 3	1
09.03	EAN-0519-AES-01-EST-N03-PL-548-09.03	DESPIECE DE VIGAS PISO 3	1
09.04	EAN-0519-AES-01-EST-N03-PL-549-09.04	DESPIECE DE VIGAS PISO 3	1
09.05	EAN-0519-AES-01-EST-N03-PL-550-09.05	DESPIECE DE VIGAS PISO 3	1
09.06	EAN-0519-AES-01-EST-N03-PL-551-09.06	DESPIECE DE VIGAS PISO 3	1
10.00	EAN-0519-AES-01-EST-N04-PL-111-10.00	PLANTA PISO 4	1
10.01	EAN-0519-AES-01-EST-N04-PL-552-10.01	CORTES PISO 4	1
10.02	EAN-0519-AES-01-EST-N04-PL-553-10.02	ESQUEMAS 3D PISO 4	1
10.03	EAN-0519-AES-01-EST-N04-PL-554-10.03	DESPIECE DE VIGAS PISO 4	1
10.04	EAN-0519-AES-01-EST-N04-PL-555-10.04	DESPIECE DE VIGAS PISO 4	1
10.05	EAN-0519-AES-01-EST-N04-PL-556-10.05	DESPIECE DE VIGAS PISO 4	1
10.06	EAN-0519-AES-01-EST-N04-PL-557-10.06	DESPIECE DE VIGAS PISO 4	1
11.00	EAN-0519-AES-01-EST-N05-PL-112-11.00	PLANTA DE PISO 5	1
11.01	EAN-0519-AES-01-EST-N05-PL-558-11.01	CORTE PISO 5	1
11.02	EAN-0519-AES-01-EST-N05-PL-559-11.02	ESQUEMAS 3D PISO 5	1
11.03	EAN-0519-AES-01-EST-N05-PL-560-11.03	DESPIECE DE VIGAS PISO 5	1
11.04	EAN-0519-AES-01-EST-N05-PL-561-11.04	DESPIECE DE VIGAS PISO 5	1
11.05	EAN-0519-AES-01-EST-N05-PL-562-11.05	DESPIECE DE VIGAS PISO 5	1
11.06	EAN-0519-AES-01-EST-N05-PL-563-11.06	DESPIECE DE VIGAS PISO 5	1
12.00	EAN-0519-AES-01-EST-N06-PL-113-12.00	PLANTA DE PISO 6	1
12.01	EAN-0519-AES-01-EST-N06-PL-564-12.01	CORTES PISO 6	1
12.02	EAN-0519-AES-01-EST-N06-PL-565-12.02	ESQUEMAS 3D PISO 6	1
12.03	EAN-0519-AES-01-EST-N06-PL-566-12.03	DESPIECE DE VIGAS PISO 6	1
12.04	EAN-0519-AES-01-EST-N06-PL-567-12.04	DESPIECE DE VIGAS PISO 6	1
12.05	EAN-0519-AES-01-EST-N06-PL-568-12.05	DESPIECE DE VIGAS PISO 6	1
12.06	EAN-0519-AES-01-EST-N06-PL-569-12.06	DESPIECE DE VIGAS PISO 6	1
13.00	EAN-0519-AES-01-EST-N07-PL-114-13.00	PLANTA DE PISO 7	1
13.01	EAN-0519-AES-01-EST-N07-PL-570-13.01	CORTES PISO 7	1
13.02	EAN-0519-AES-01-EST-N07-PL-571-13.02	ESQUEMAS 3D PISO 7	1
13.03	EAN-0519-AES-01-EST-N07-PL-572-13.03	DESPIECE DE VIGAS PISO 7	1
13.04	EAN-0519-AES-01-EST-N07-PL-573-13.04	DESPIECE DE VIGAS PISO 7	1
13.05	EAN-0519-AES-01-EST-N07-PL-574-13.05	DESPIECE DE VIGAS PISO 7	1
14.00	EAN-0519-AES-01-EST-CUB-PL-115-14.00	PLANTA DE CUBIERTA	1
14.01	EAN-0519-AES-01-EST-CUB-PL-575-14.01	CORTES Y ESQUEMAS 3D CUBIERTA	1
14.02	EAN-0519-AES-01-EST-CUB-PL-576-14.02	PLANTA DE LOCALIZACIÓN DE PUNTOS DE ANCLAJE Y DUCTOS DE CUBIERTA	1
14.03	EAN-0519-AES-01-EST-CUB-PL-577-14.03	DESPIECE DE VIGAS CUBIERTA	1
14.04	EAN-0519-AES-01-EST-CUB-PL-578-14.04	DESPIECE DE VIGAS CUBIERTA	1
14.05	EAN-0519-AES-01-EST-CUB-PL-579-14.05	DESPIECE DE VIGAS CUBIERTA	1
14.06	EAN-0519-AES-01-EST-CUB-PL-580-14.06	PLANTA Y CORTES ASCENSOR MONTALIBROS	1
15.00	EAN-0519-AES-01-EST-SCU-PL-116-15.00	PLANTA DE CUBIERTA DE MÁQUINAS	1
15.01	EAN-0519-AES-01-EST-SCU-PL-581-15.01	CORTE Y ESQUEMA 3D CUBIERTA DE MÁQUINAS	1
15.02	EAN-0519-AES-01-EST-SCU-PL-582-15.02	DESPIECE DE VIGAS DE CUBIERTA DE MAQUINAS	1
16.00	EAN-0519-AES-01-EST-B2-PL-118-16.00	PLANTA TANQUE DE AGUA	1
16.01	EAN-0519-AES-01-EST-B2-PL-583-16.01	CORTES TANQUE DE AGUA	1
16.02	EAN-0519-AES-01-EST-B2-PL-584-16.02	DESPIECES VIGAS DE CIMENTACIÓN TANQUE DE AGUA	1
16.03	EAN-0519-AES-01-EST-B1-PL-585-16.03	PLANTA Y CORTE TANQUE DE AGUA ENTRE EJES 1 Y 2	1
16.04	EAN-0519-AES-01-EST-B1-PL-586-16.04	CORTES TANQUE DE AGUA ENTRE EJES 1 Y 2	1
16.05	EAN-0519-AES-01-EST-B1-PL-587-16.05	PLANTA Y CORTE TANQUE DE AGUA ENTRE EJES 5 Y 6	1
16.06	EAN-0519-AES-01-EST-B1-PL-588-16.06	CORTE TANQUE DE AGUA ENTRE EJES 5 Y 6	1
16.07	EAN-0519-AES-01-EST-B1-PL-589-16.07	POZO EYECTOR TIPO 1	1
16.08	EAN-0519-AES-01-EST-B1-PL-590-16.08	POZO EYECTOR TIPO 2	1
16.09	EAN-0519-AES-01-EST-B1-PL-591-16.09	POZO EYECTOR TIPO 3	1
17.00	EAN-0519-AES-01-EST-PL-592-17.00	DESPIECE DE ESCALERA TIPO 1 DE CIMENTACIÓN A PISO 1	1
17.01	EAN-0519-AES-01-EST-PL-593-17.01	DESPIECE DE ESCALERA TIPO 1 DE CIMENTACIÓN A PISO 1	1
17.02	EAN-0519-AES-01-EST-PL-594-17.02	DESPIECE DE ESCALERA TIPO 1 DE PISO 1 A PISO 2	1
17.03	EAN-0519-AES-01-EST-PL-595-17.03	DESPIECE DE ESCALERA TIPO 1 DE PISO 1 A PISO 2	1
17.04	EAN-0519-AES-01-EST-PL-596-17.04	DESPIECE DE ESCALERA TIPO 1 TÍPICA PISOS (2 Y 4 A CUBIERTA)	1
17.05	EAN-0519-AES-01-EST-PL-597-17.05	DESPIECE DE ESCALERA TIPO 1 TÍPICA PISOS (2 Y 4 A CUBIERTA)	1
17.06	EAN-0519-AES-01-EST-PL-598-17.06	DESPIECE DE ESCALERA TIPO 1 DE PISO 3 A PISO 4	1
17.07	EAN-0519-AES-01-EST-PL-599-17.07	DESPIECE DE ESCALERA TIPO 1 DE PISO 3 A PISO 4	1
17.08	EAN-0519-AES-01-EST-PL-5100-17.08	DESPIECE DE ESCALERA TIPO 2 PISO 1 A PISO 2	1
17.09	EAN-0519-AES-01-EST-PL-5101-17.09	DESPIECE DE ESCALERA TIPO 2 PISO 1 A PISO 2	1
17.10	EAN-0519-AES-01-EST-PL-5102-17.10	DESPIECE DE ESCALERA TIPO 2 TÍPICA PISOS (2 Y 4 A CUBIERTA)	1
17.11	EAN-0519-AES-01-EST-PL-5103-17.11	DESPIECE DE ESCALERA TIPO 2 PISO 2 A PISO 3	1
17.12	EAN-0519-AES-01-EST-PL-5104-17.12	DESPIECE DE ESCALERA TIPO 2 PISO 3 A PISO 4	1
17.13	EAN-0519-AES-01-EST-PL-5105-17.13	DESPIECE DE ESCALERA TIPO 2 PISO 3 A PISO 4	1
18.00	EAN-0519-AES-01-EST-PL-5106-18.00	DETALLES DE MUROS NO ESTRUCTURALES	1
18.01	EAN-0519-AES-01-EST-PL-5107-18.01	DETALLES DE ELEMENTOS NO ESTRUCTURALES	1
18.02	EAN-0519-AES-01-EST-PL-5108-18.02	DETALLES DE MUROS NO ESTRUCTURALES	1

VERSIÓN : 1

PLANO N° 01.01

Aycardi Estructural

GERENTE DE PROYECTO
LUIS ENRIQUE AYCARDI F.
MAT. 2520212794 CND

INGENIERO
DANIEL E. QUICANO C.

MODELADOR
JUAN MANUEL SANTOS

MODIFICACIONES	FECHA
Emisión Inicial	13-03-2026

HUMANISE

Circular Lab

HUMANISE STUDIO

EAN-0519- AES-01-EST

Calle 71 #9-84

CORTE ESQUEMATICO E INDICE DE PLANOS

EAN-0519 -AES-01-EST-PL-201 01.01

REVISOR ESTRUCTURAL
JULIO CESAR SANMIGUEL CAMACHO
MAT. 25202-57738 CND

PLANO N° 01.01 VERSIÓN : 1