COLUMNA TIPO 1
Son 2
ESC gen. 1:100
ESC secc. 1:25






**LOCALIZACIÓN DE COLUMNA TIPO 1 EN 3D**

**Sin escala**

De B1 a Cubierta

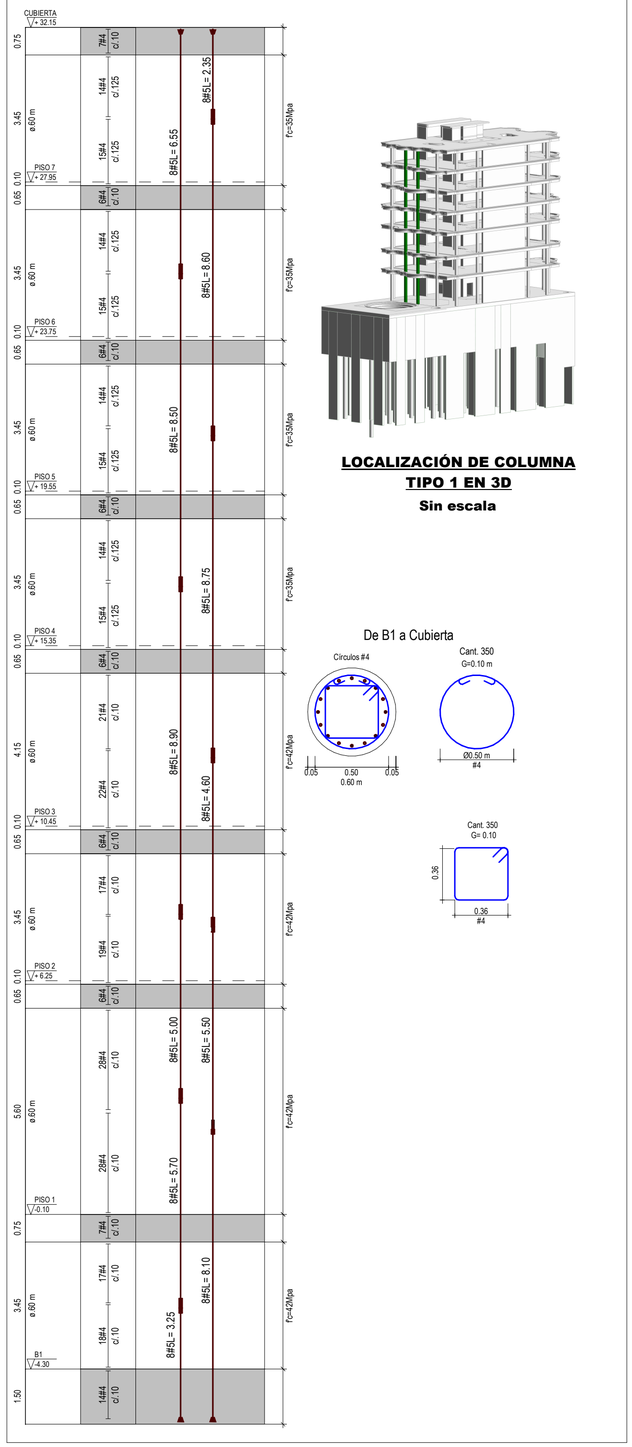


COLUMNA TIPO 2
Es 1
ESC gen. 1:100
ESC secc. 1:25






**LOCALIZACIÓN DE COLUMNA TIPO 2 EN 3D**

**Sin escala**

De B1 a Cubierta

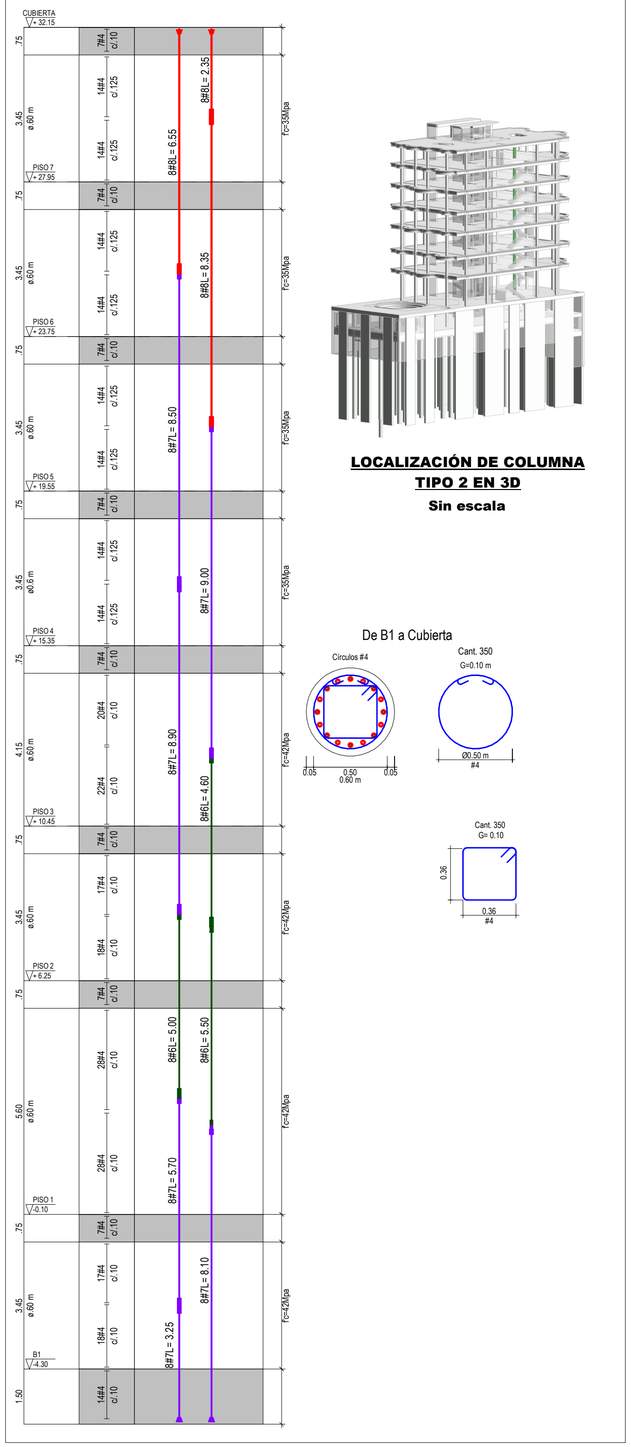


COLUMNA TIPO 2A
Es 1
ESC gen. 1:100
ESC secc. 1:25






**LOCALIZACIÓN DE COLUMNA TIPO 2A EN 3D**

**Sin escala**

De B1 a Cubierta

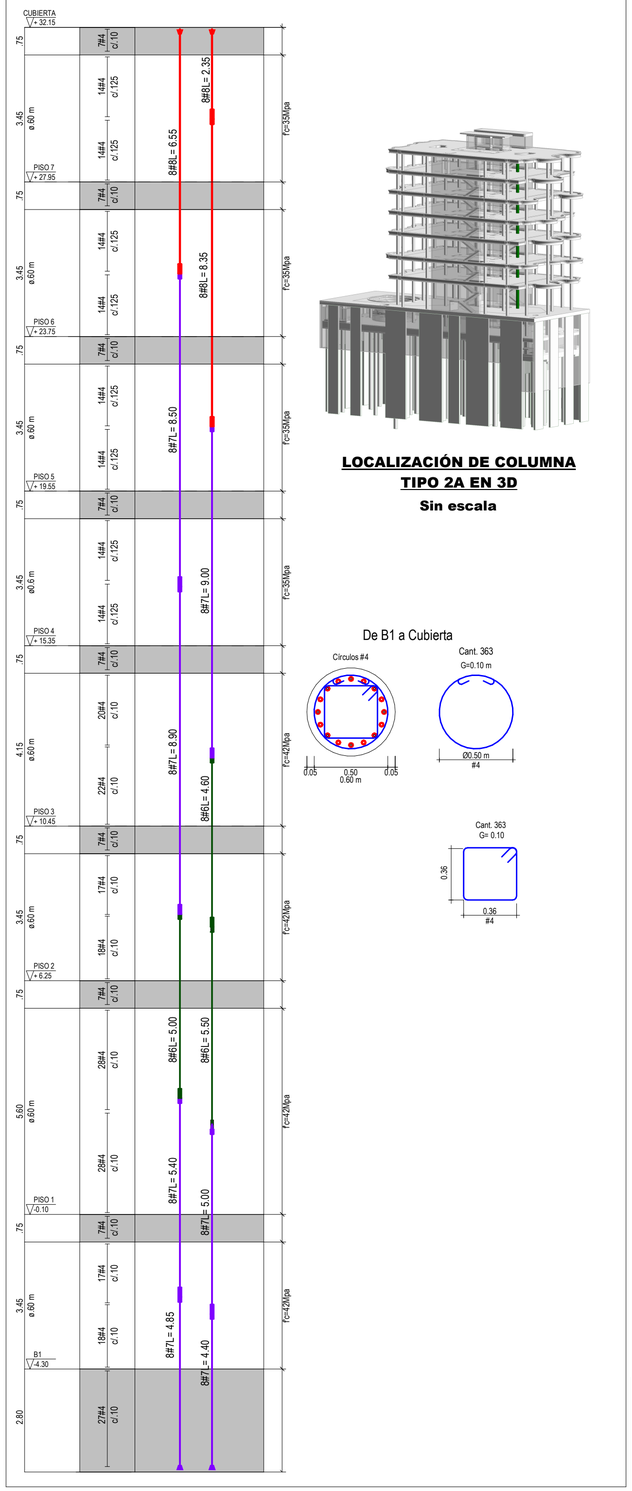


**CONVENCIONES**

Indica disco de anclaje
Indica empalme mecánico

**NOTAS**

1. Ver detalles generales en plano PL N° 01.02 y 01.03
2. Ver planta localización e identificación de muros y columnas en PL. N° 04.00

VERSIÓN : 1

PLANO N° 04.01

Aycardi Estructural

GERENTE DE PROYECTO
LUIS ENRIQUE AYCARDI F.
**MAT. 2520212794 CND**

INGENIERO
DANIEL E. QUICANO C.

MODELADOR
JUAN MANUEL SANTOS

| MODIFICACIONES | FECHA |
|---|---|
| Emisión Inicial | 13-03-2026 |
| | |
| | |
| | |
| | |
| | |

HUMANISE

Circular Lab

**HUMANISE STUDIO**

EAN-0519- AES-01-EST

Calle 71 #9-84

**DESPIECE DE COLUMNAS**

EAN-0519 -AES-01-EST-PL-508 04.01

REVISOR ESTRUCTURAL
JULIO CESAR SANMIGUEL CAMACHO
MAT. 25202-57738 CND

PLANO N° 04.01 VERSIÓN : 1